

APD




2024


EMIE GUGLIELMO

MEMOIRE PROJET
PROFESSIONNEL


PLAN DÉMOLITION ET
CONSTRUCTION
REZ-DE-CHAUSSÉE

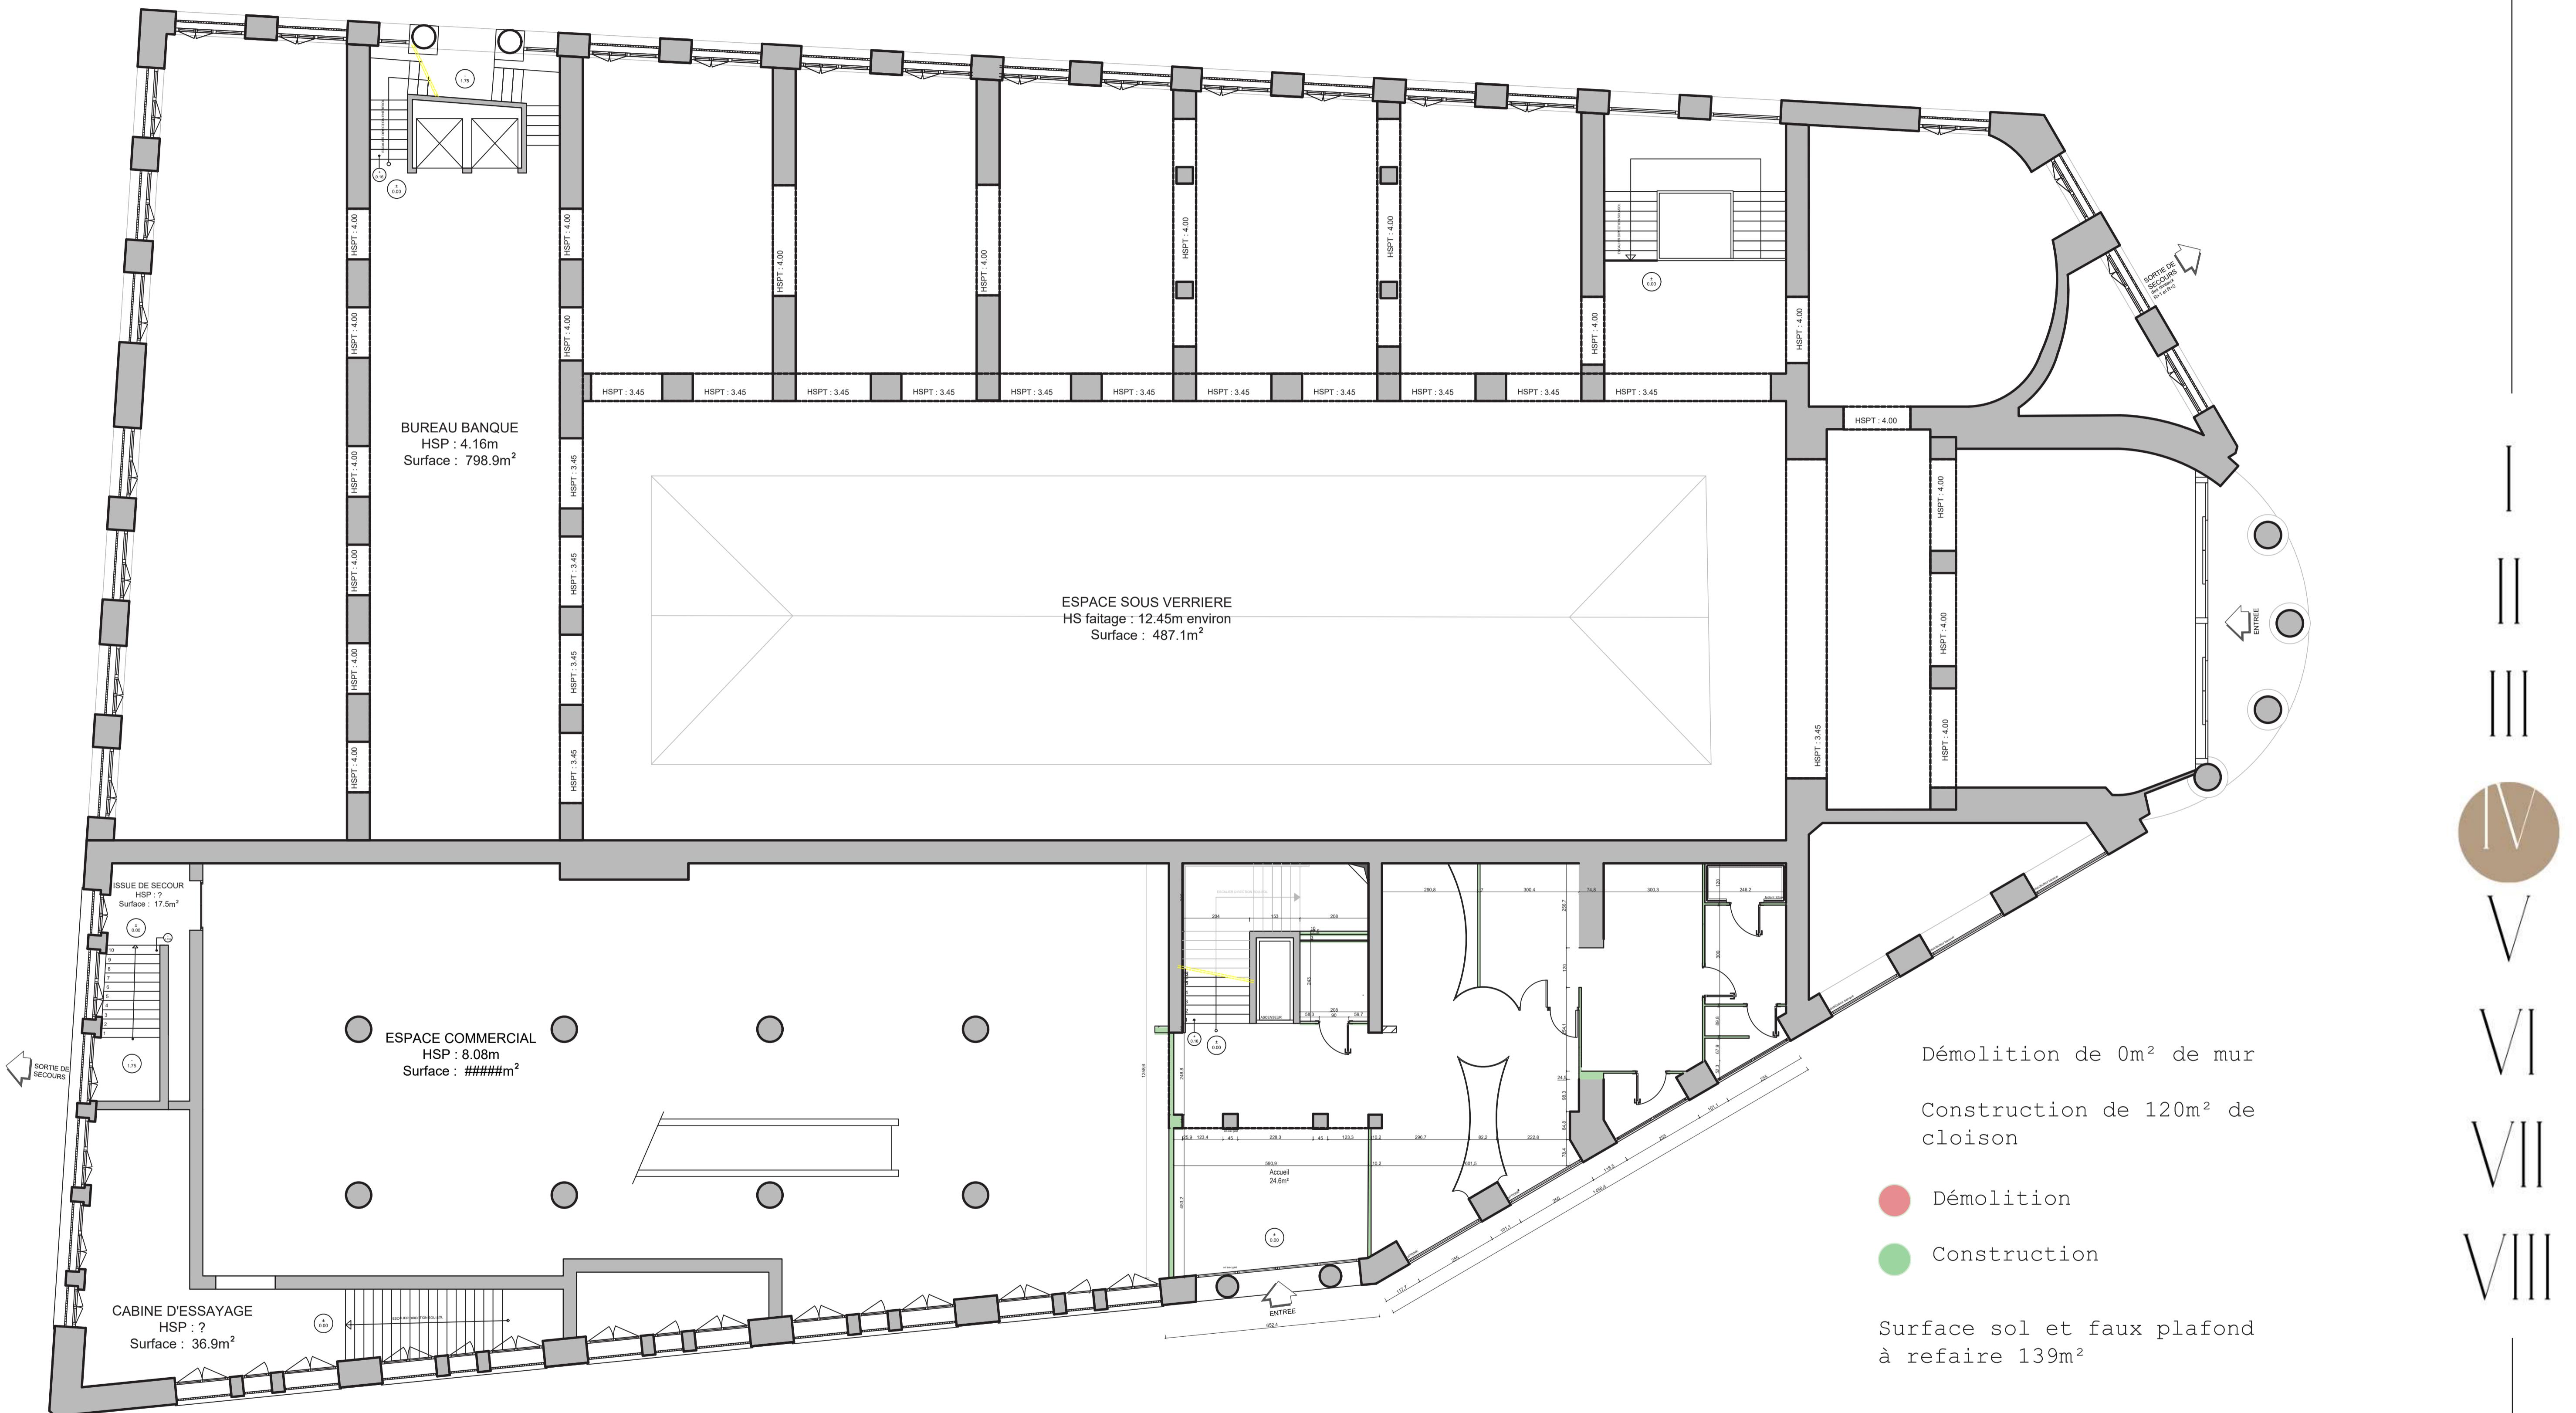


PLAN DÉMOLITION ET
CONSTRUCTION
1ER ÉTAGE

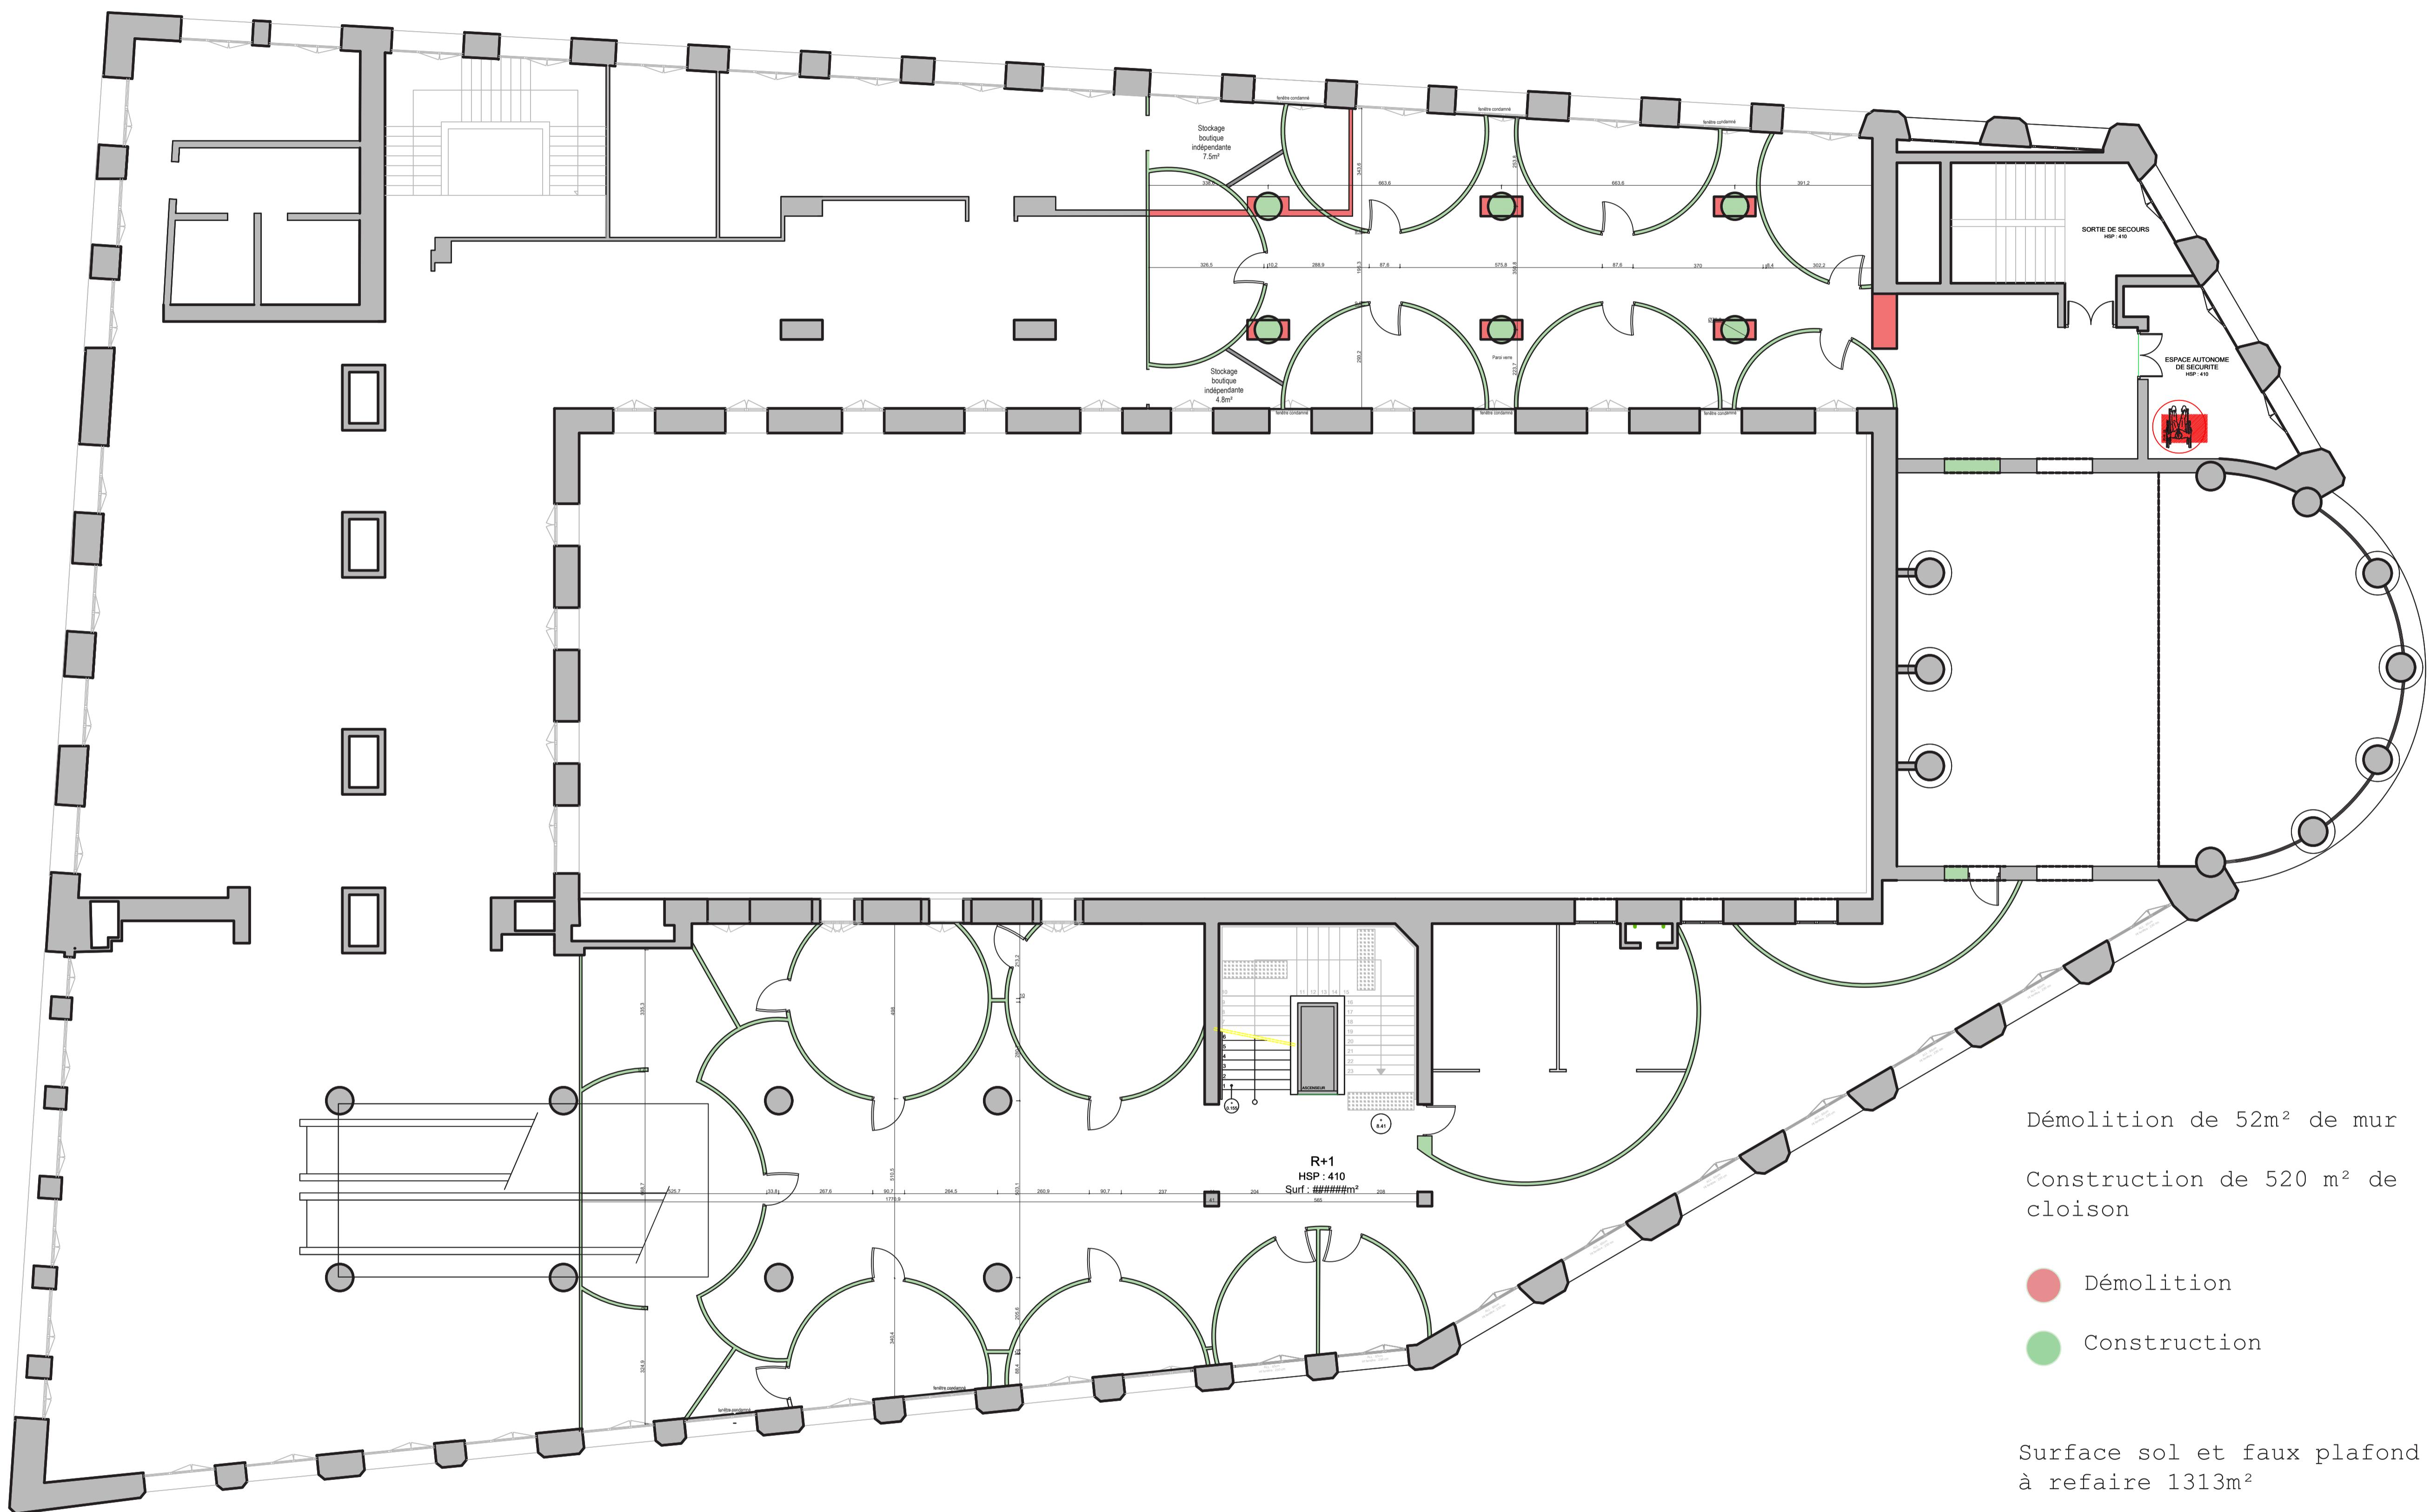

PLAN DÉMOLITION ET CONSTRUCTION 2E ÉTAGE

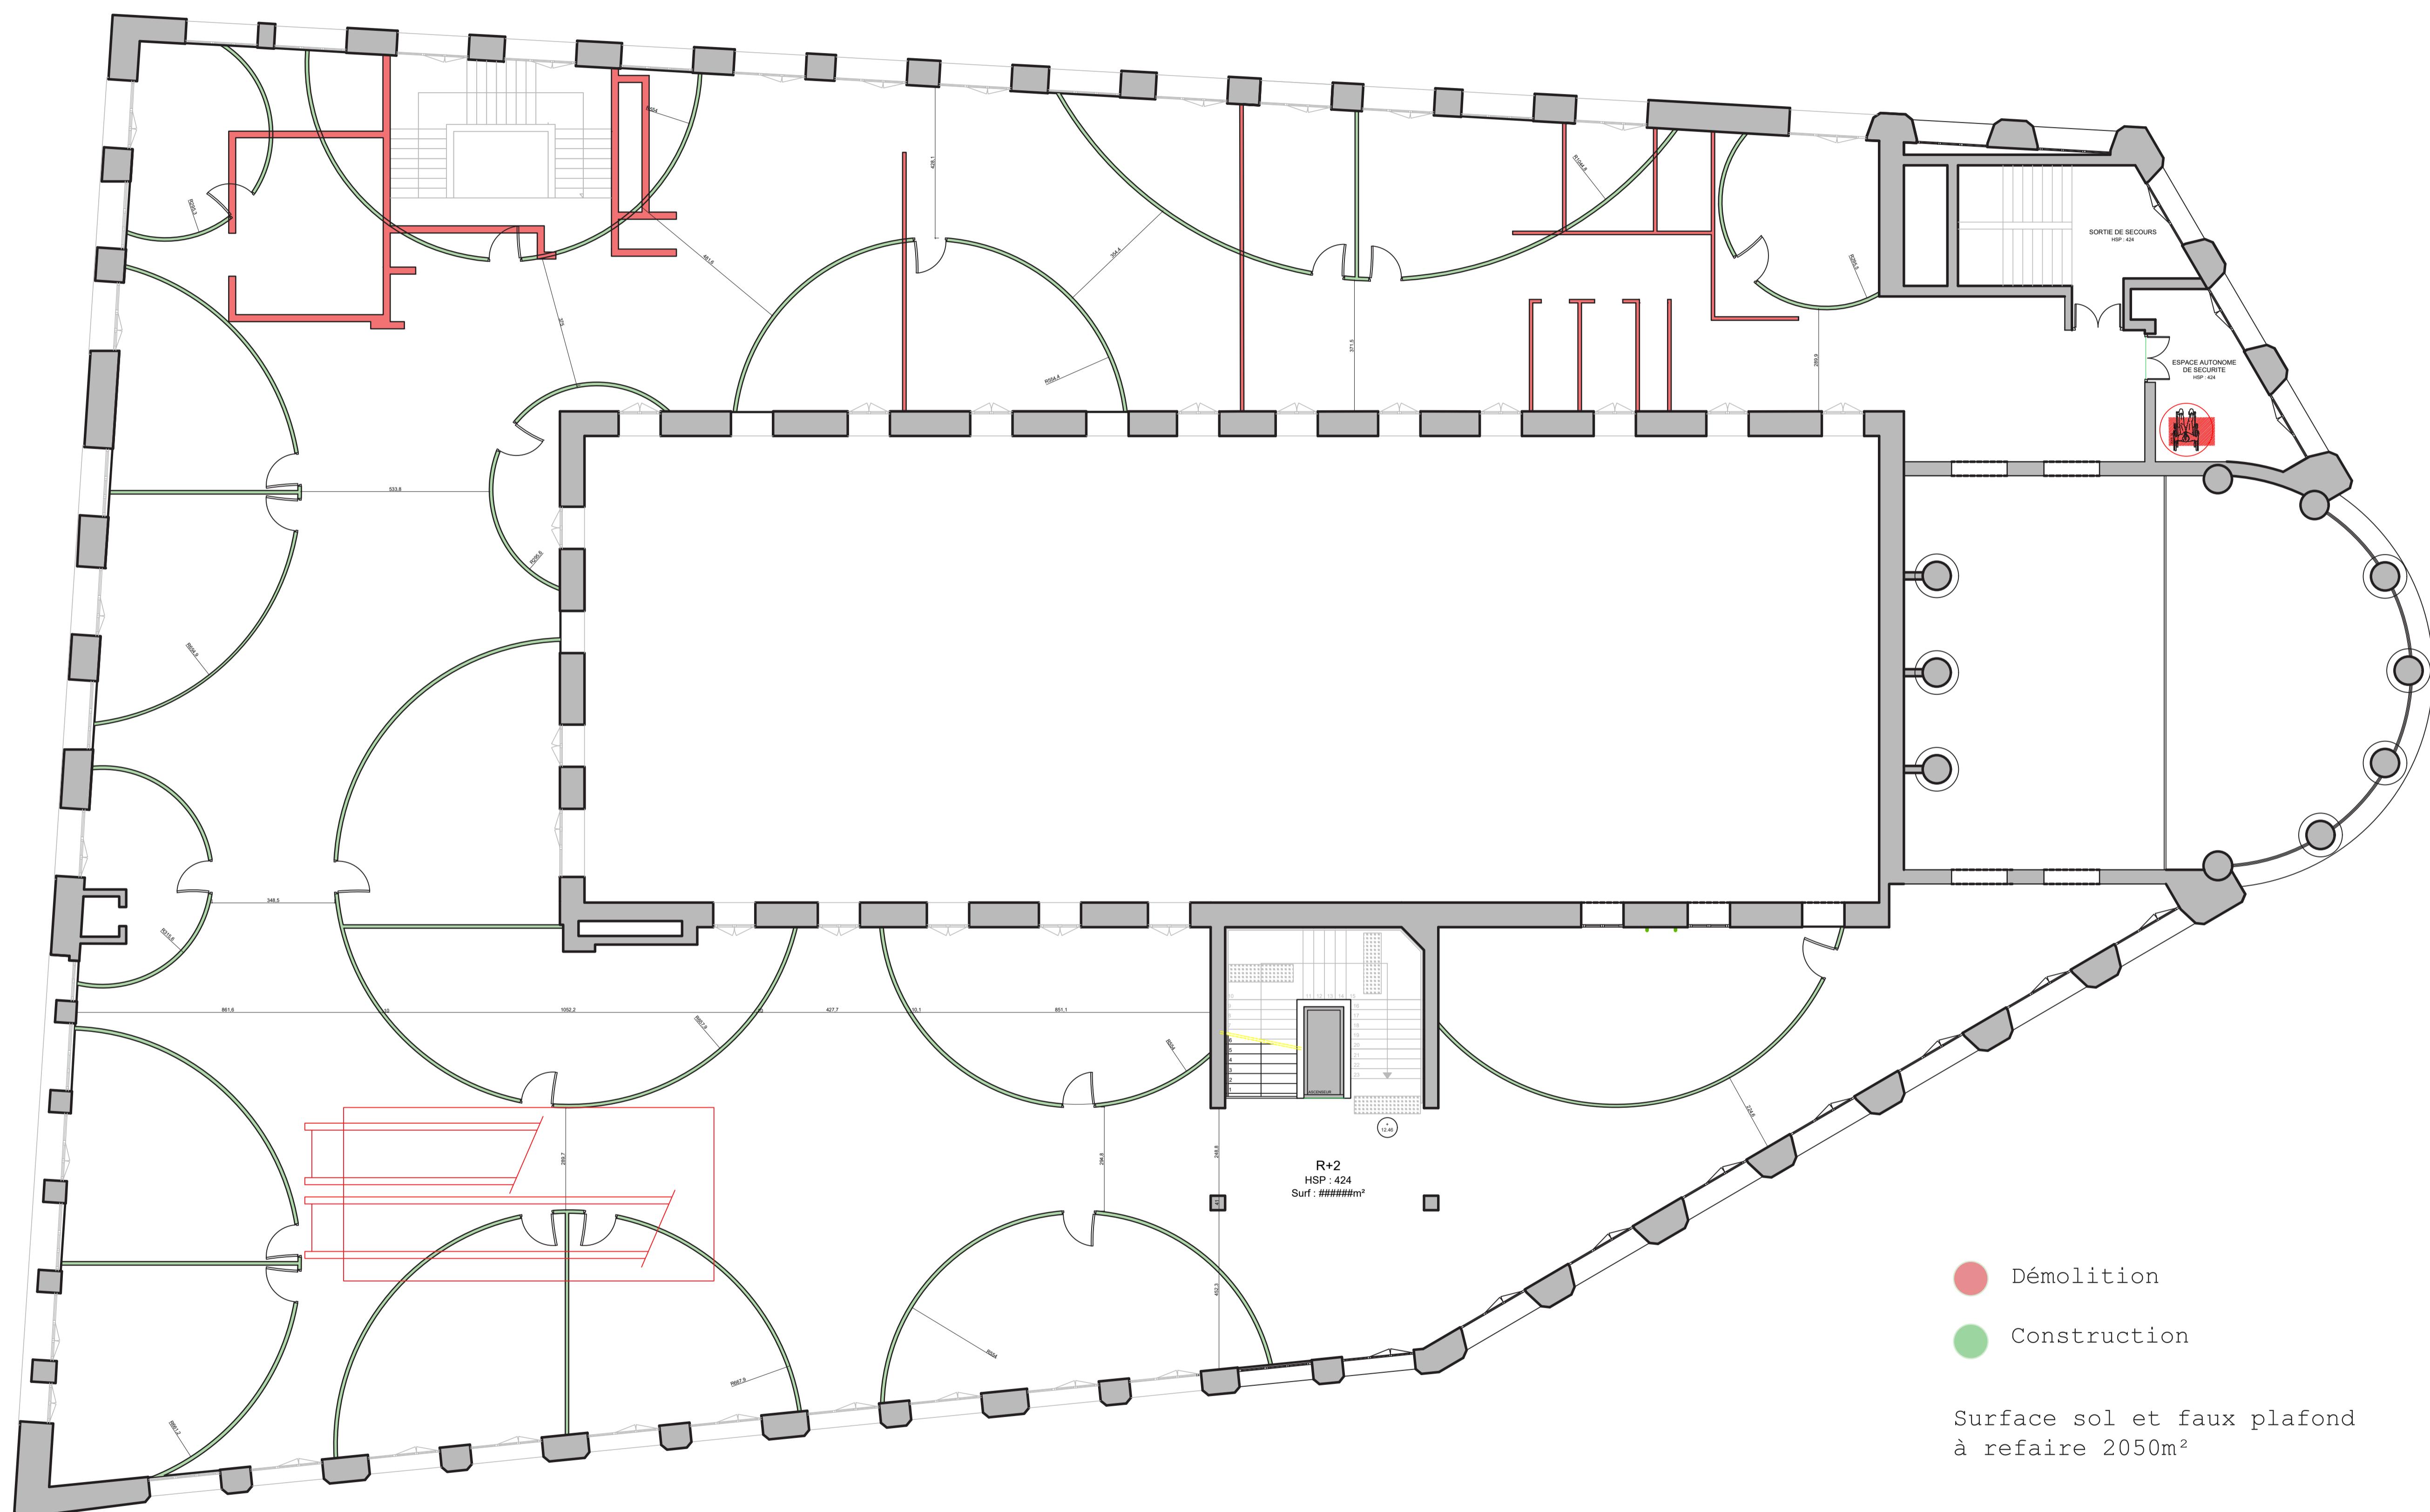


PLAN GÉNÉRAL REZ-DE-CHAUSSÉE

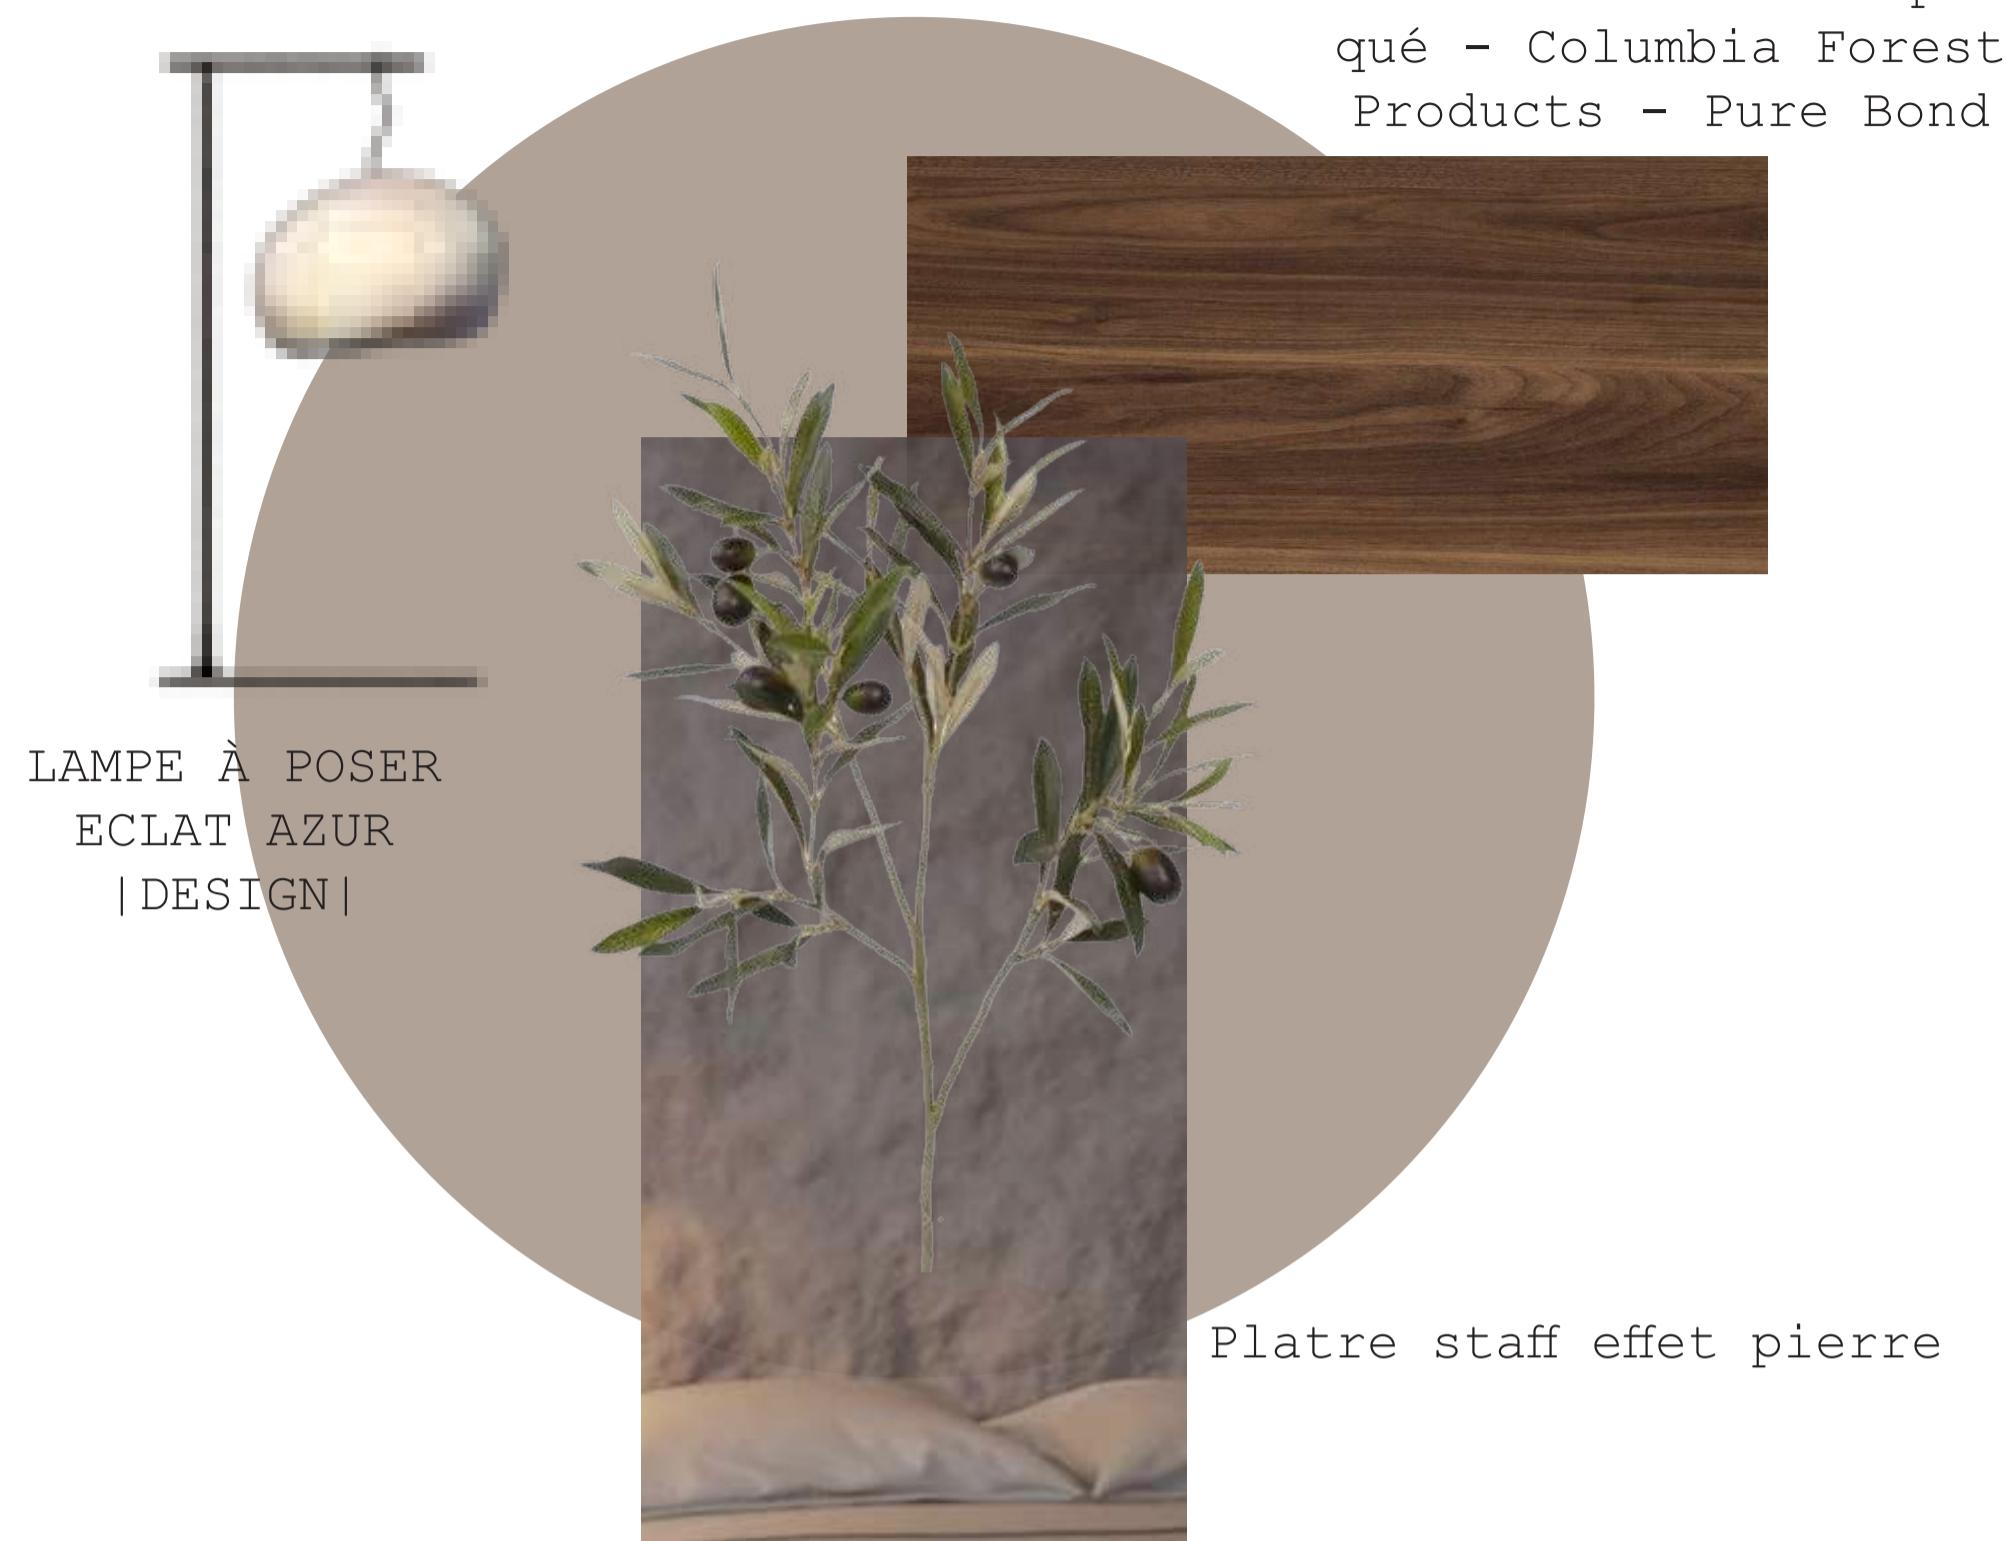


CHAISE DE SALLE À MANGER EN LIN BLANC | ANDREW MARTIN MAGNUS




CELESTINE | TABLE
ARRONDIE | APEZA

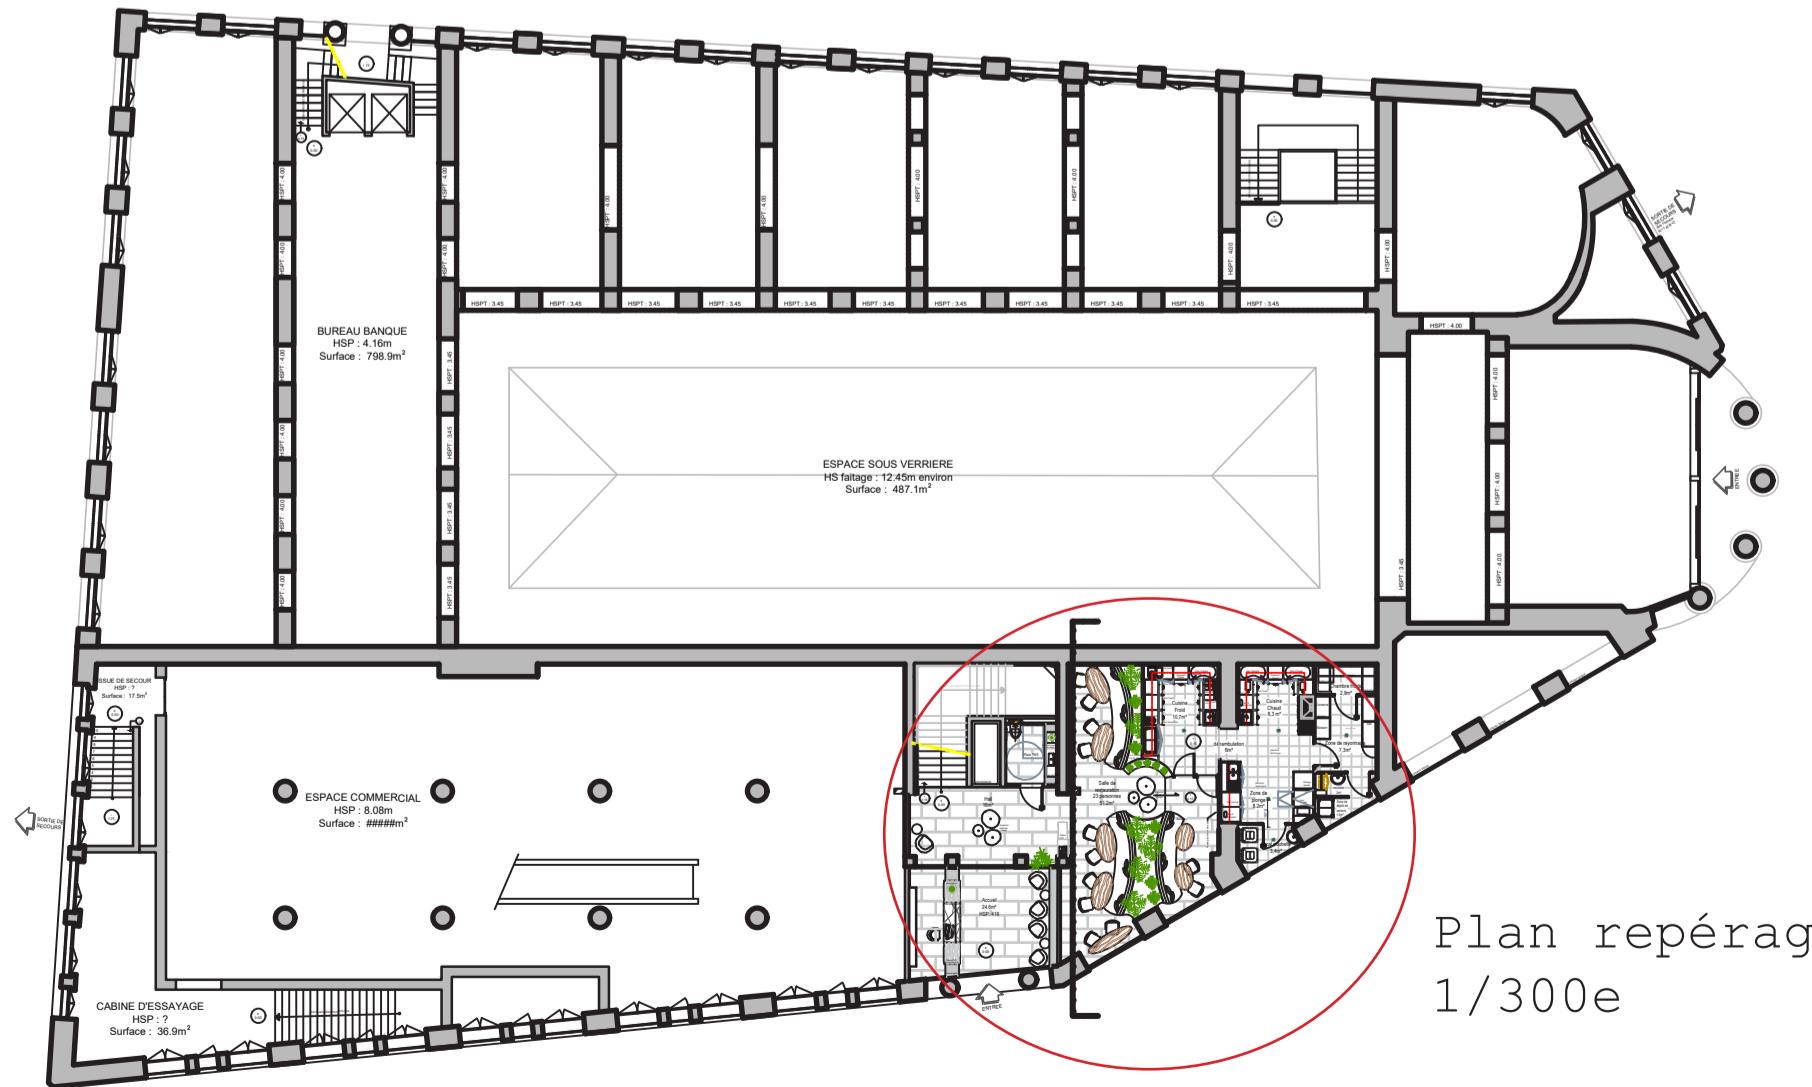

Plan repérage

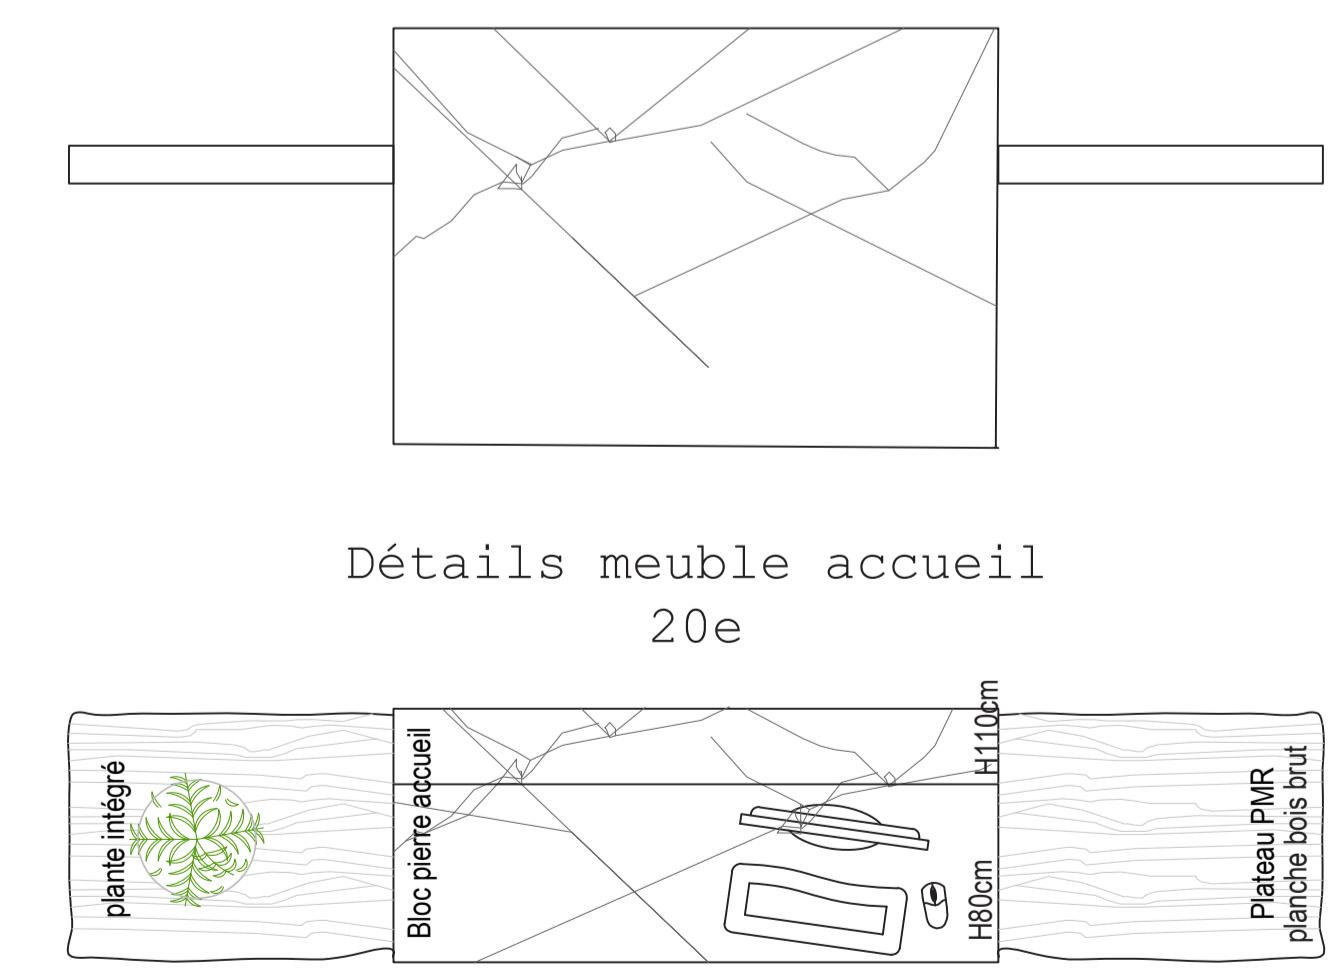


Détails meuble accueil 20e

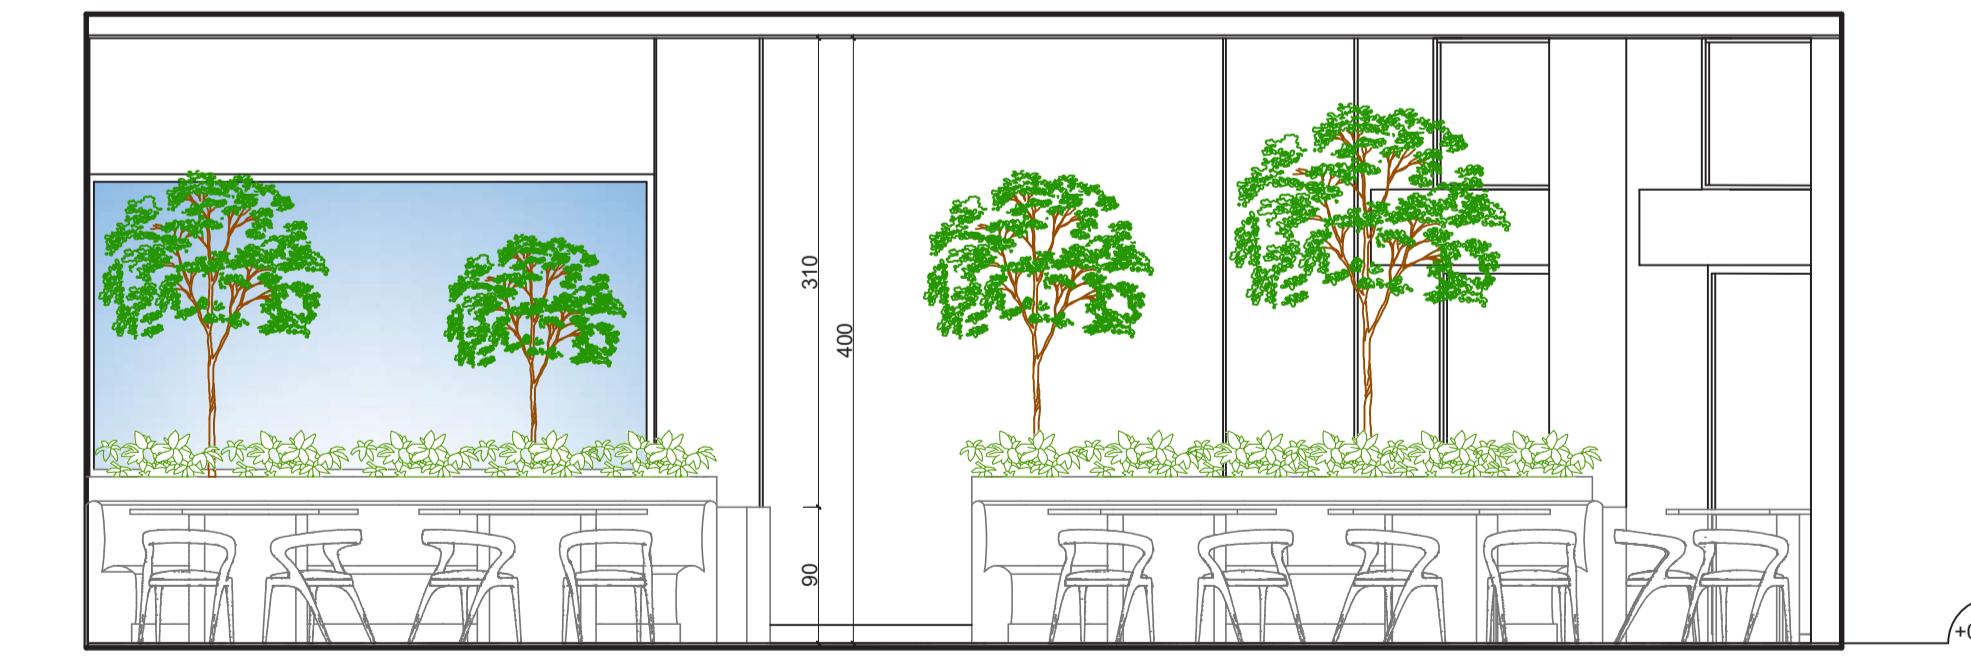

Coupe AA'

PLAN GÉNÉRAL 1ER ÉTAGE

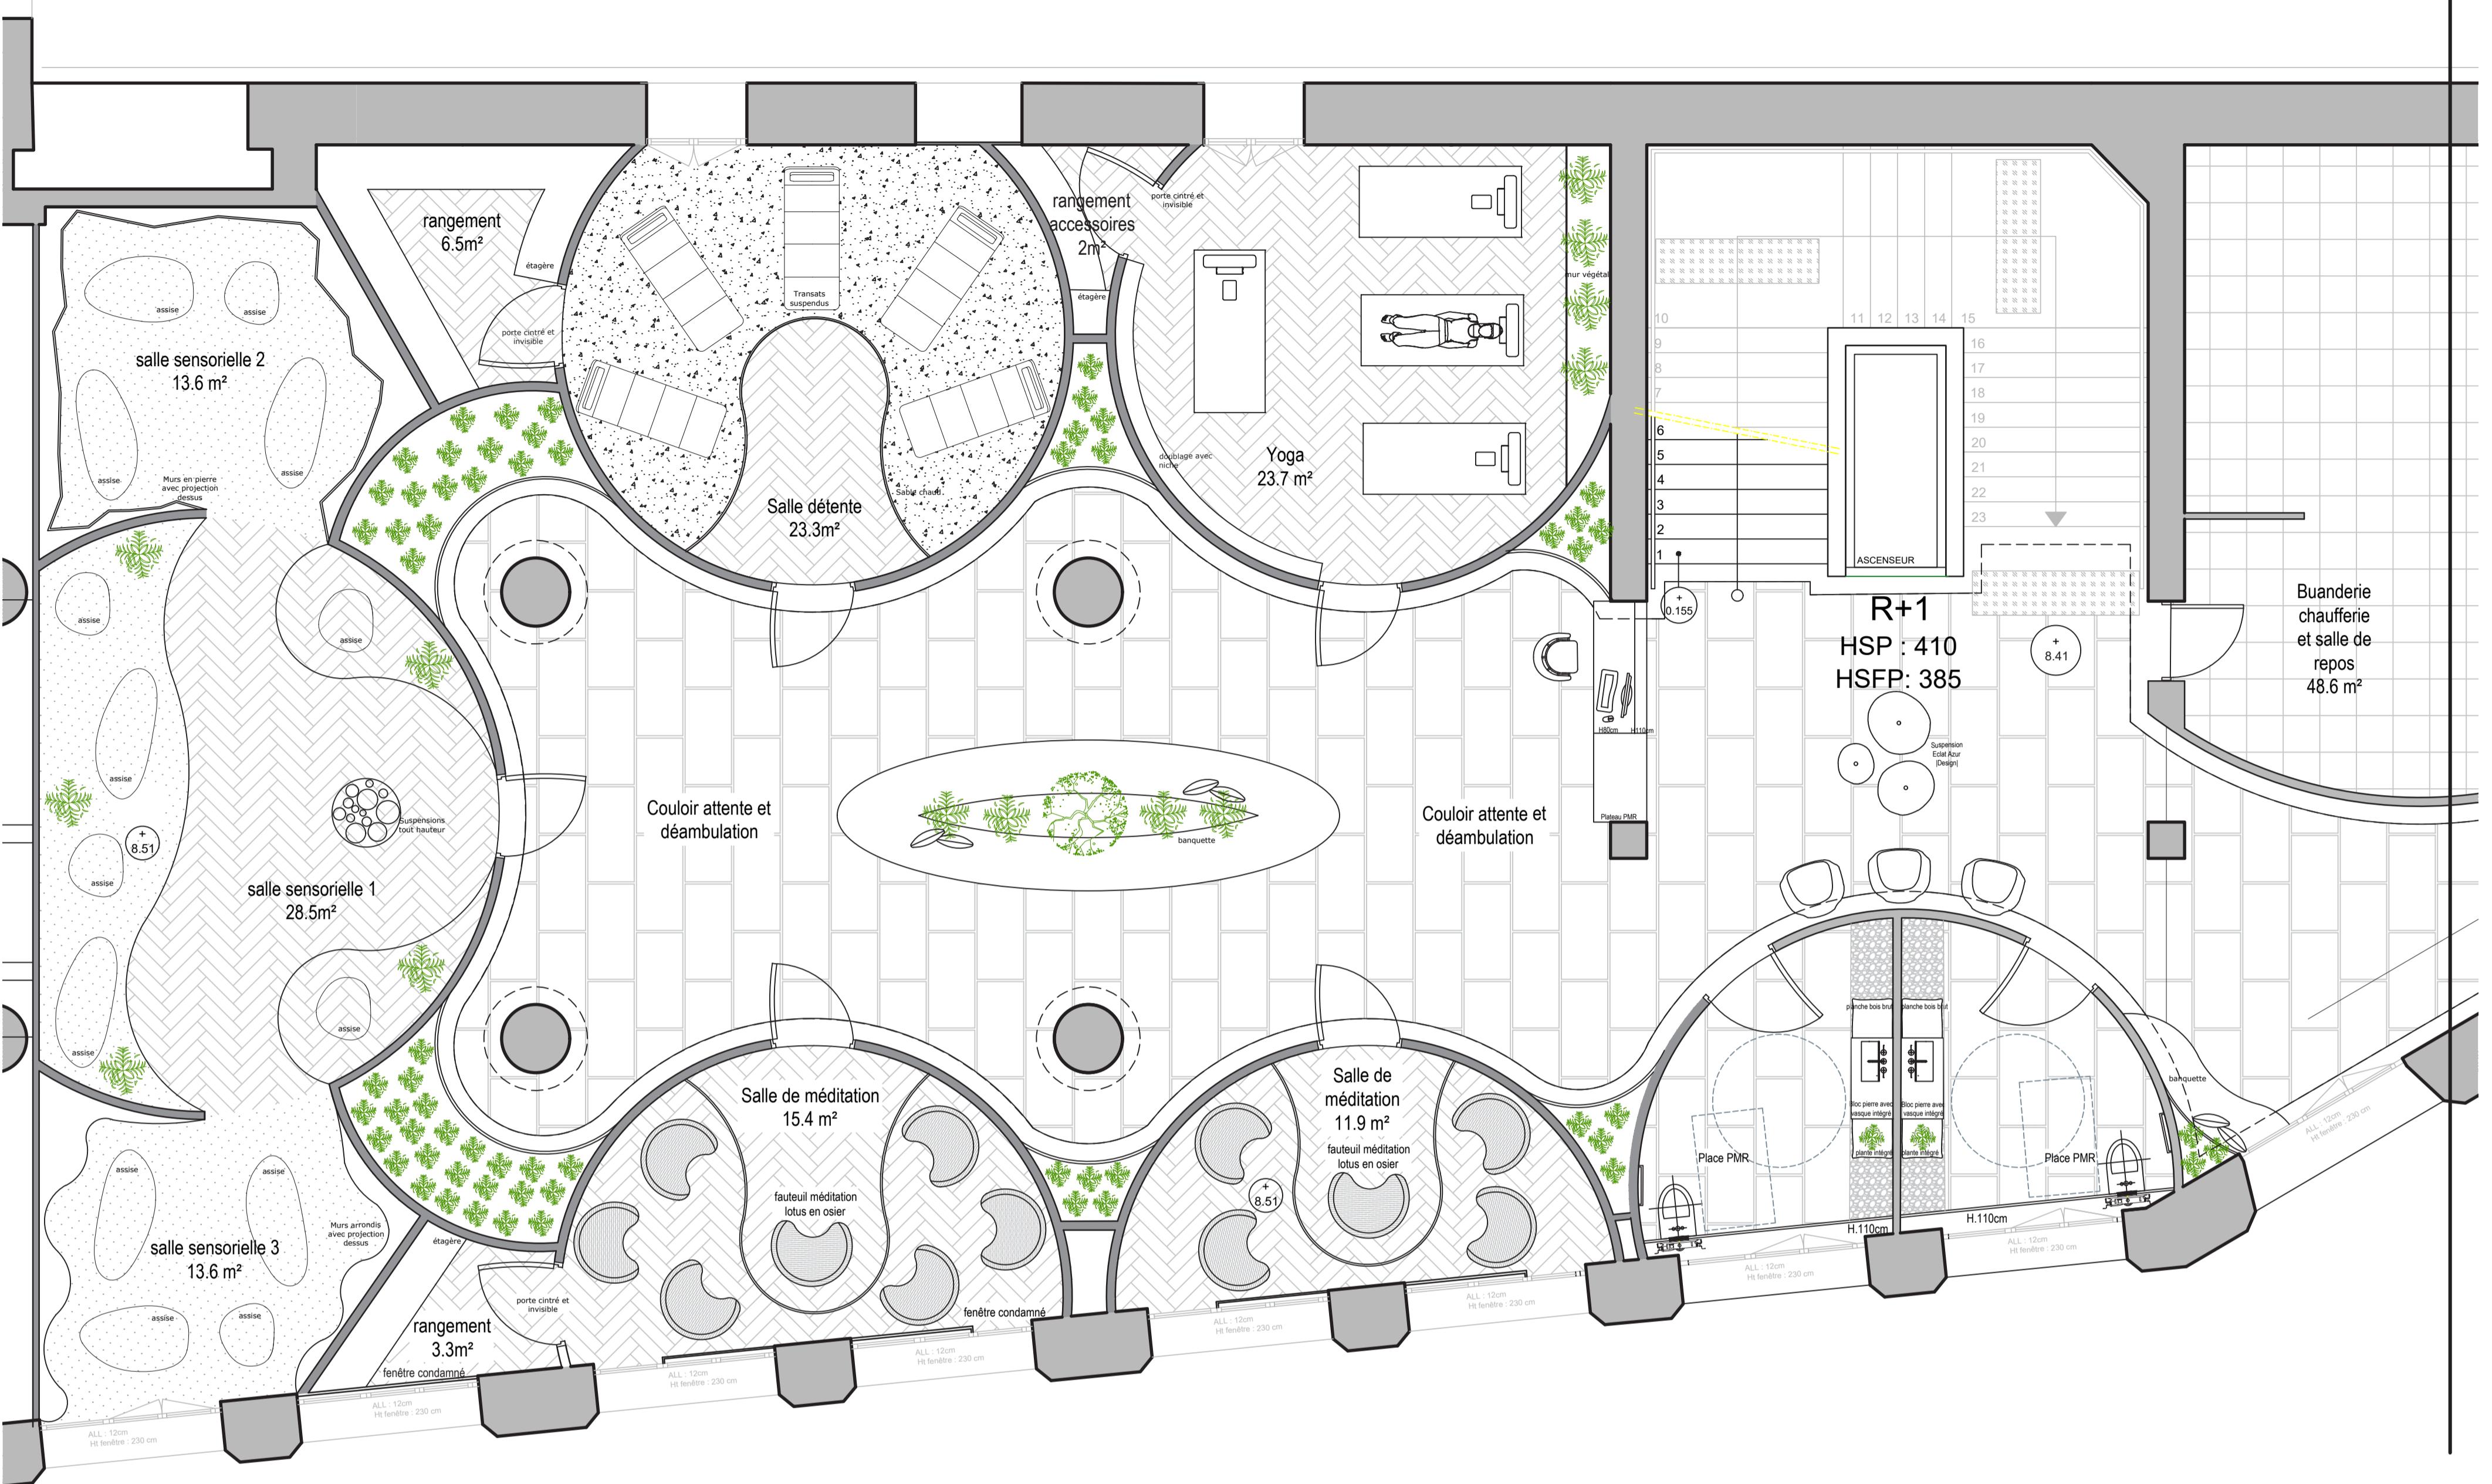

Fauteuil Lotus - Nature & Découvertes | Chaise méditation





Tapis de Yoga écolo-gique luxe en liège na-turel



Lit Hamac Suspendu




Galet Pouf & mobilier design | Poufs de Giorgetti

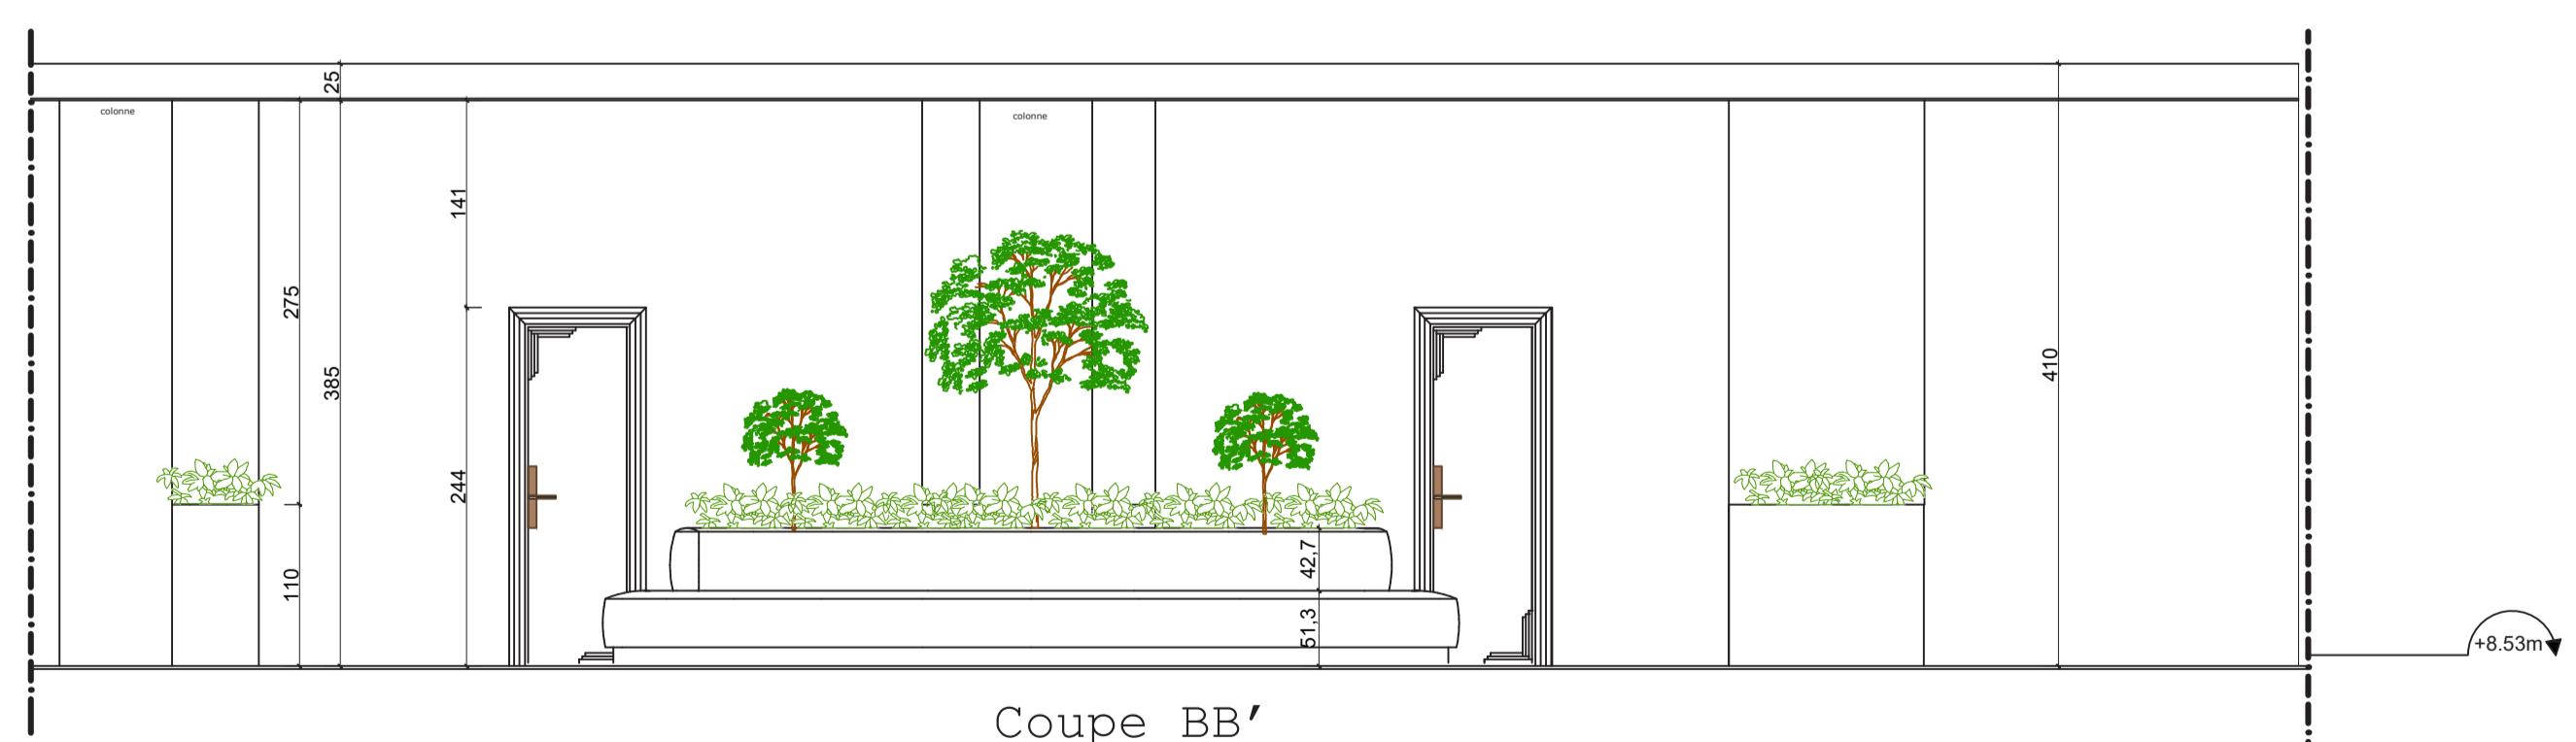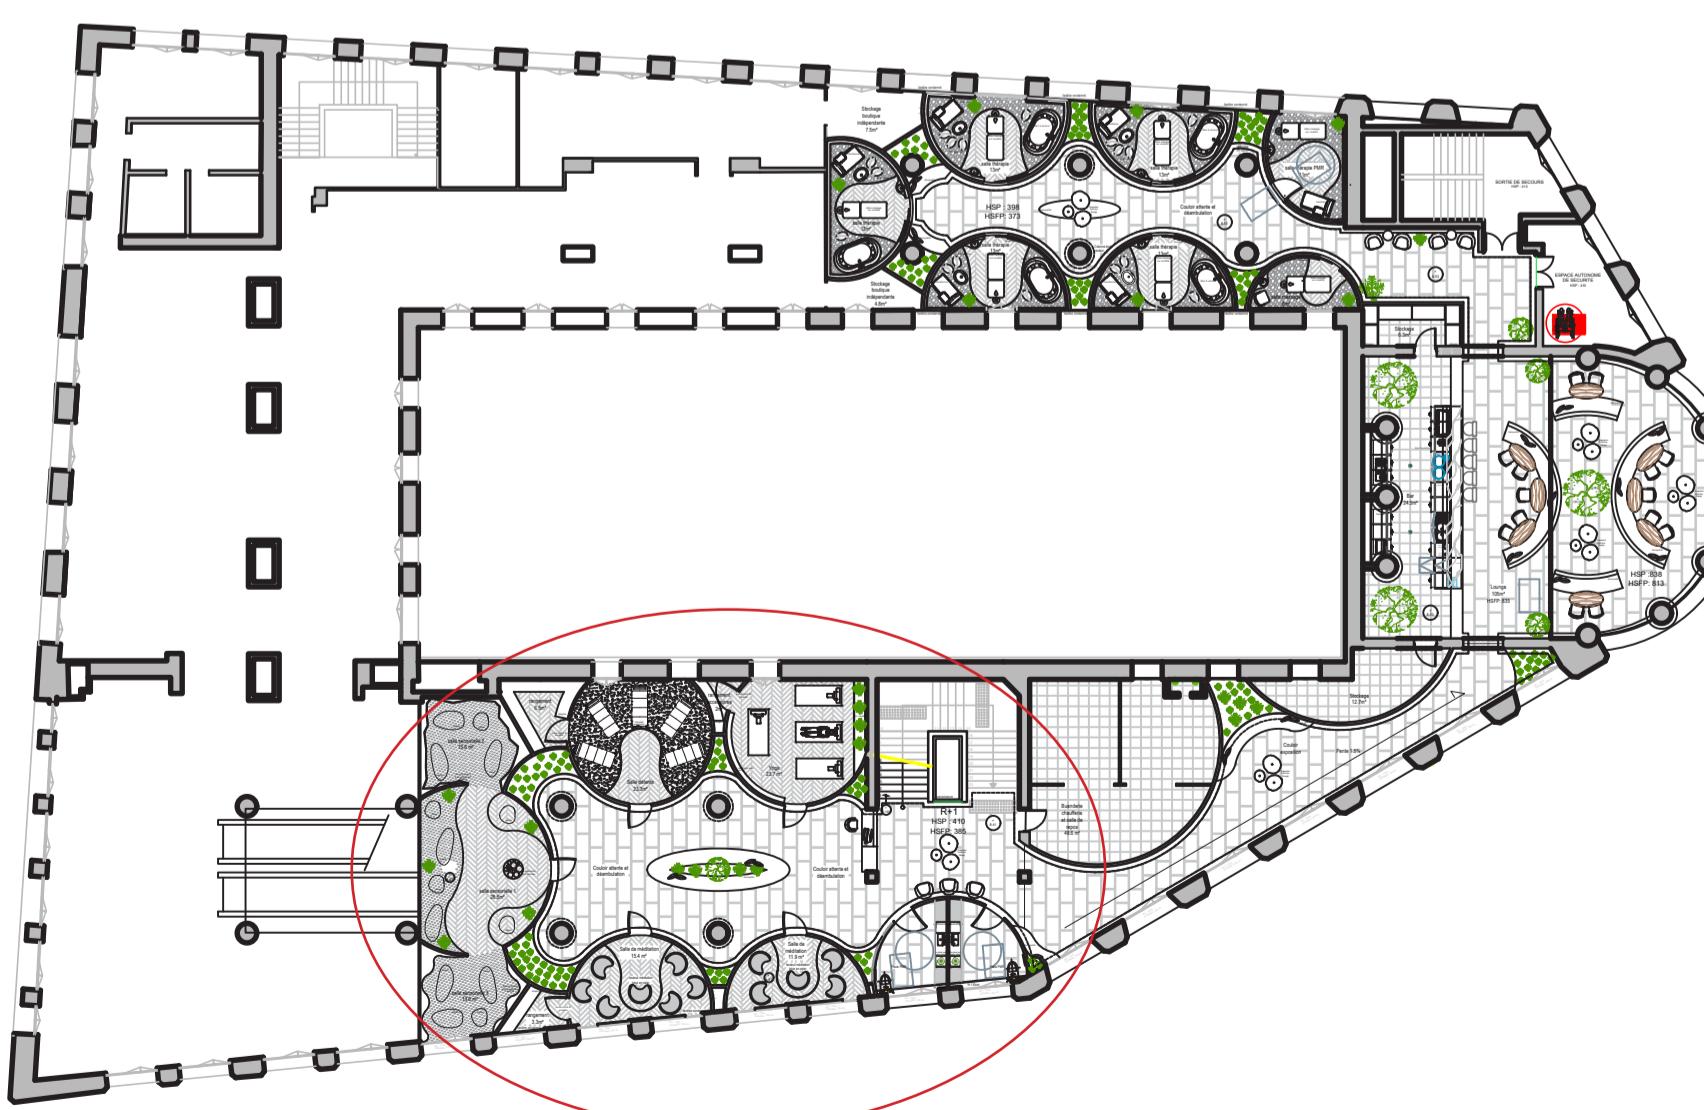

Sensory Haven

PLAN GÉNÉRAL 1ER ÉTAGE

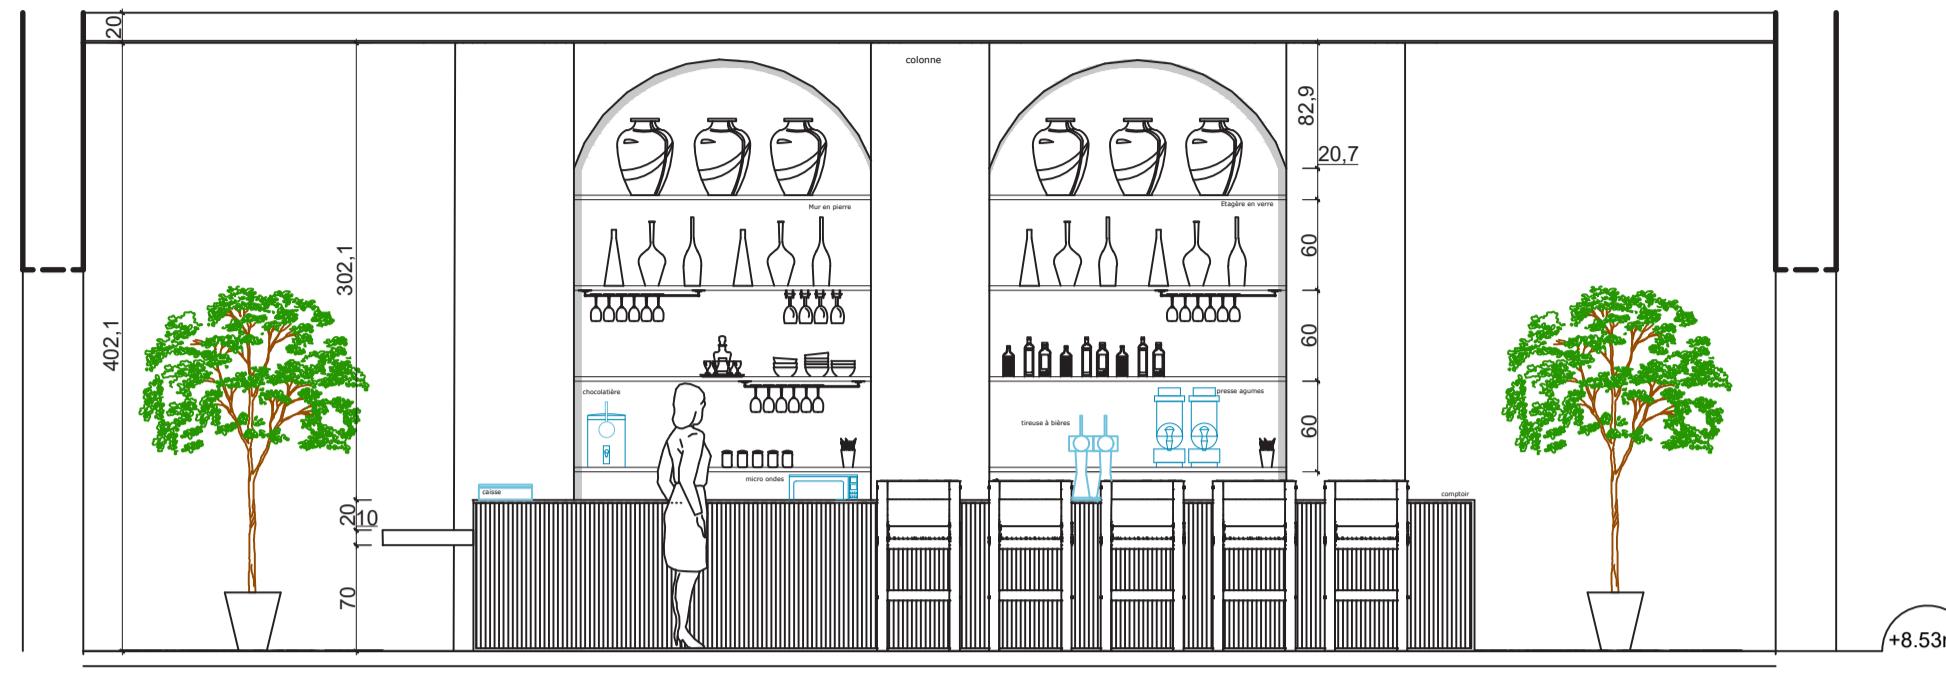

Coupe C




Platre staf
effet pierre



Bar en travertin | CU- PASTONE PIERRES DISTRIBUTION


BLINDE DESIGN BARSTOOL SITE B19

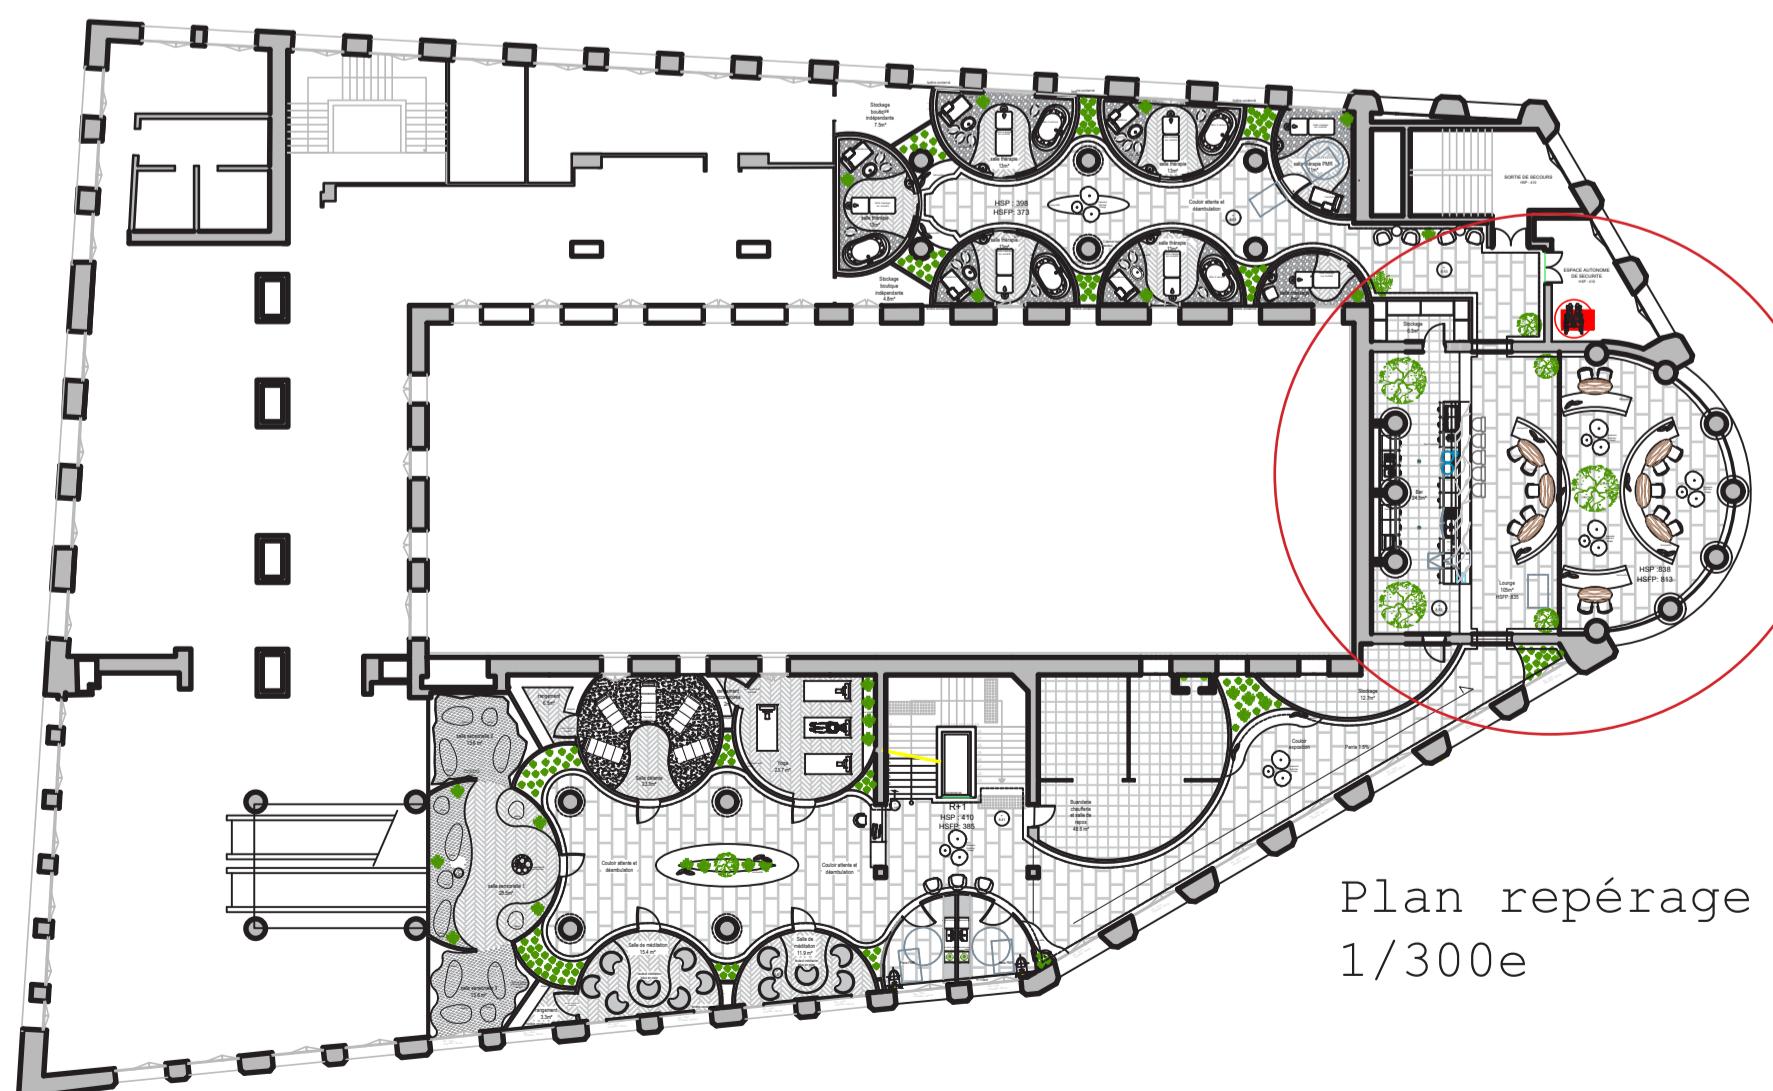

Plan repérage
1/300e



BANQUETTE EN
TOILE DE LIN
BEIGE | STOF

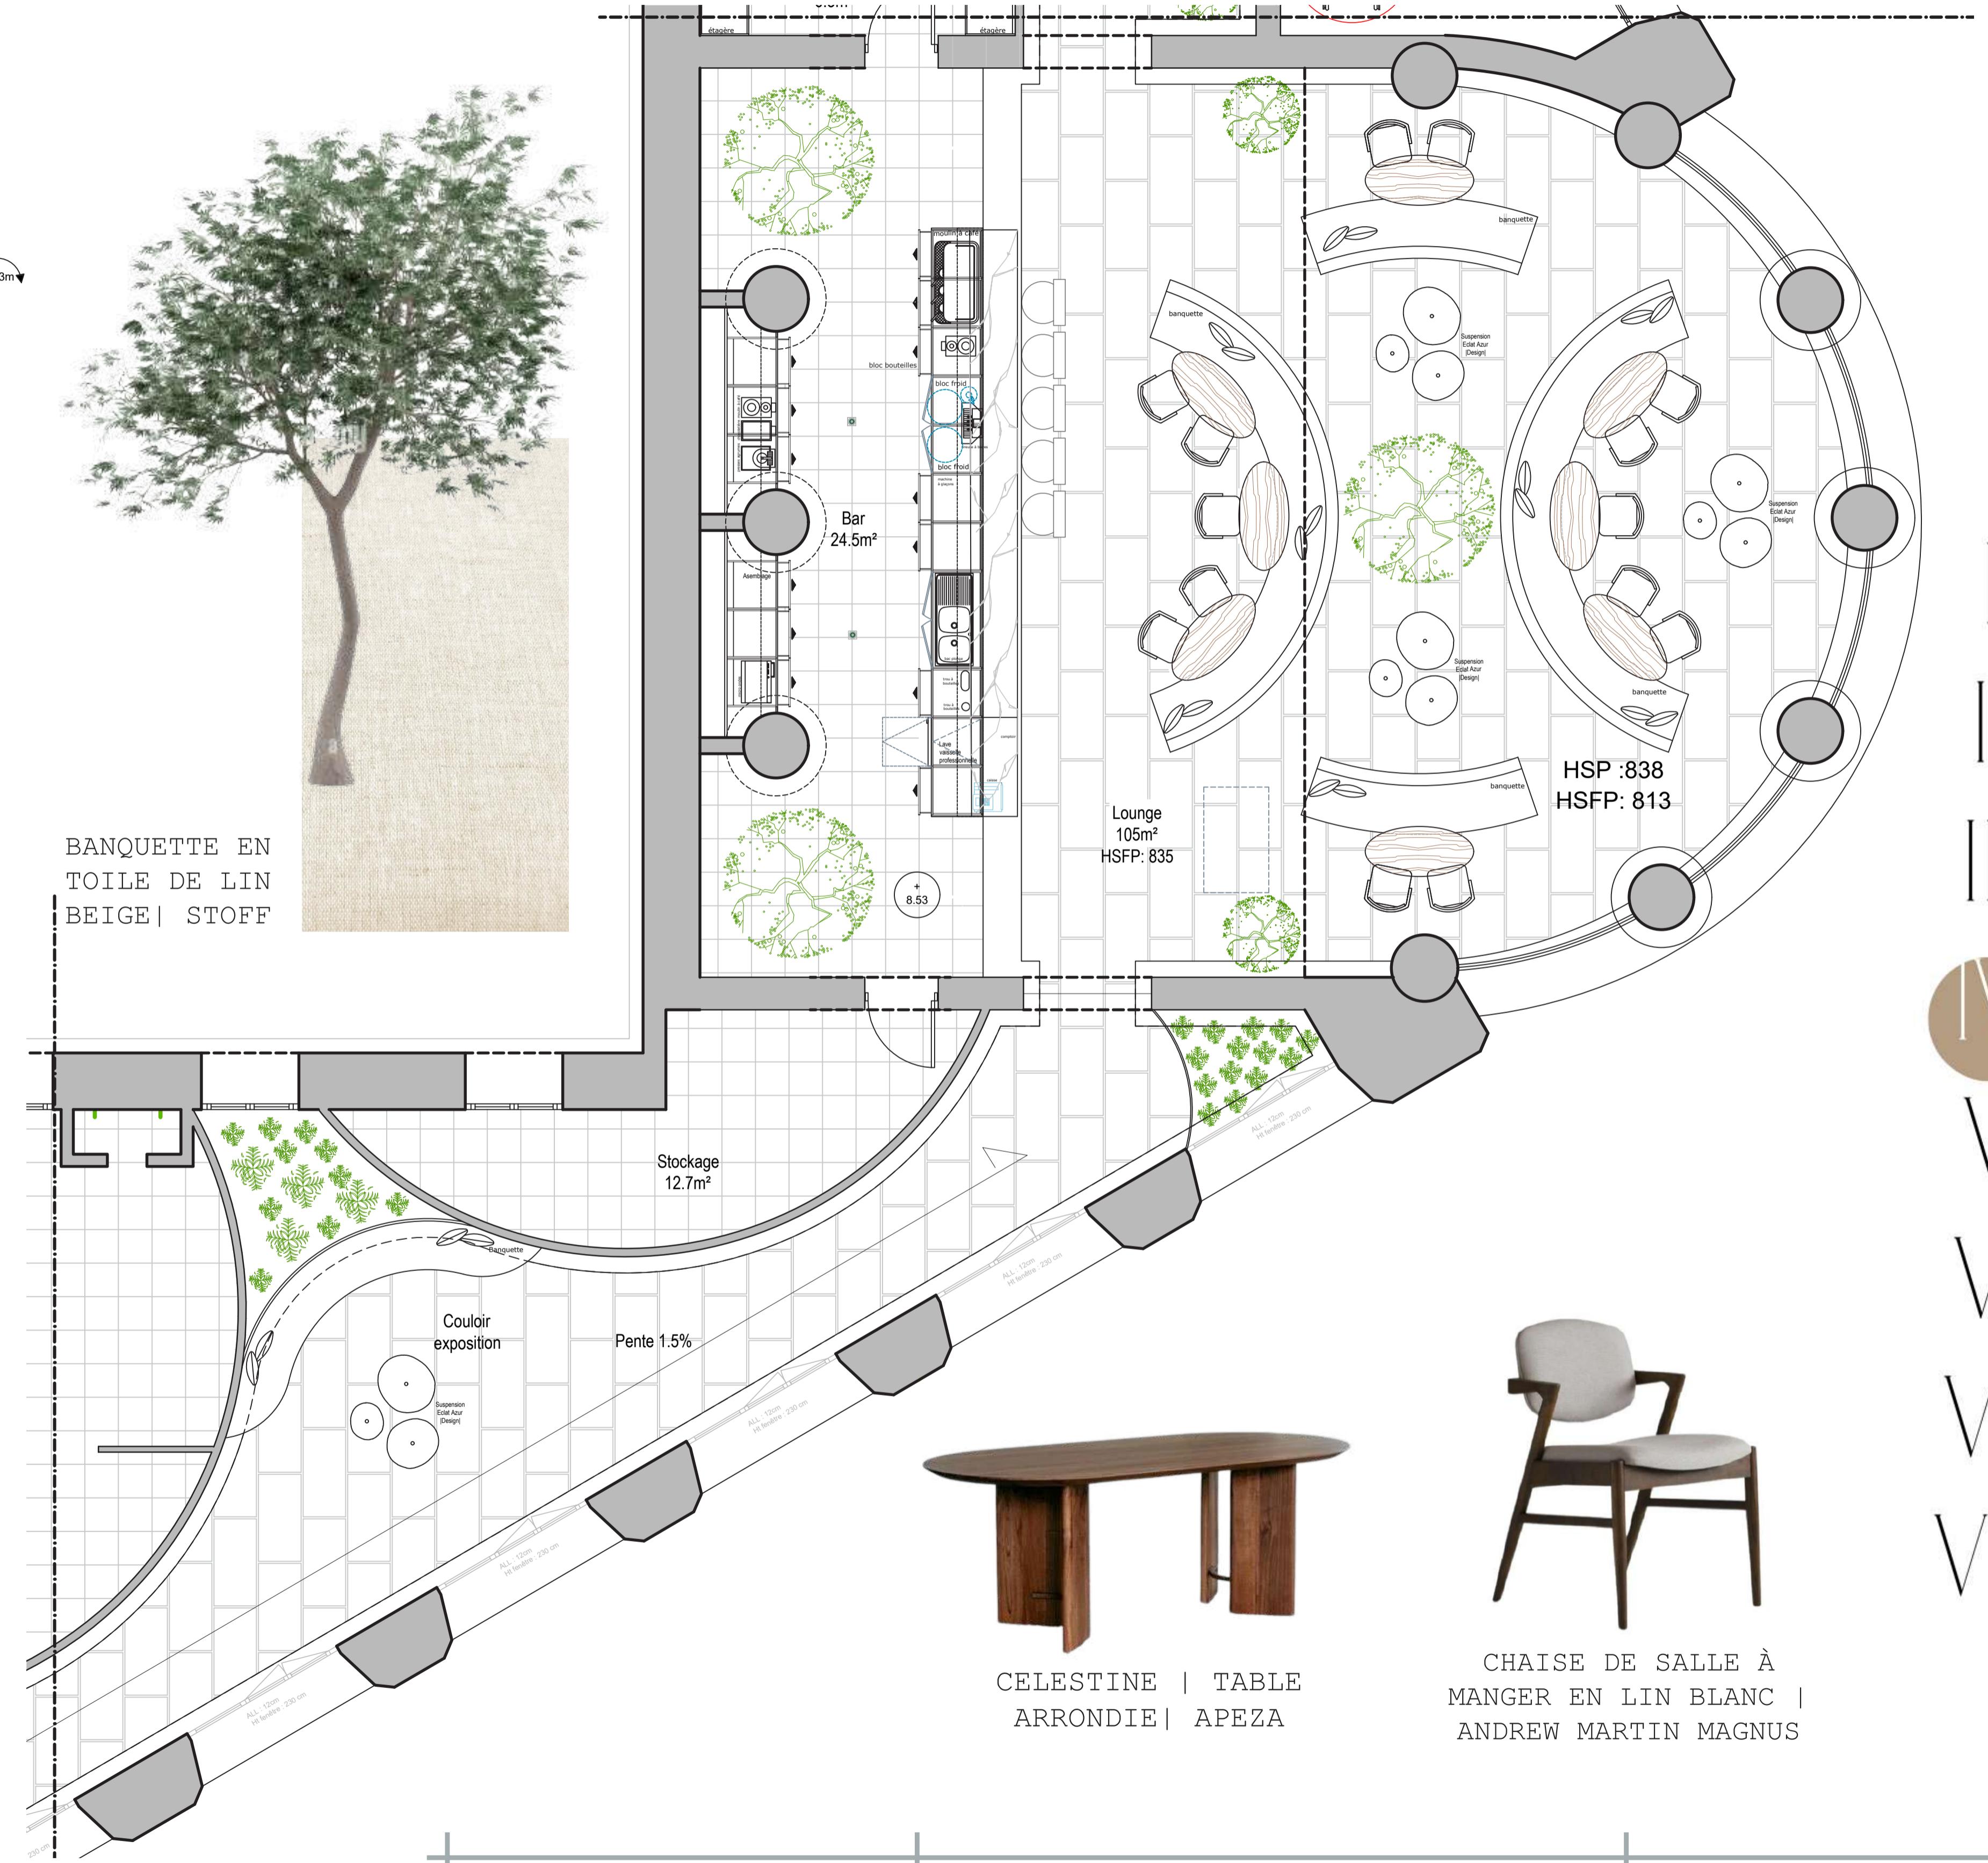

A1- 1/50e
2024
N°017



Sensory Haven

Plan général

PLAN GÉNÉRAL
1ER ÉTAGE

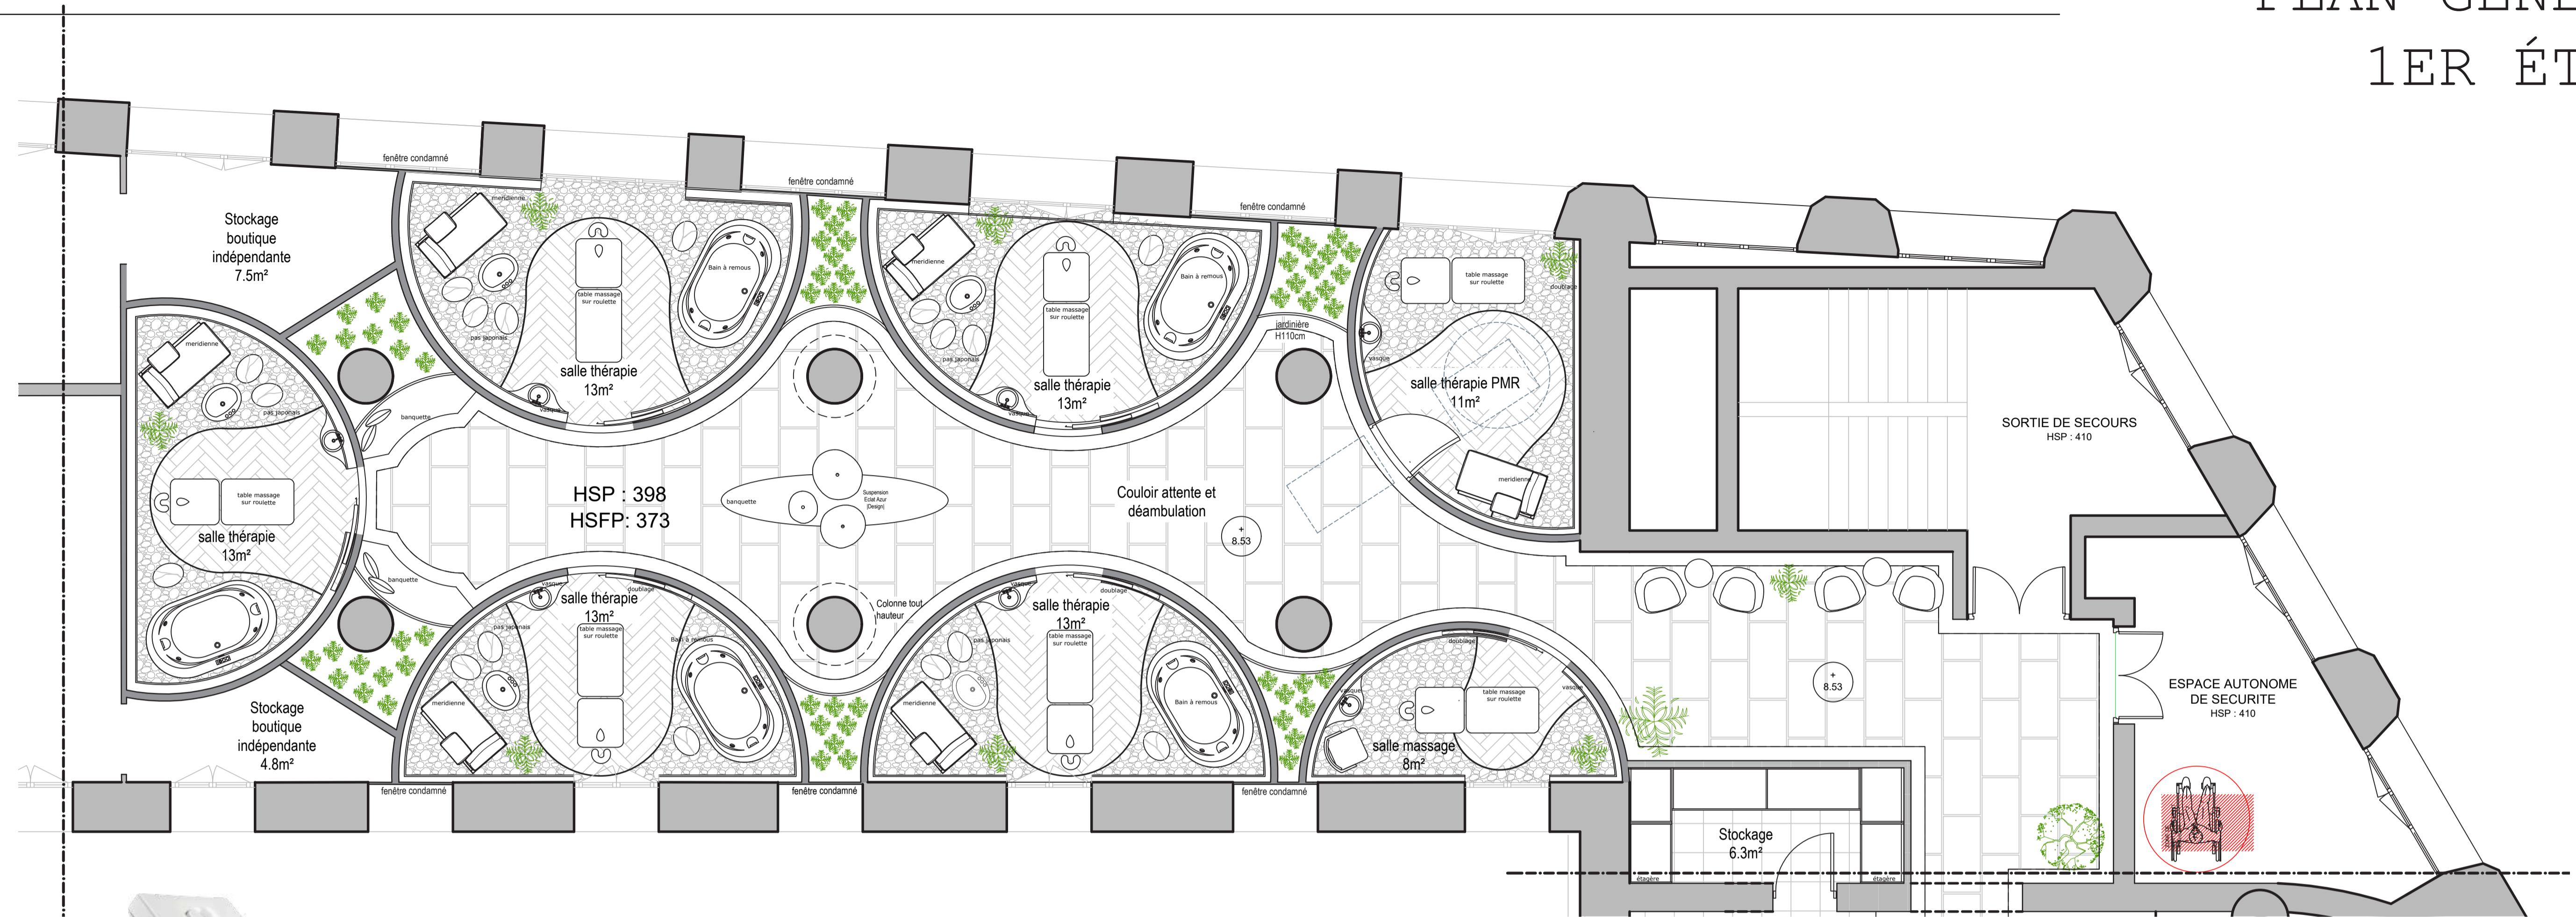



TABLE DE MASSAGE | ES-
THETIC DESIGN




BAIGNOIRE BALNÉO ÎLOT AU SOL -
LOFT - DISCOUNT-PLOMBERIE




BAYSIDE - MÉRIDIENNE GAUCHE OU
BAIN DE SOLEIL MODULABLE

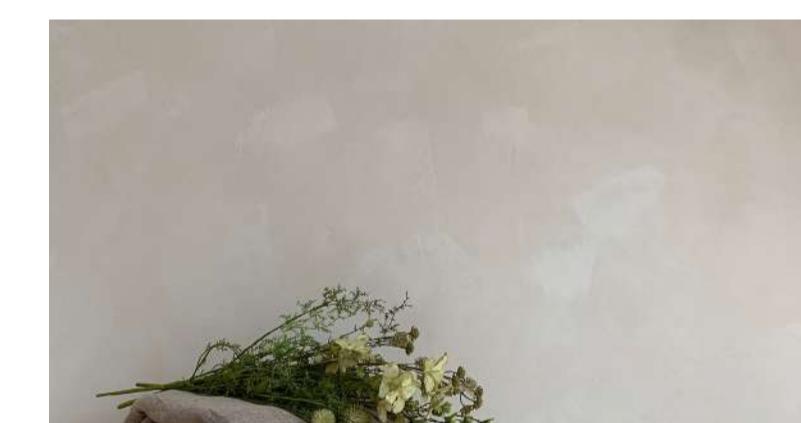


Peinture naturelle à la
chaux | couleur blanc vieil-
li

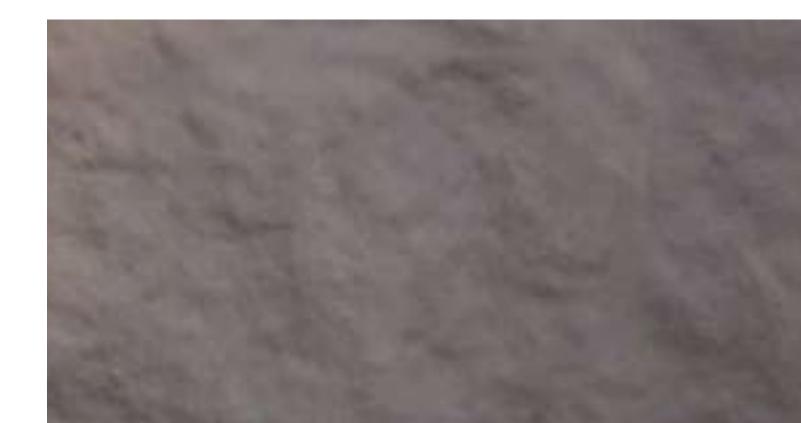

Platre staff
effet pierre

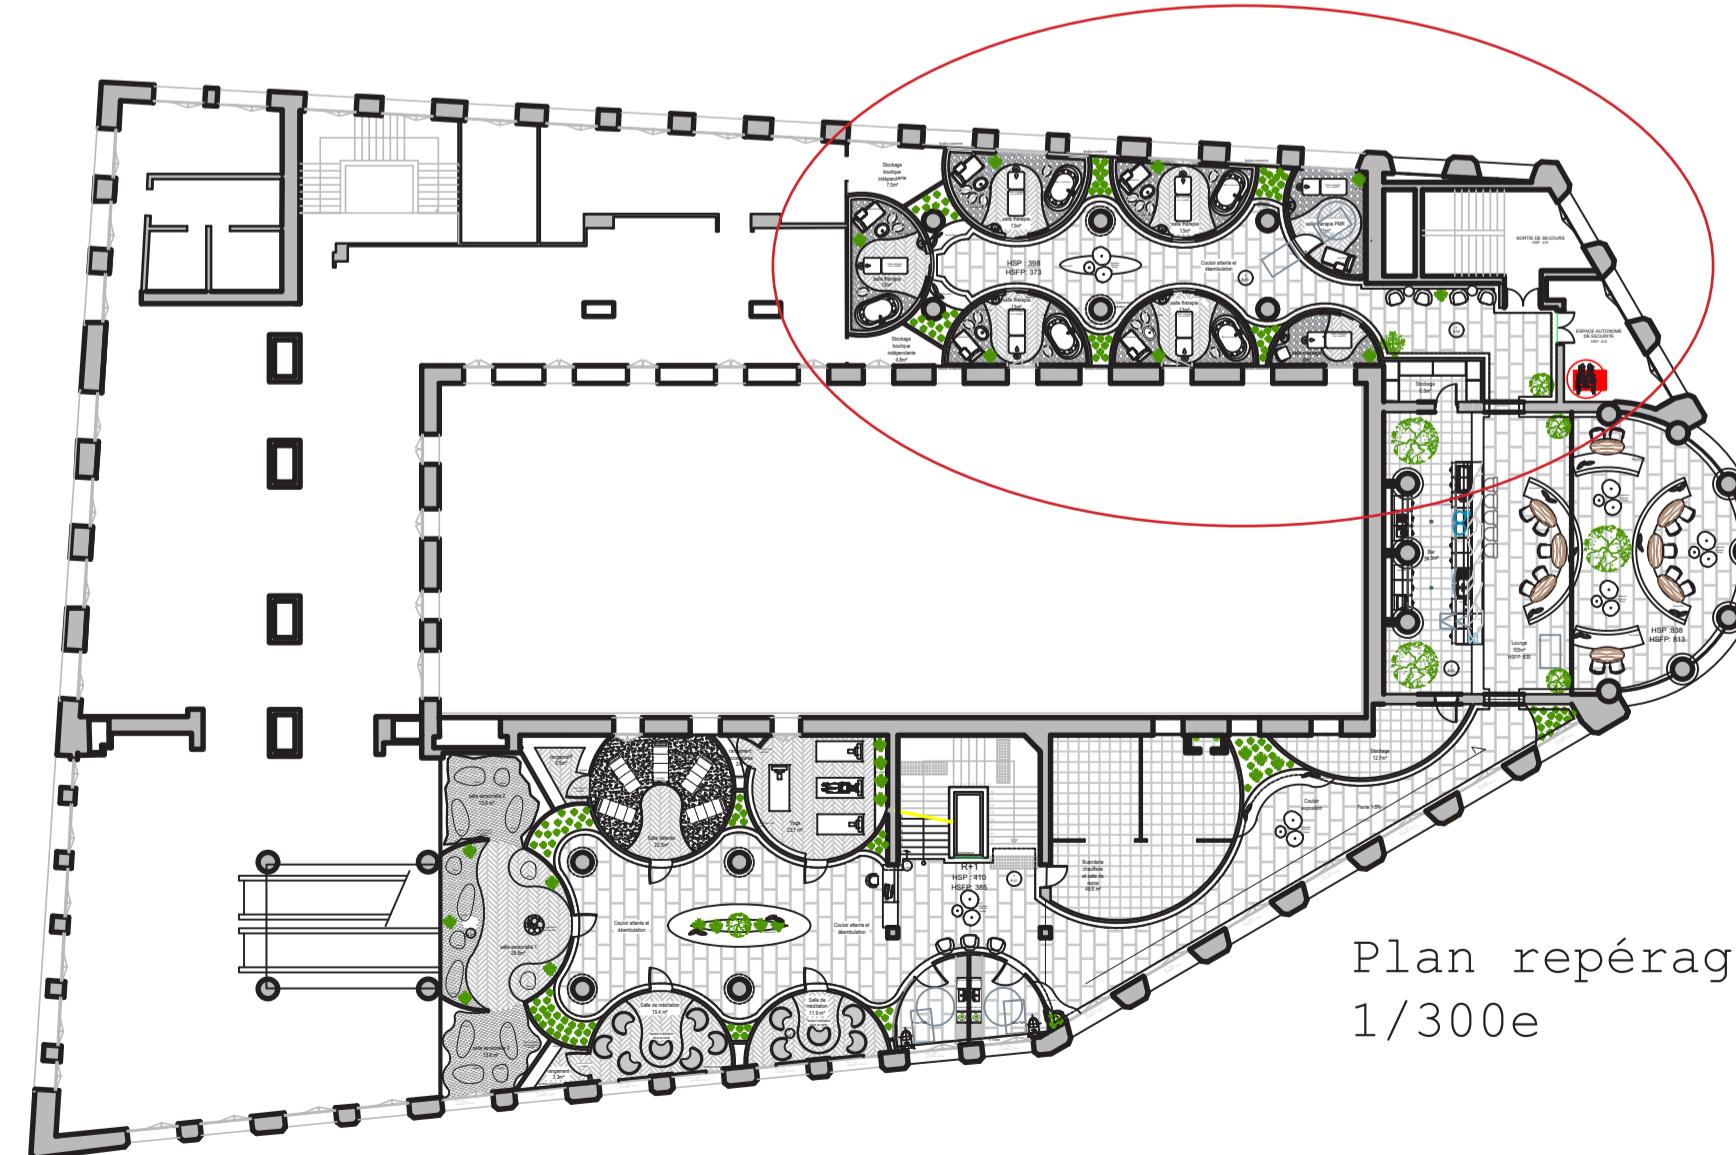


Plan repérage
1/300e

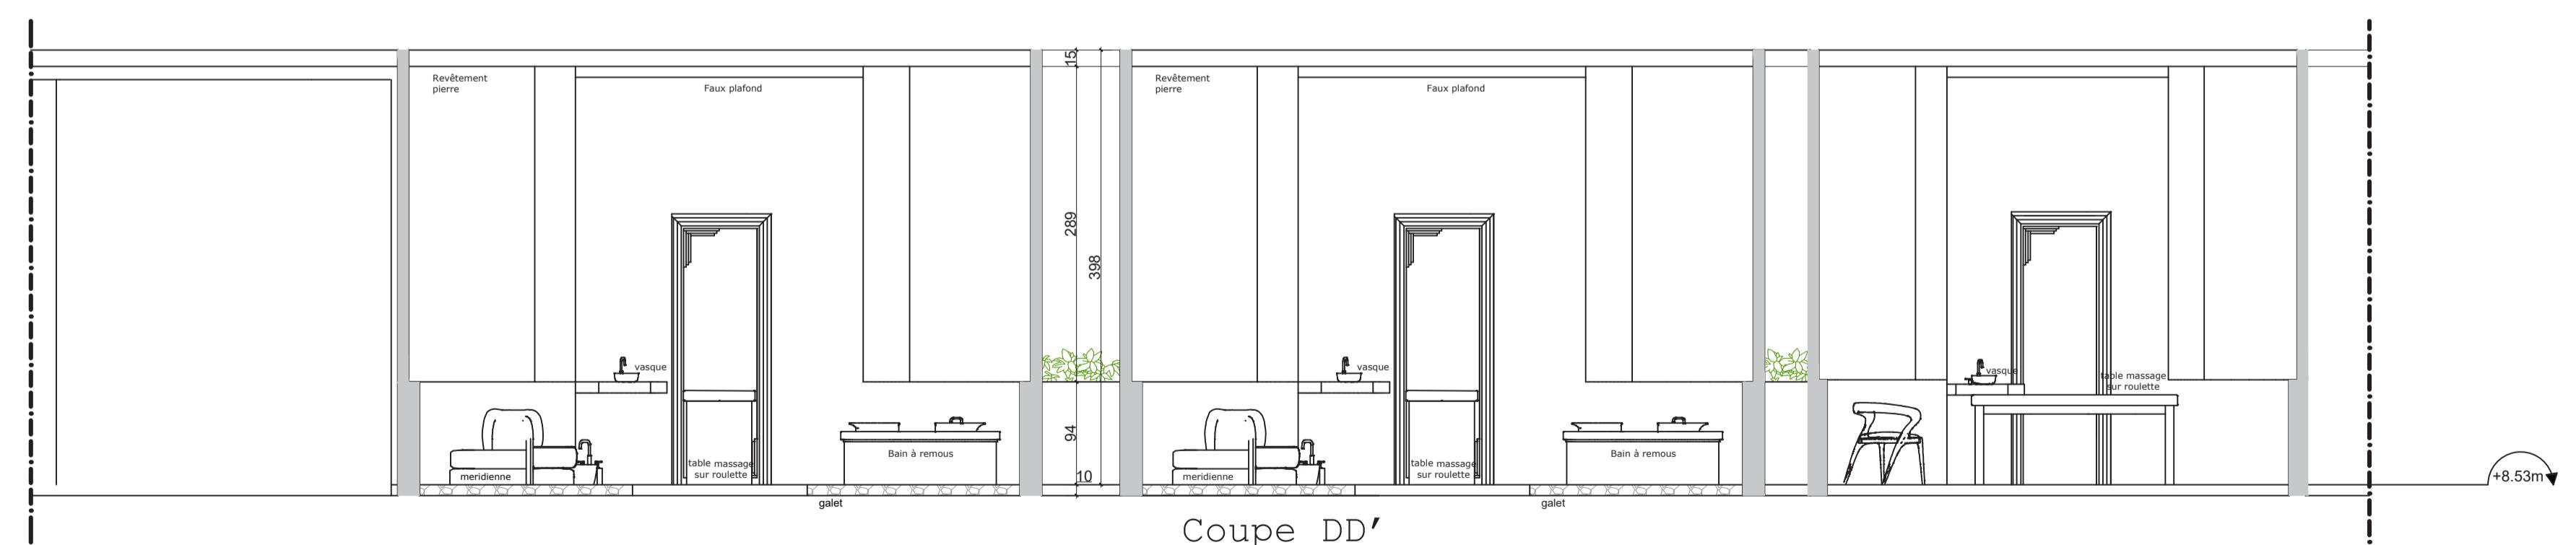


Coupe DD'

PLAN SOL
REZ -DE-CHAUSSÉE

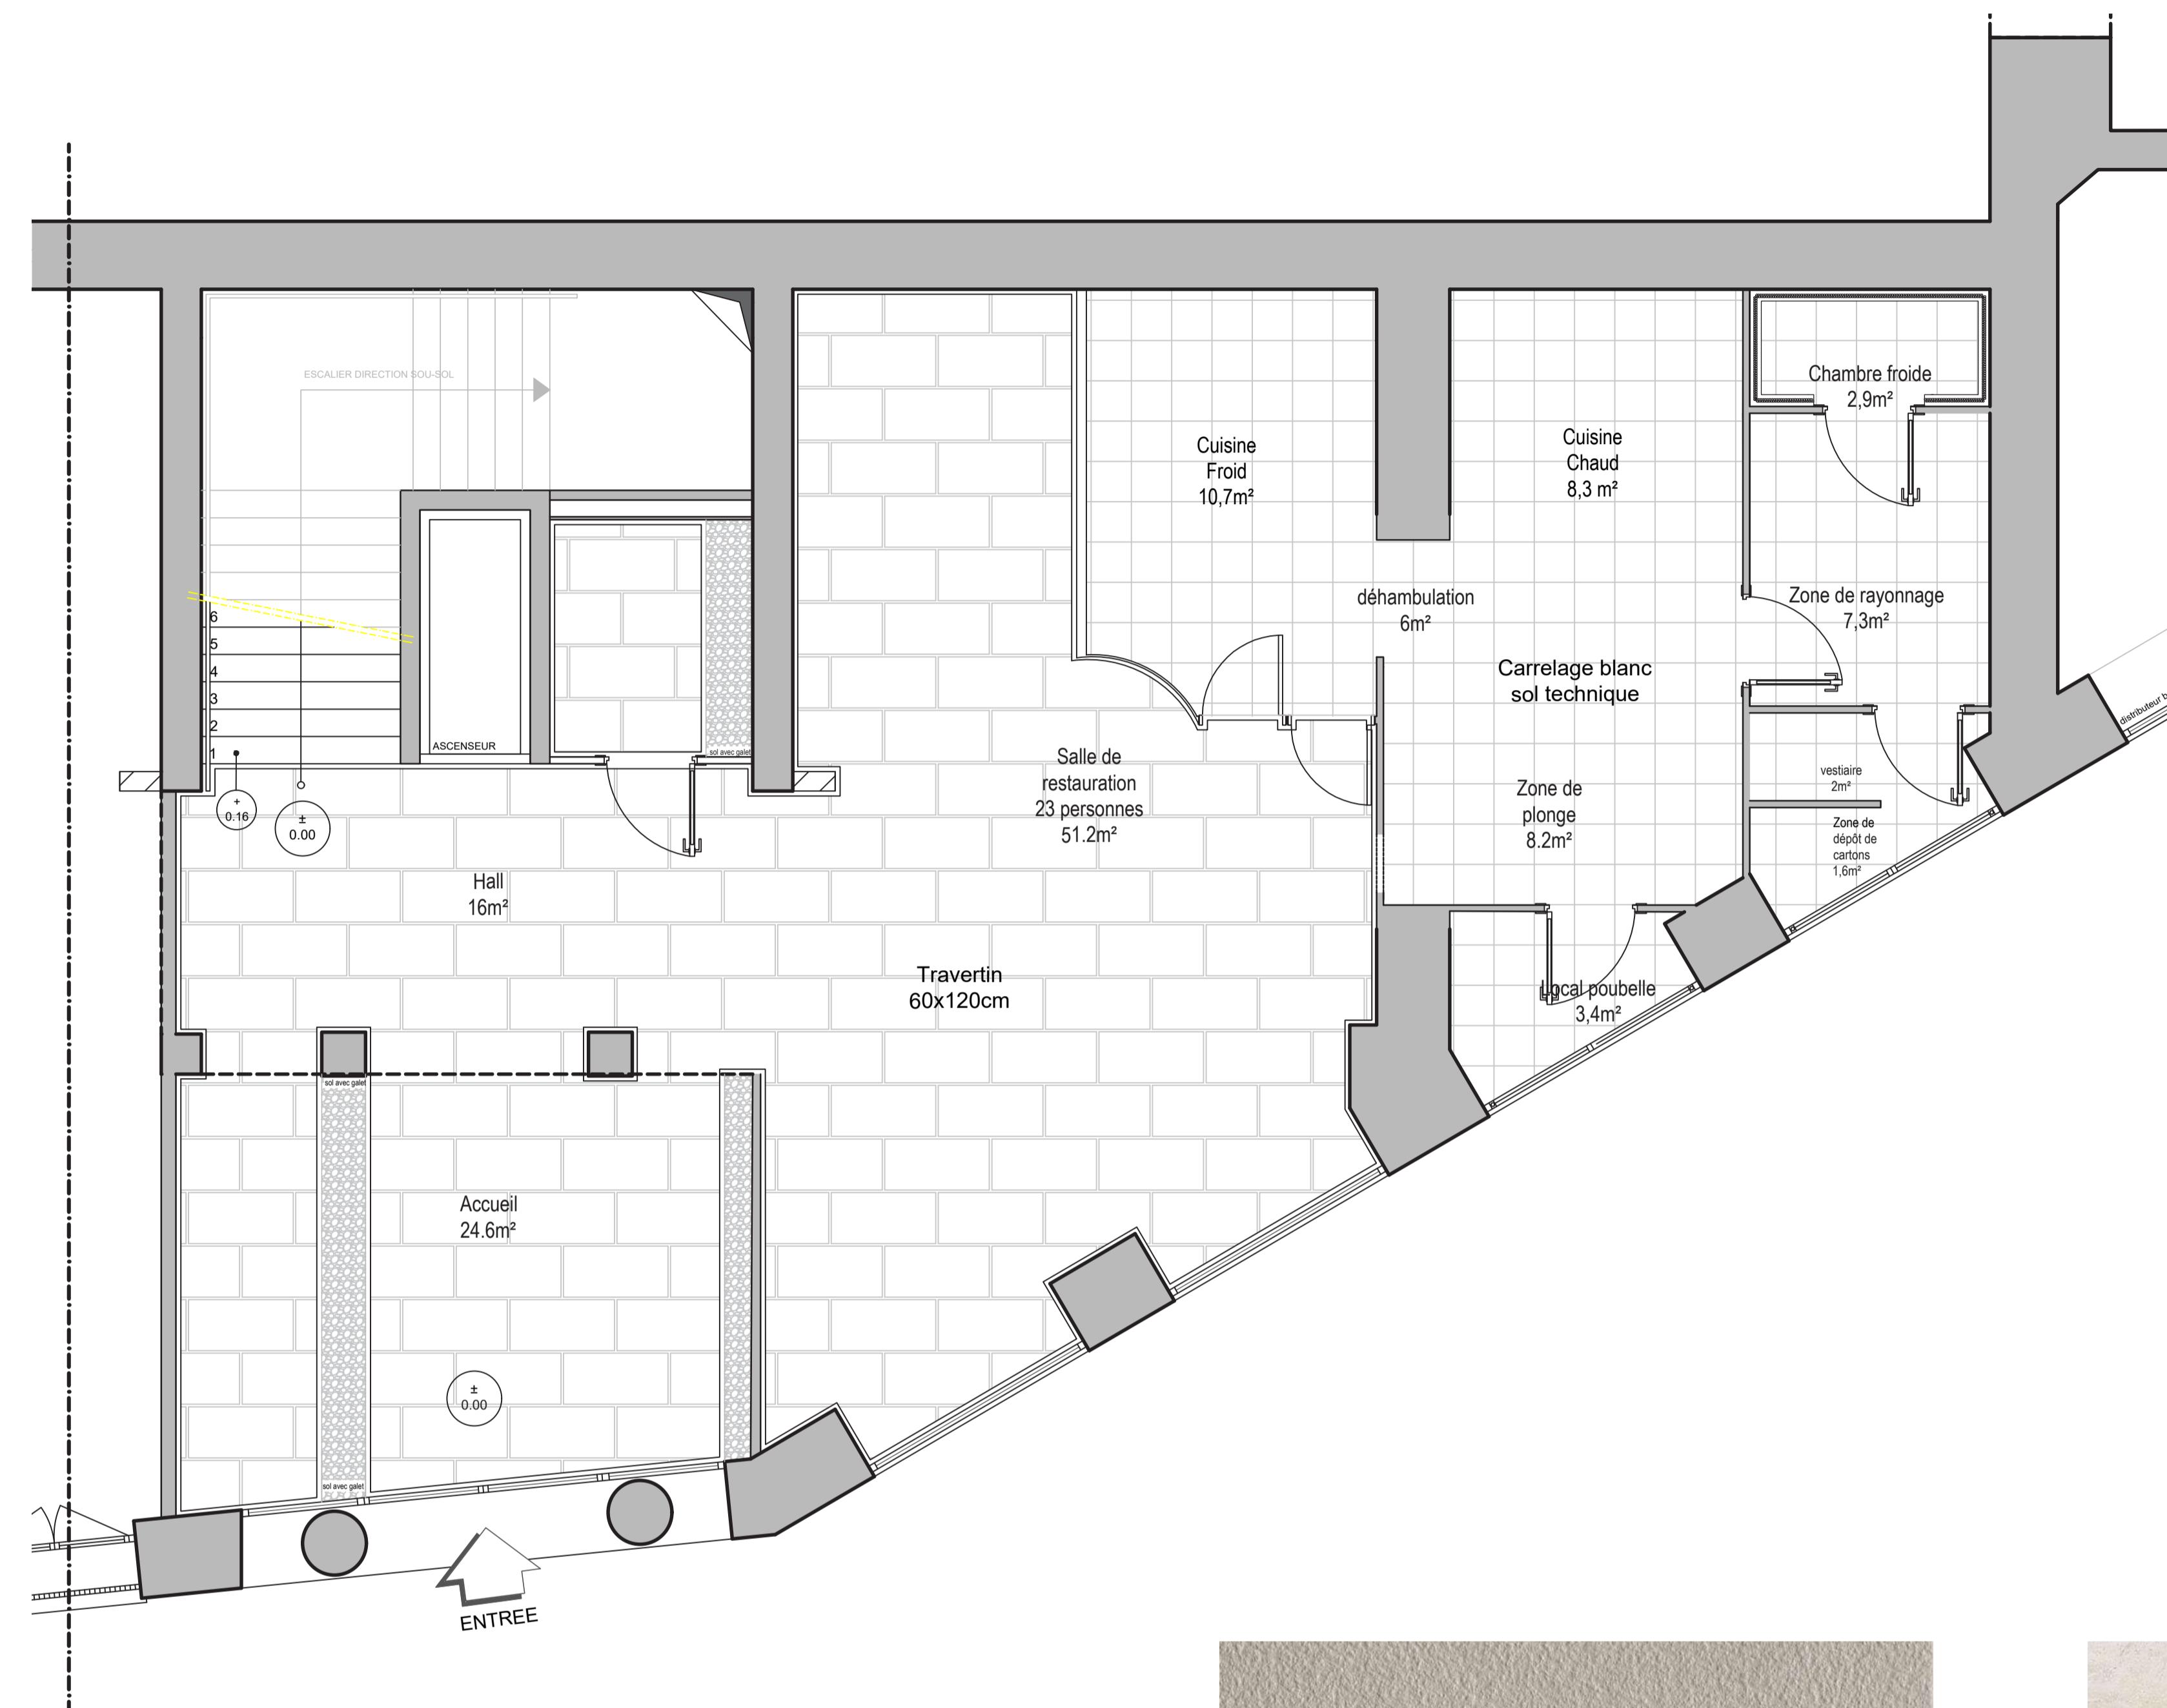


Carrelage 45x45 Shades
Gris Cuisine Profes-
sionnelle

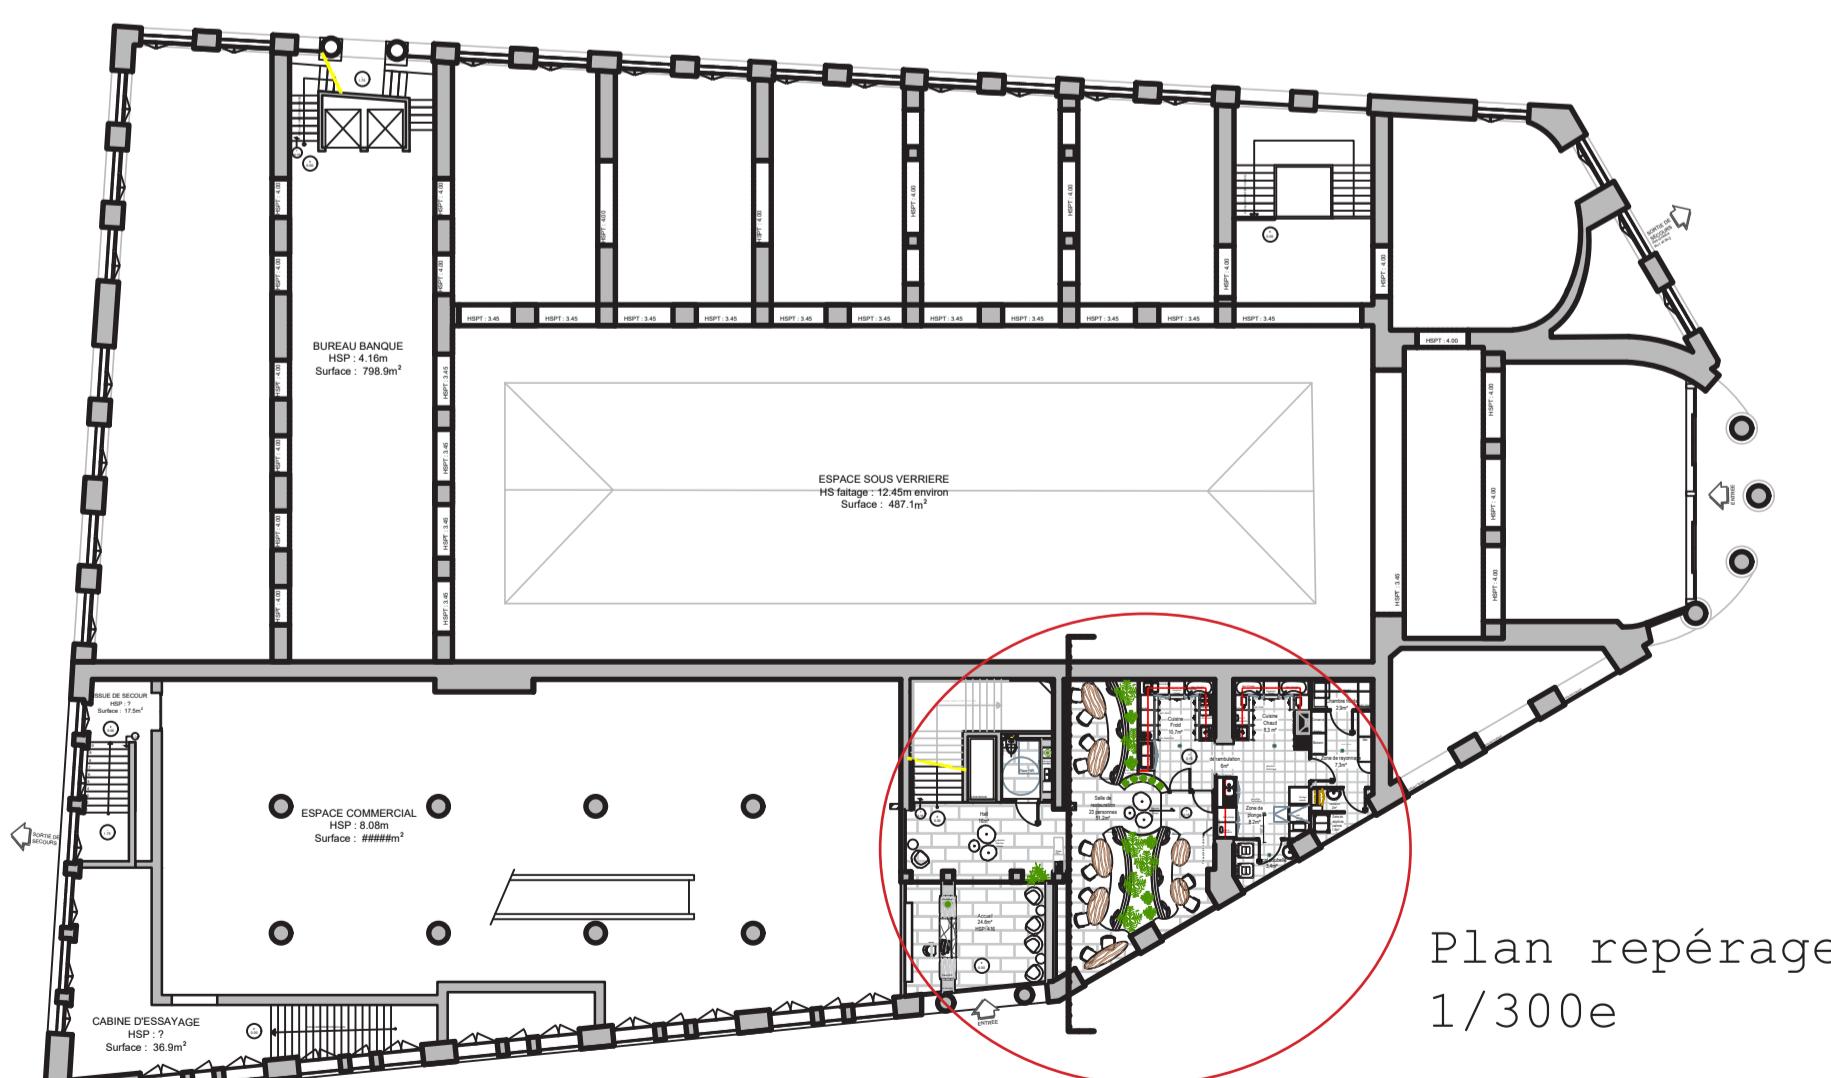

CUPASTONE PIERRES DIS-
TRIBUTION
Dallage sol traver-
tin - light mix - ref:
Pointp4190321

PLAN SOL
1ER ÉTAGE

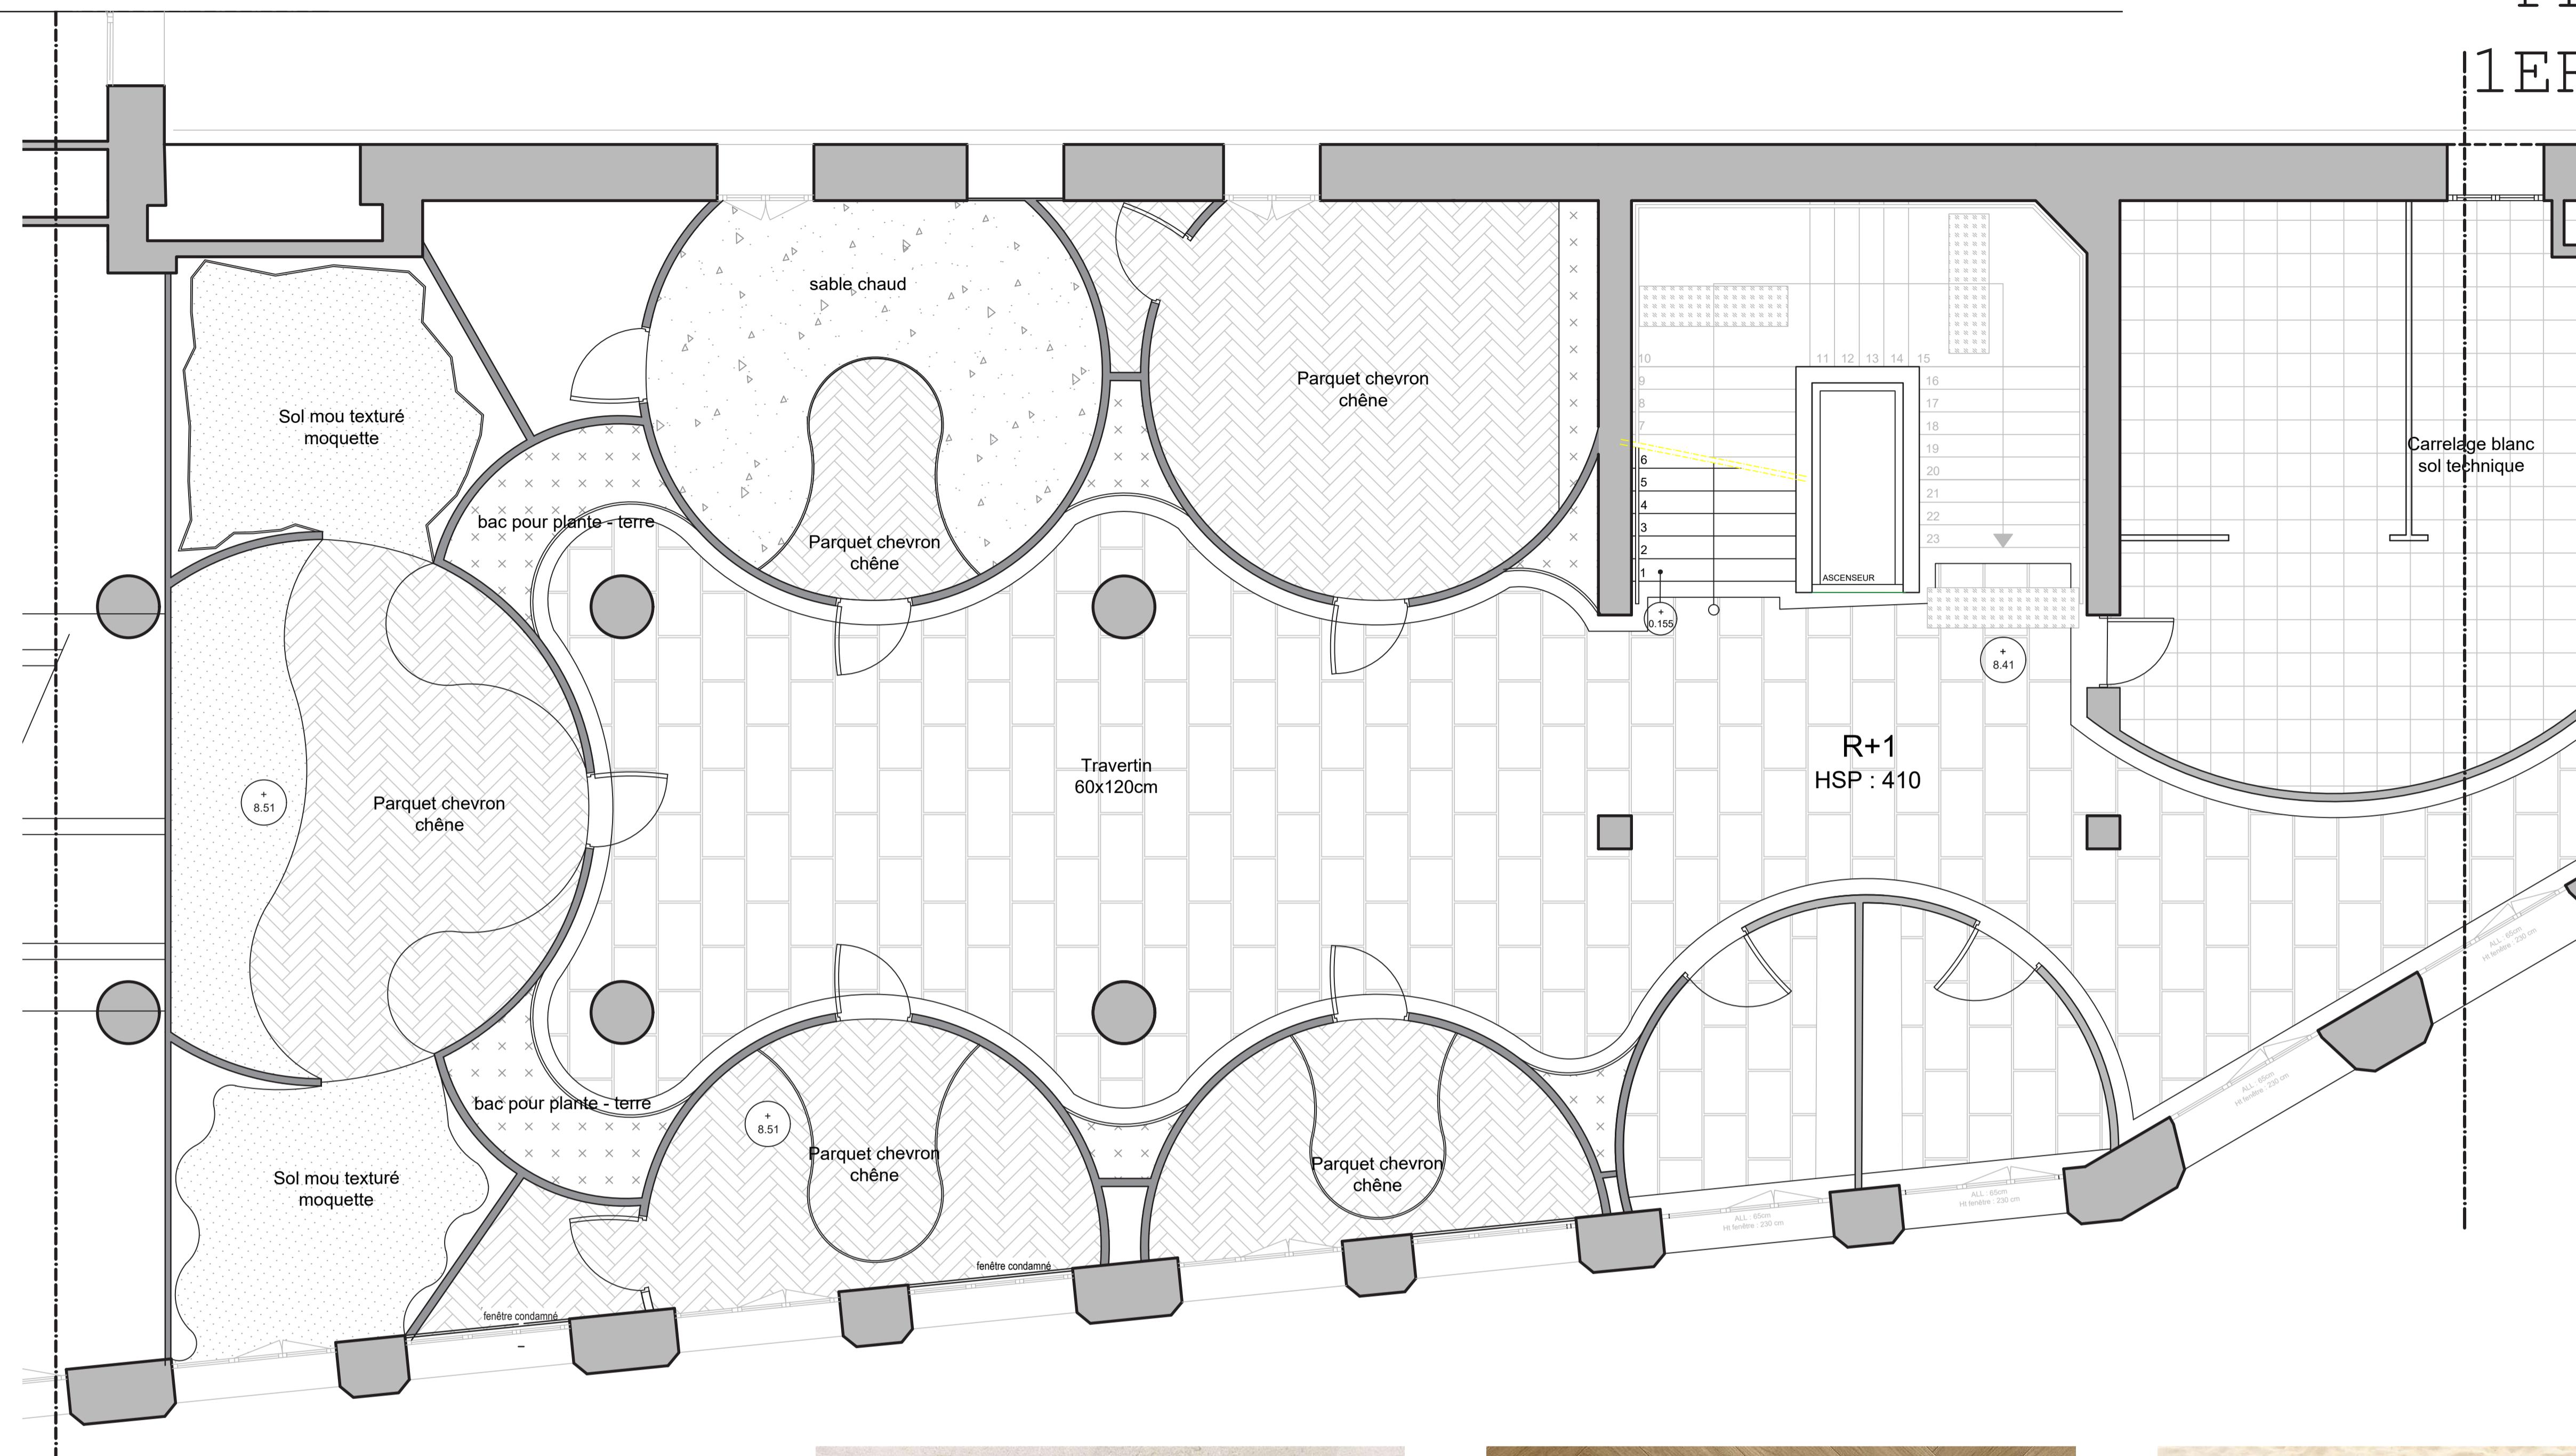


IV

V


VI

VII


VIII

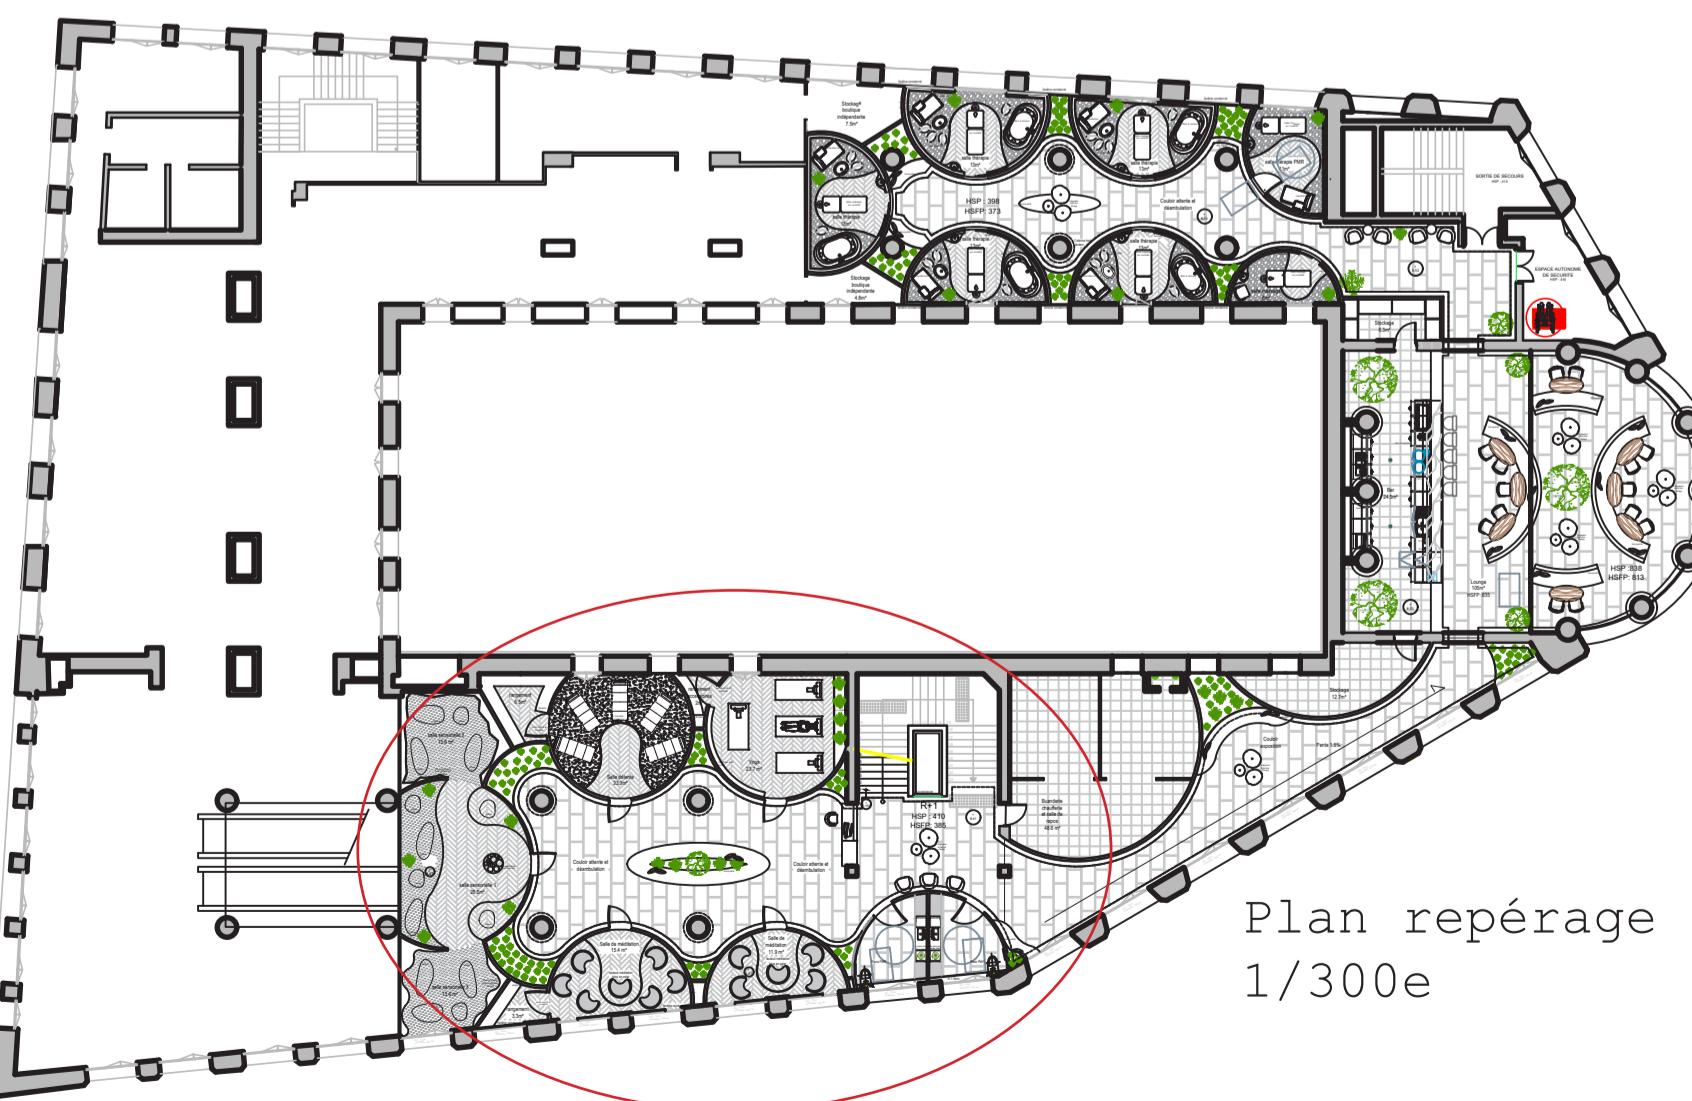

CUPASTONE PIERRES DIS-
TRIBUTION
Dallage sol traver-
tin - light mix - ref:
Pointp4190321

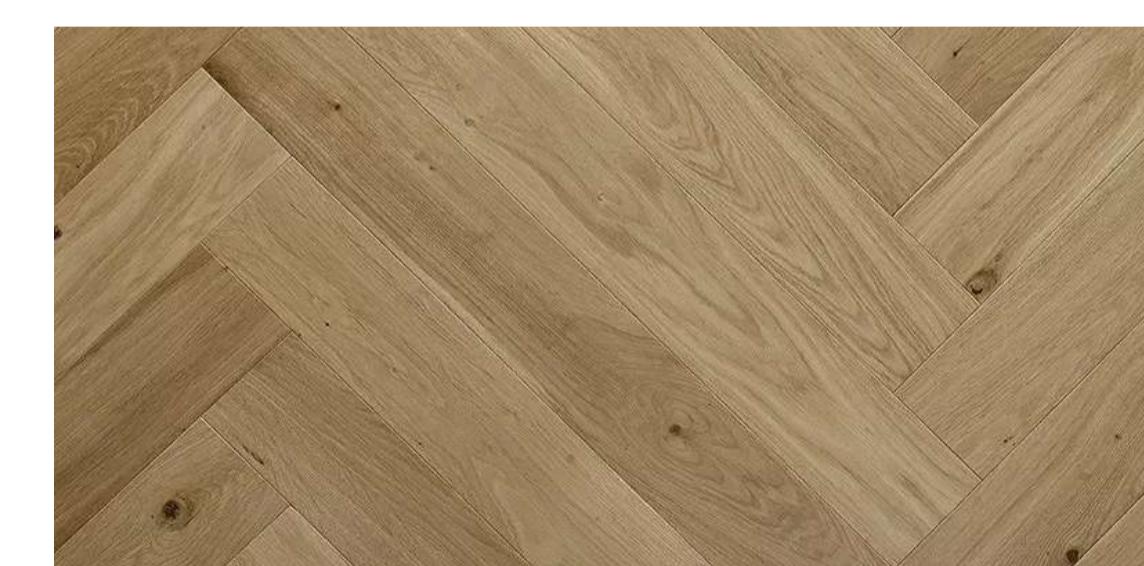


Bâton Rompu Chêne
Contrecollé Natural
Référence : 00502914108
Carré sol



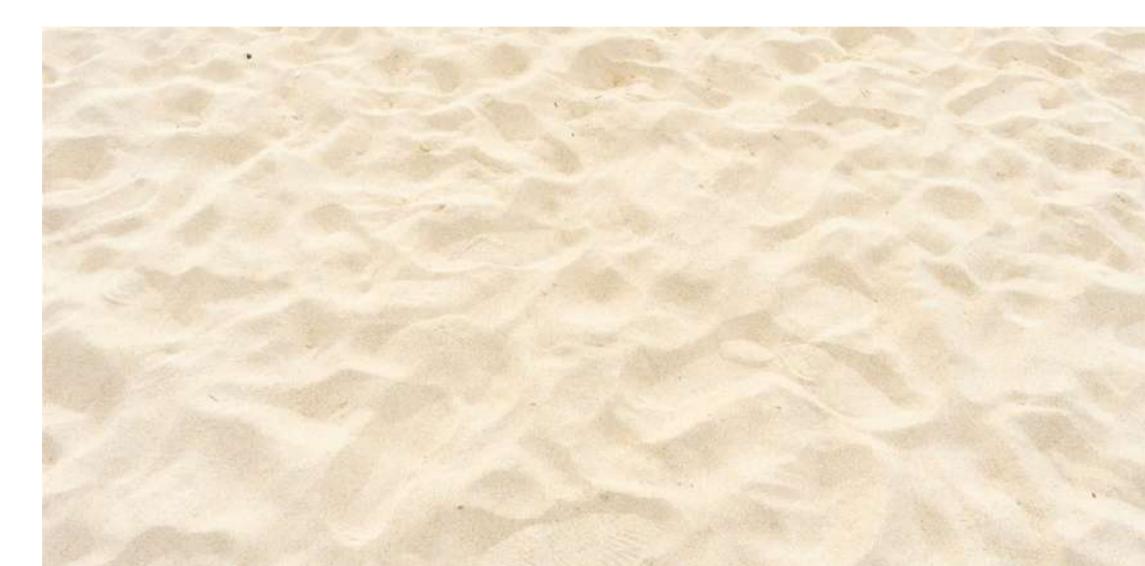


sol en sable jaune doux
et chaud


PLAN SOL
1ER ÉTAGE

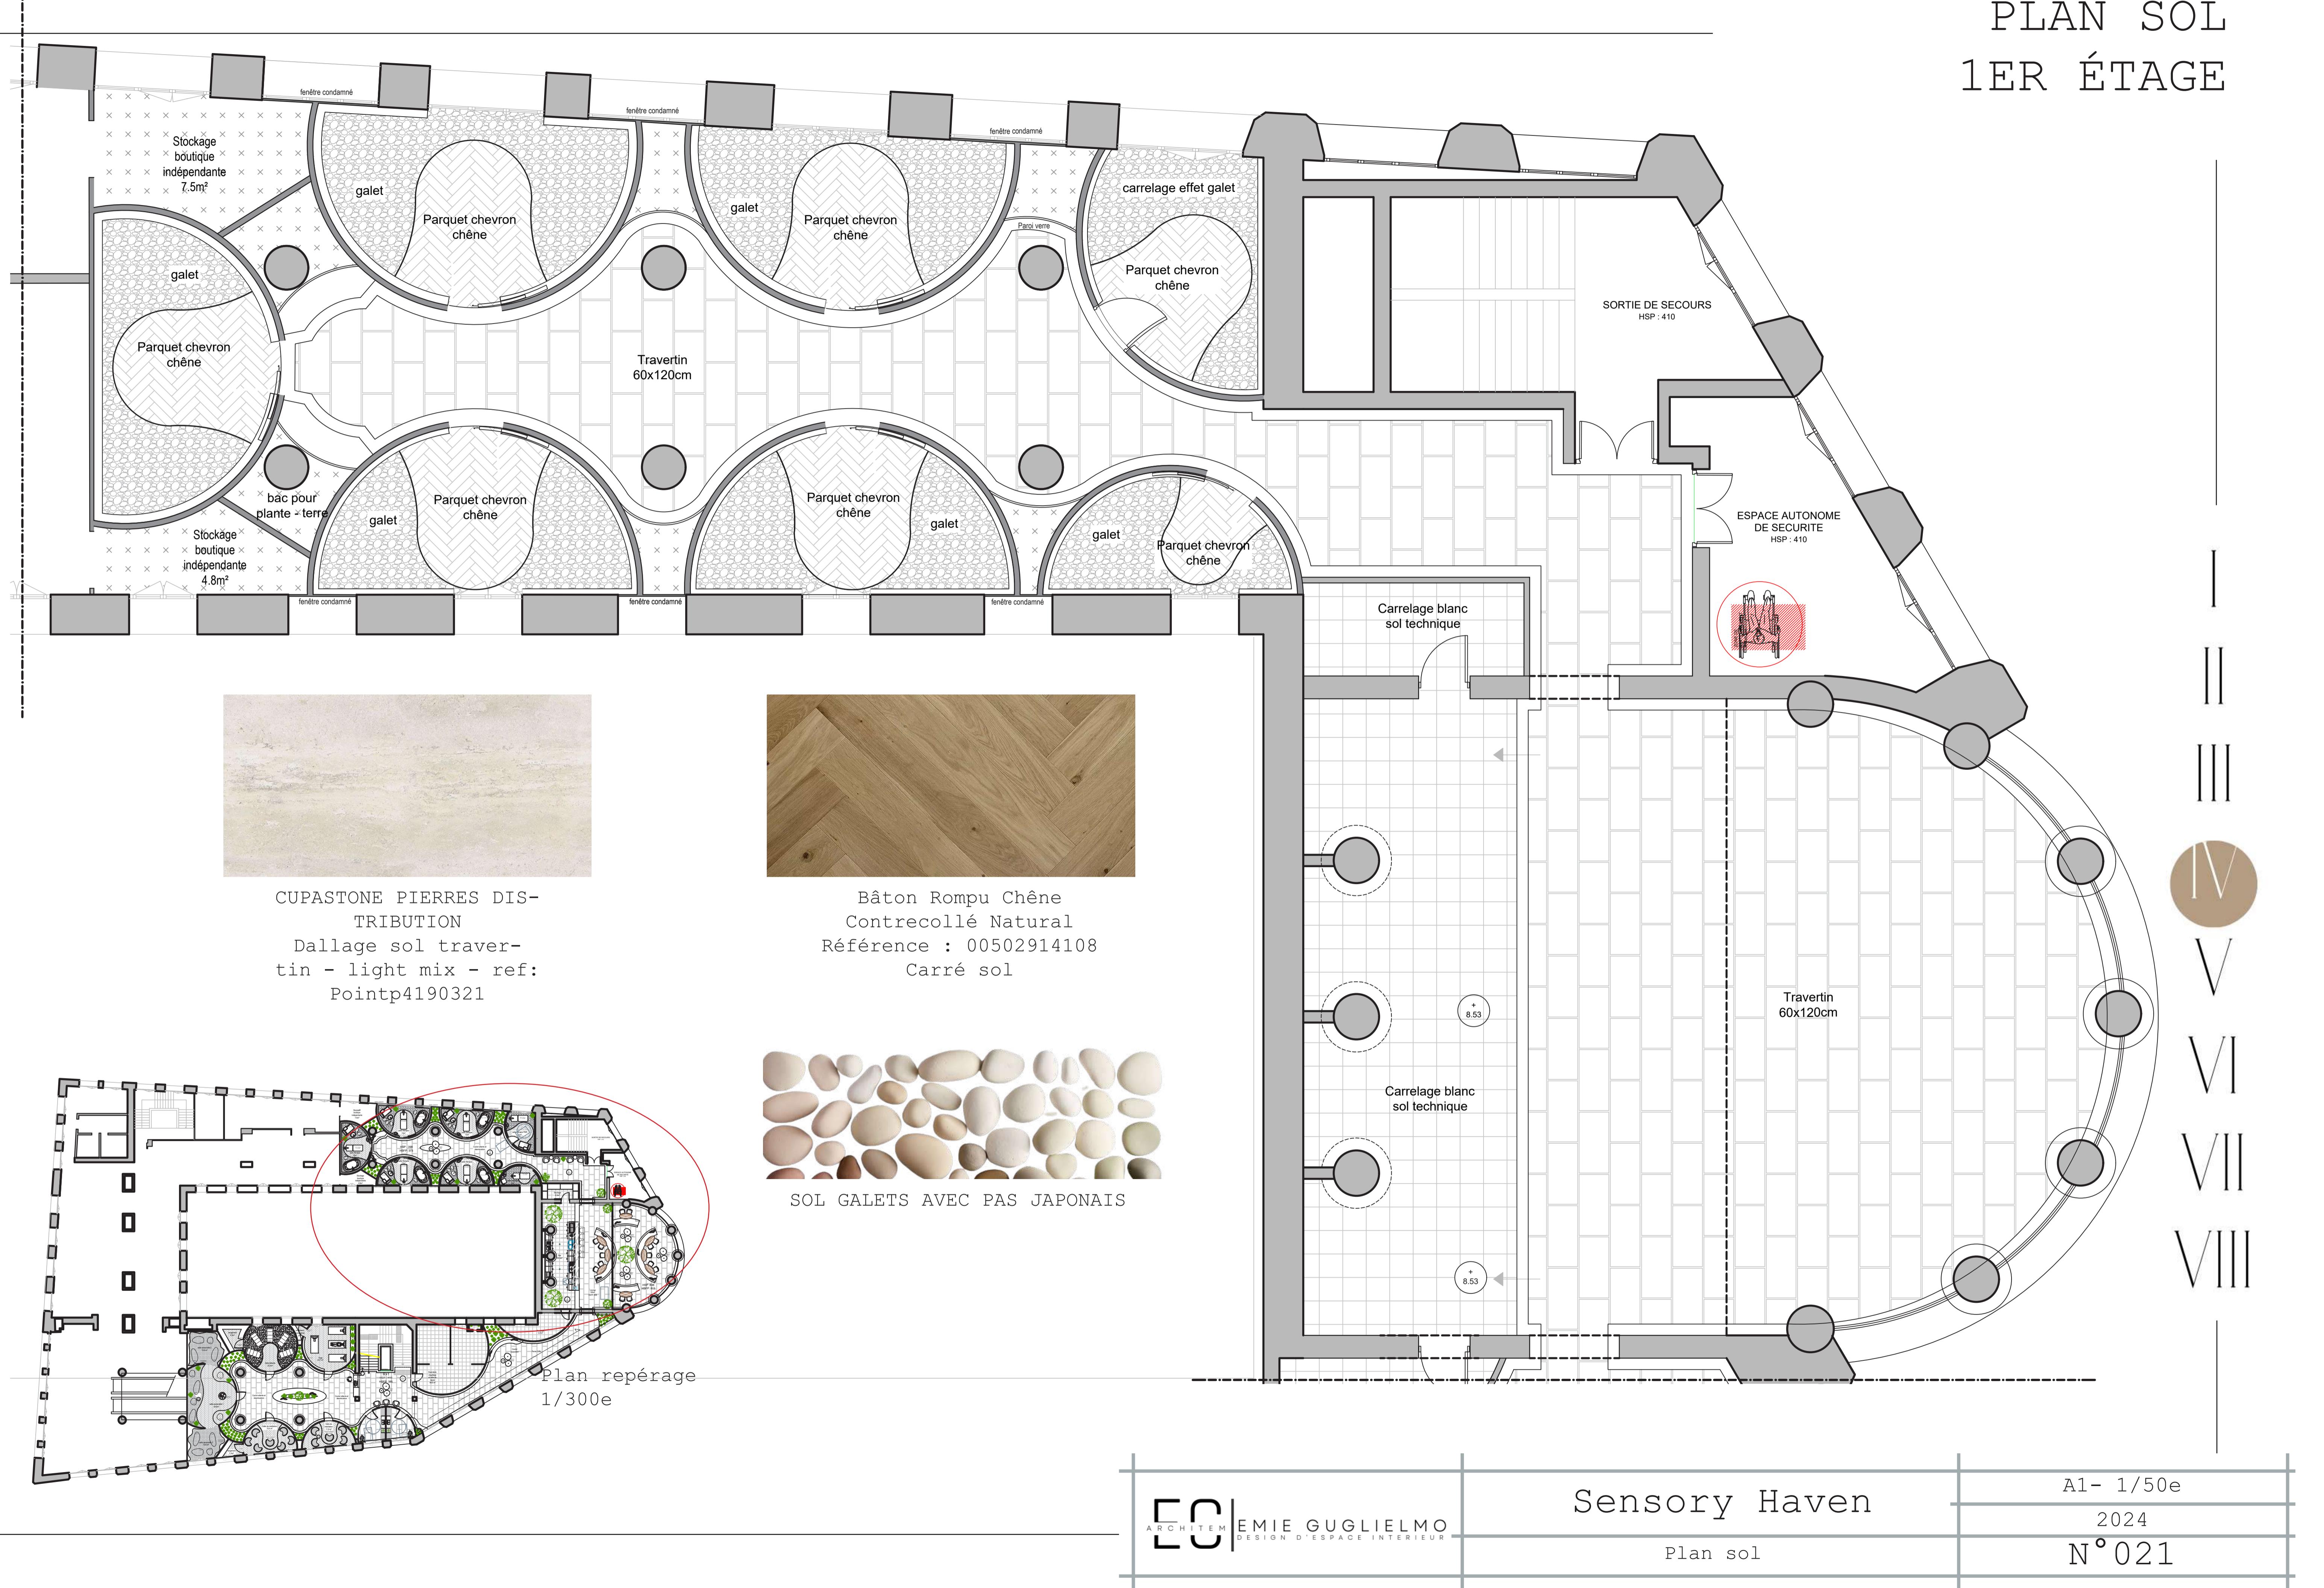

PLAN PLAFOND REZ - DE - CHAUSSEE

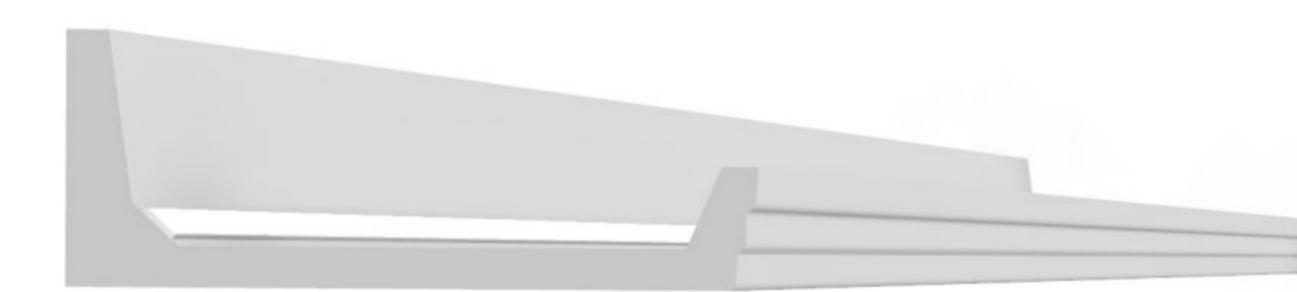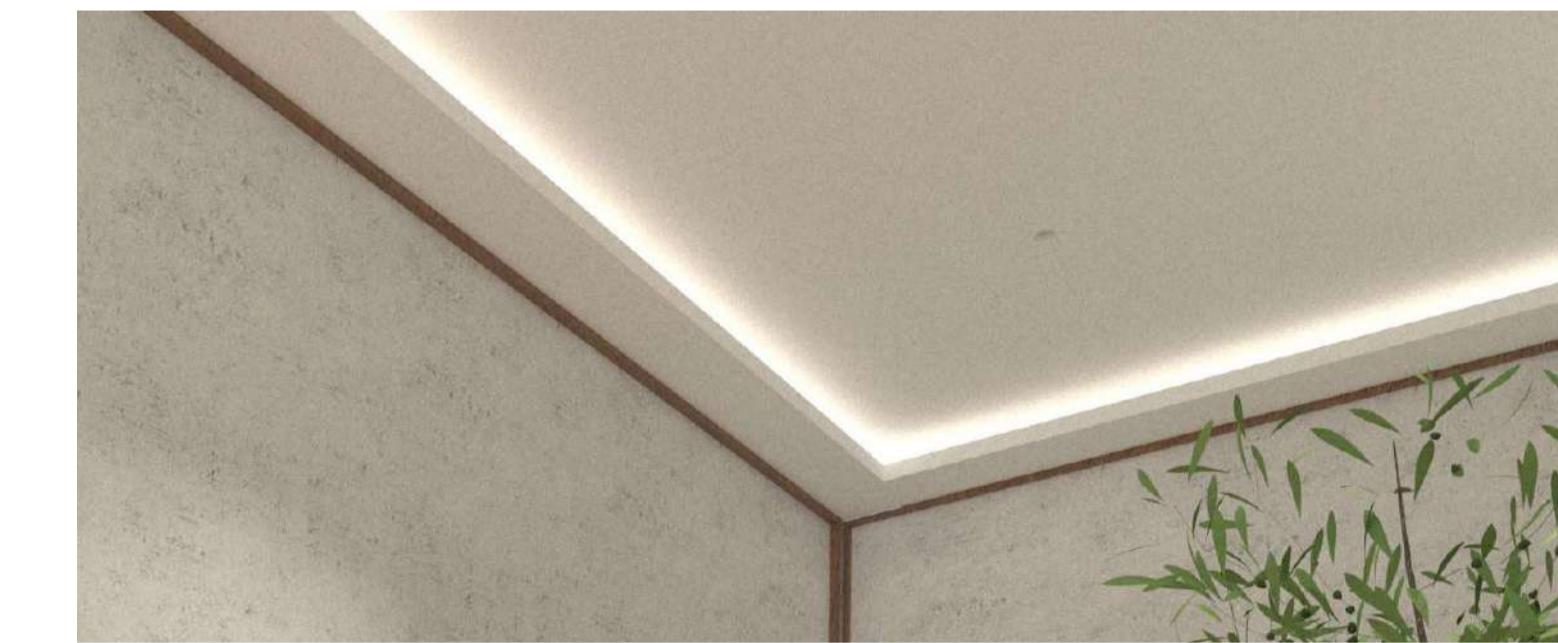
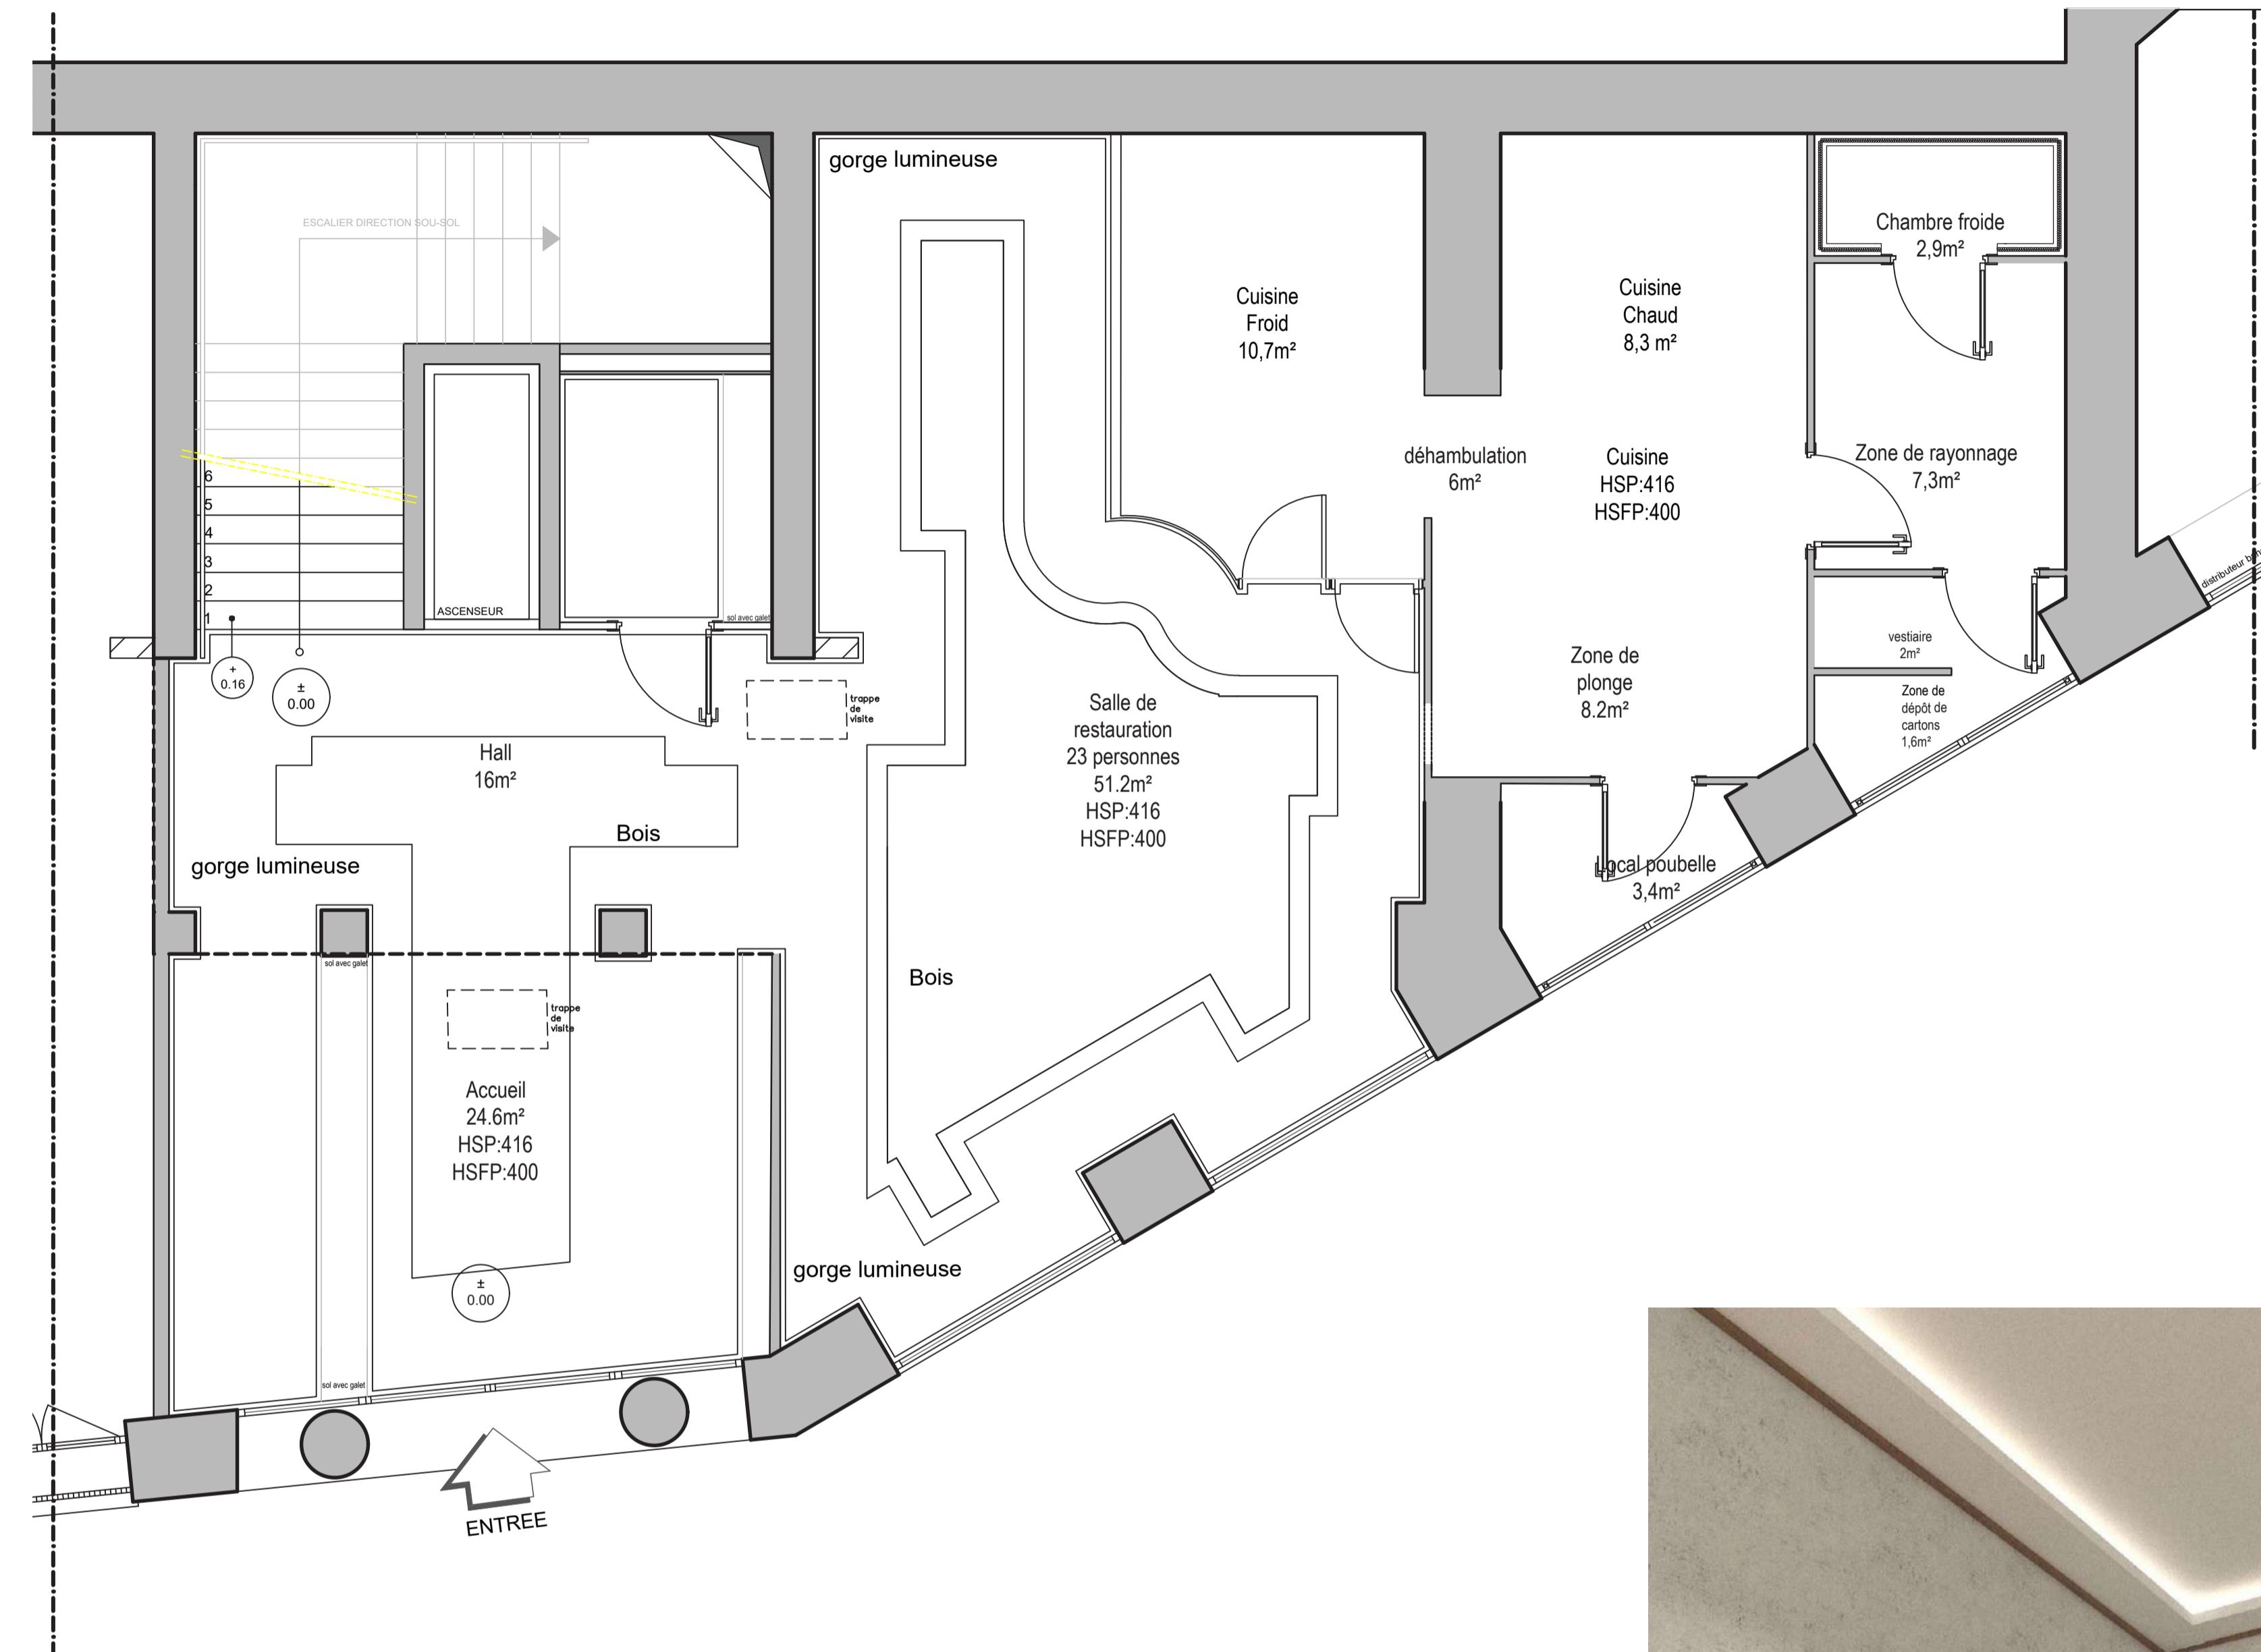


CORNICHE À ÉCLAIRAGE INDIRECT - STAFF DÉCOR - D104

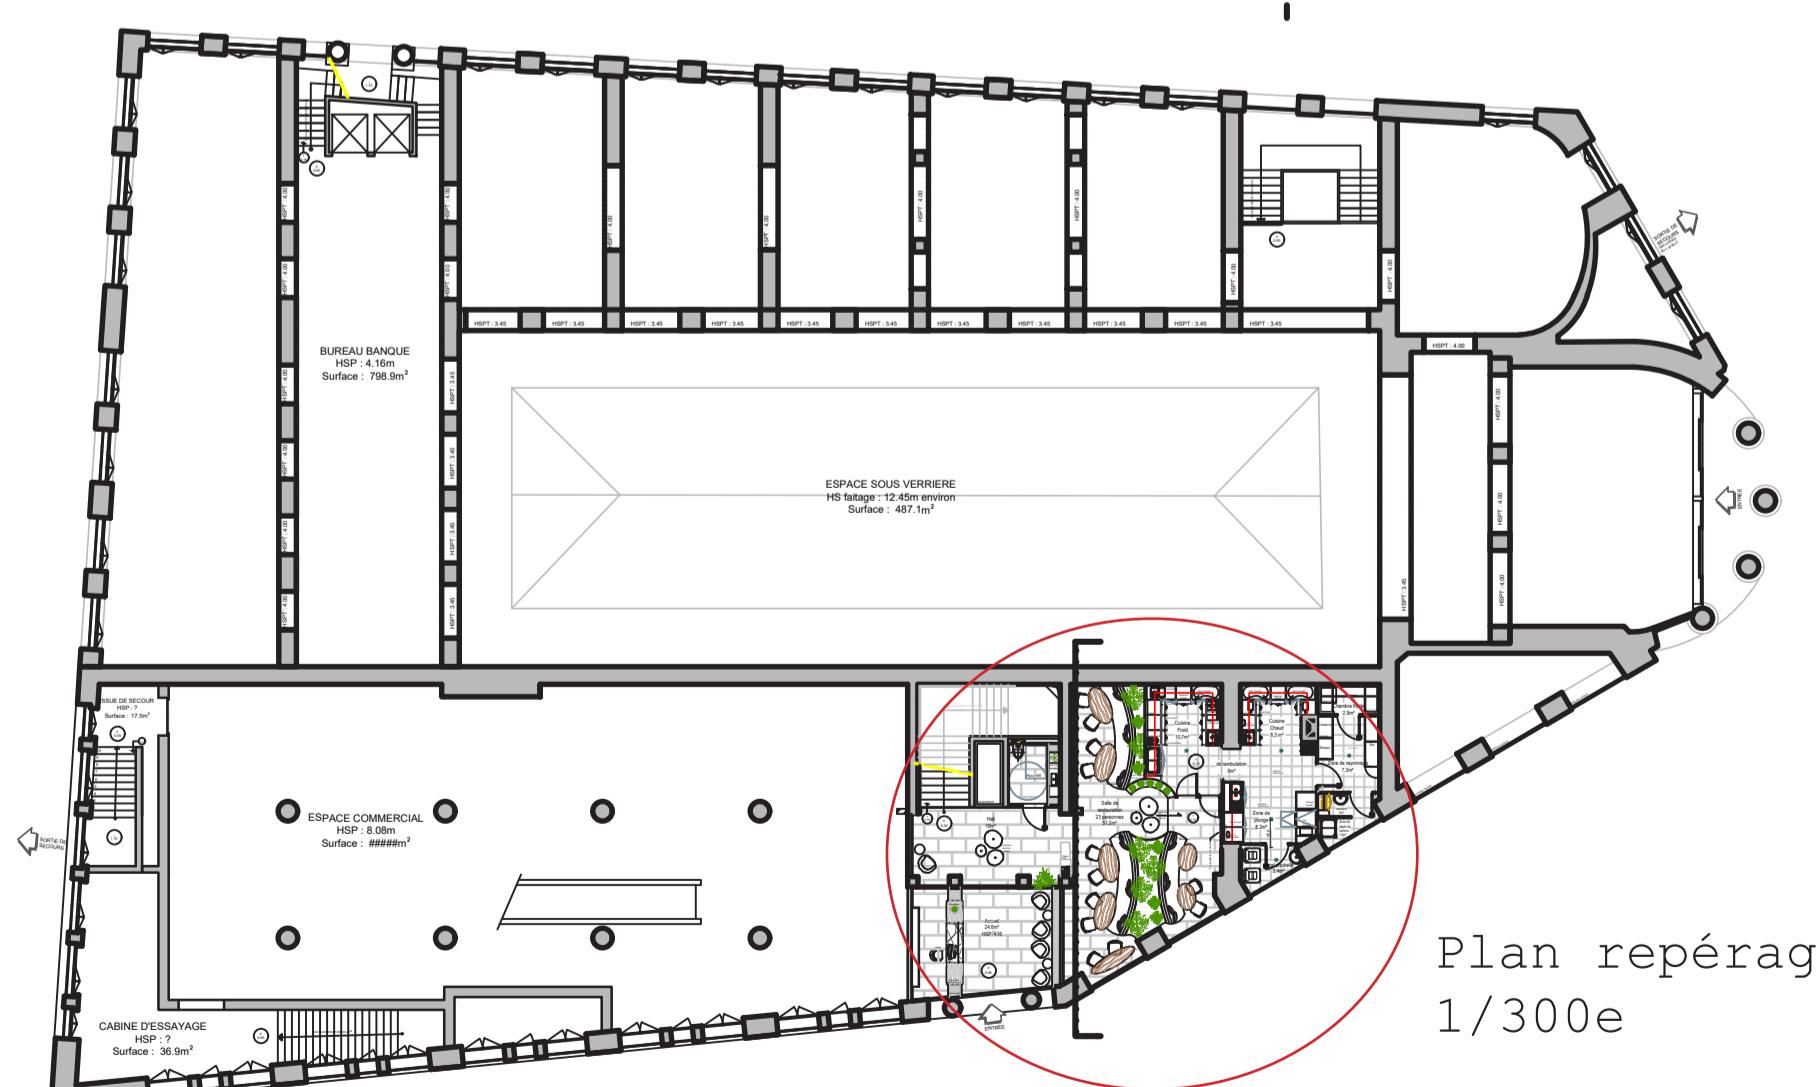

Plan repérage
1/300e


PLAN PLAFOND
1ER ÉTAGE

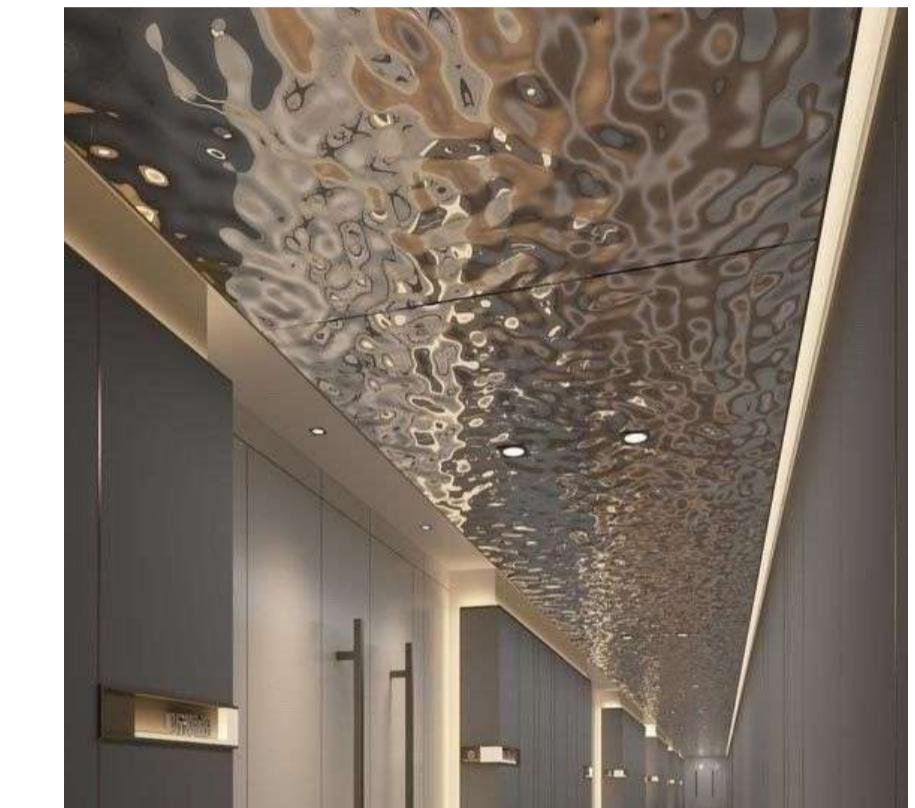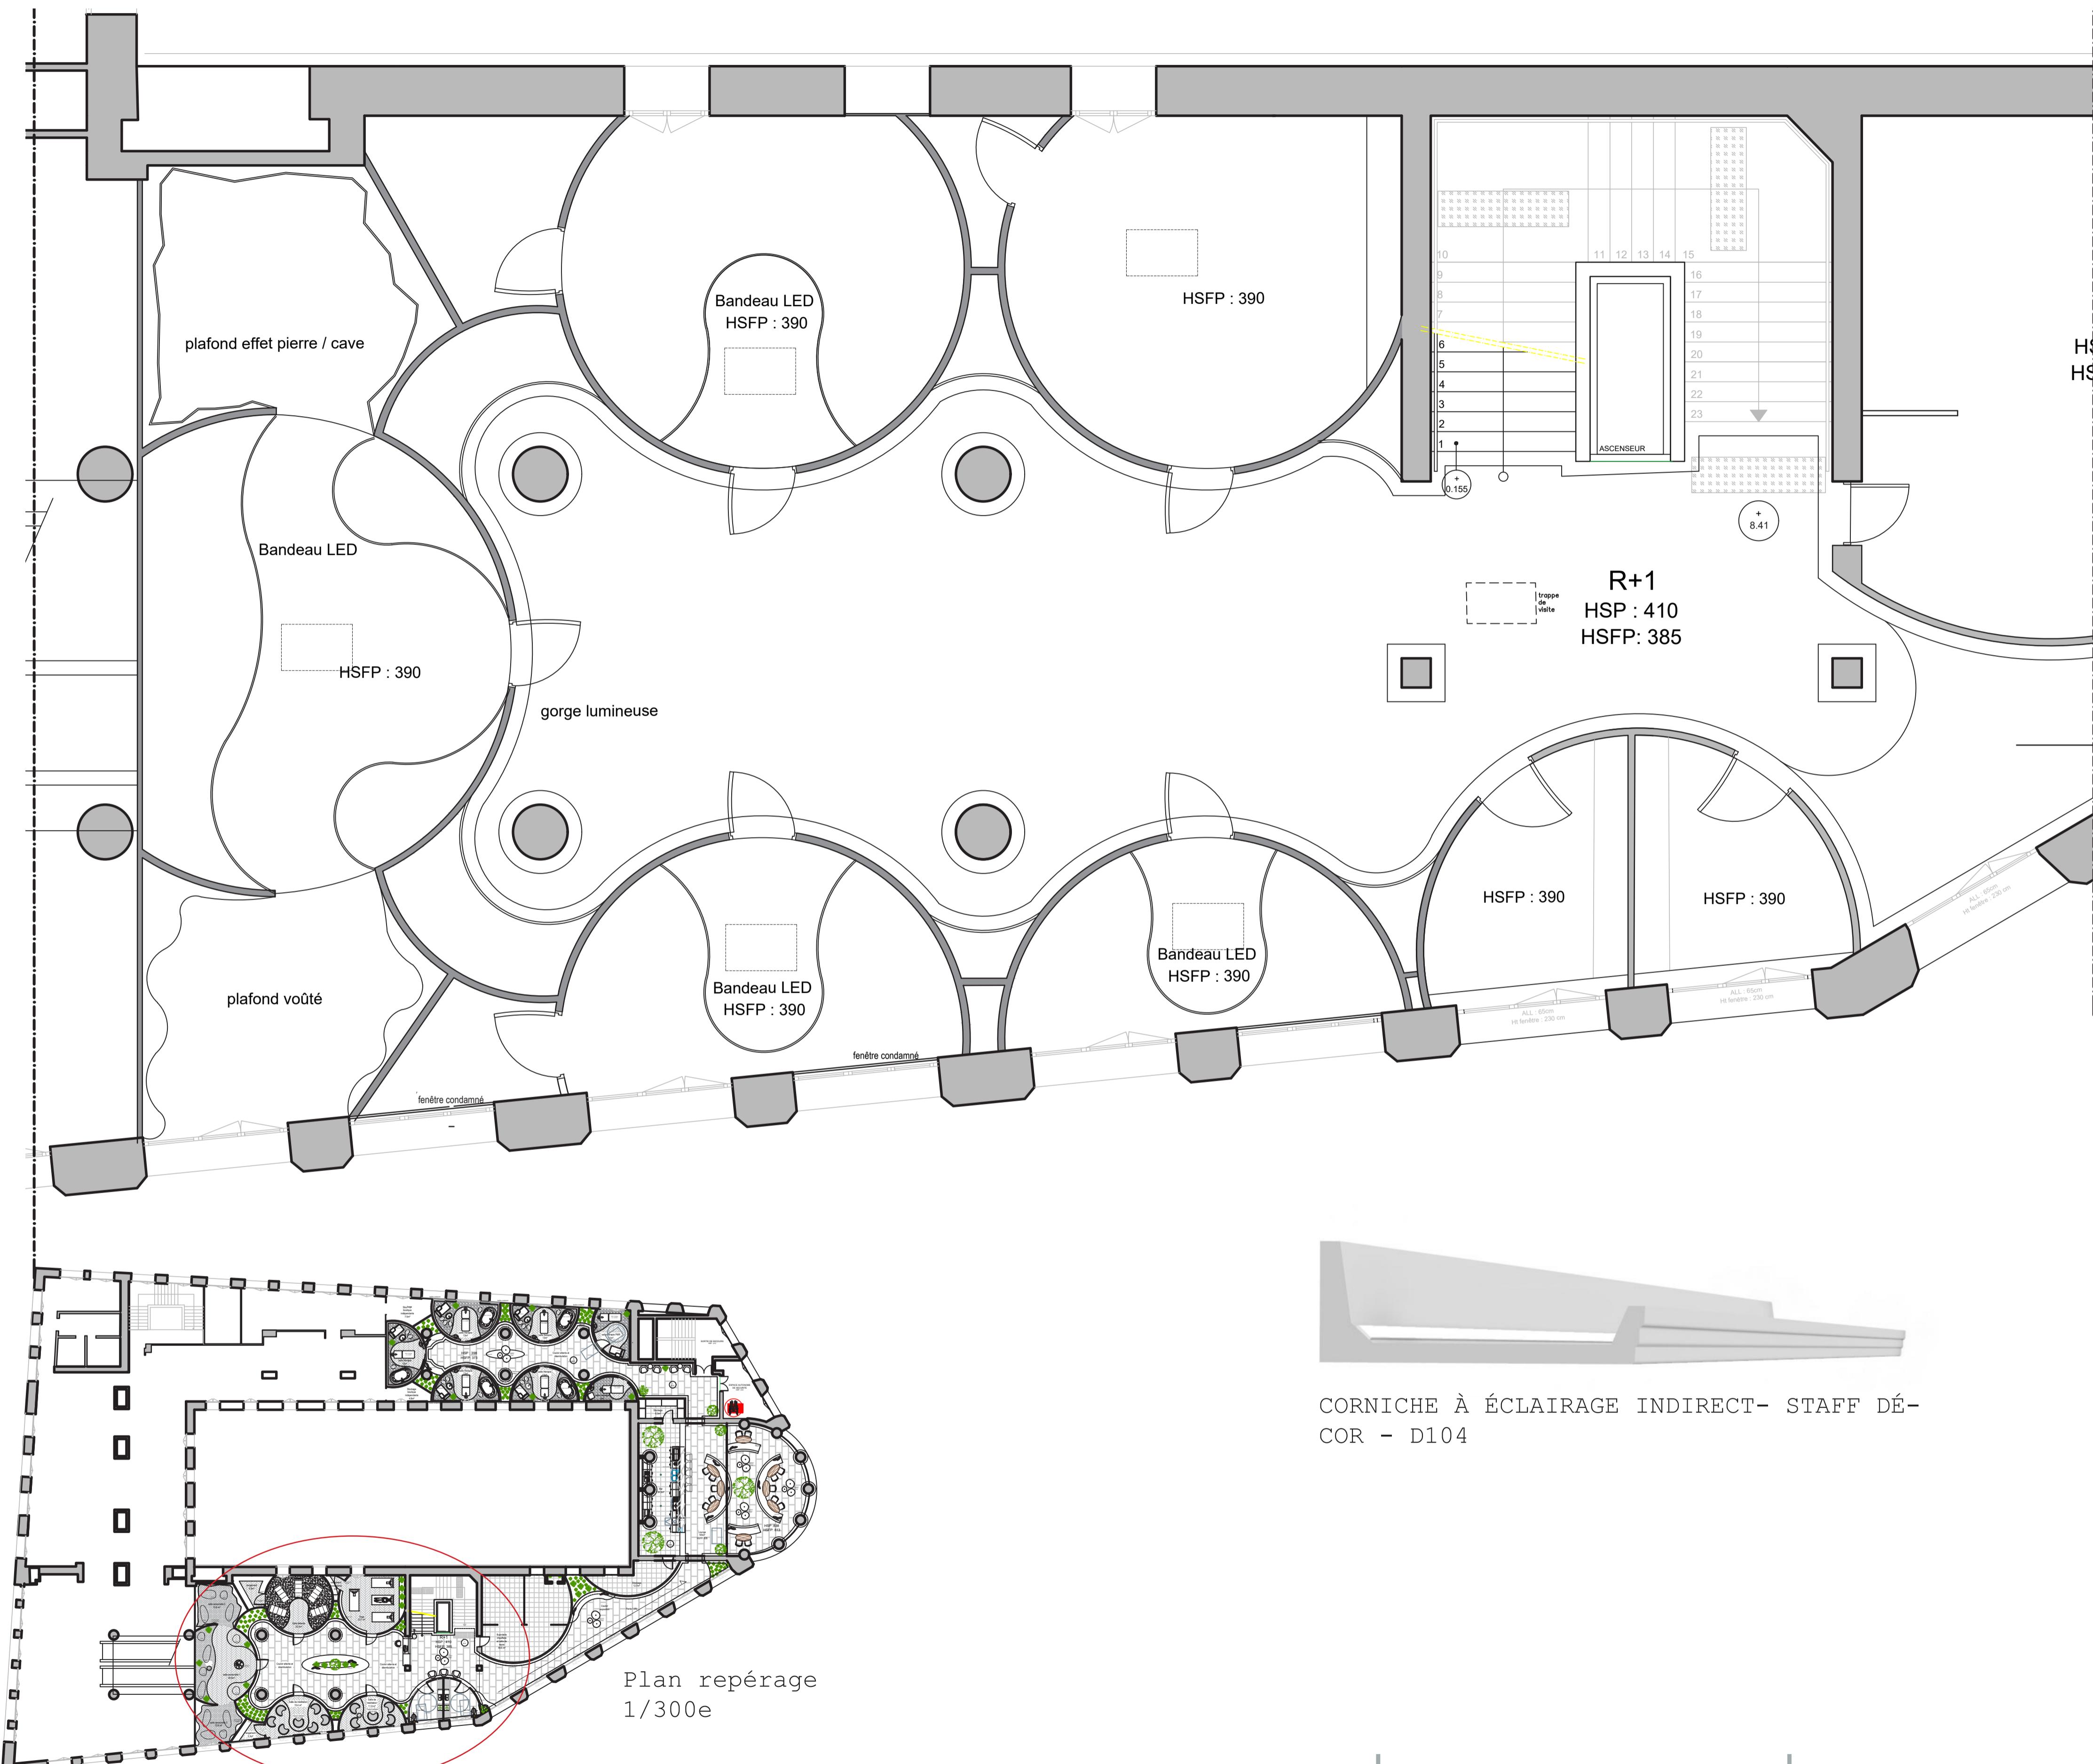

FEUILLE D'ONDULATION DE L'EAU EN ACIER INOXYDABLE AVEC EFFET DÉCORATIF BRILLANT ARGGER




CORNICHE À ÉCLAIRAGE INDIRECT- STAFF DÉCOR - D104


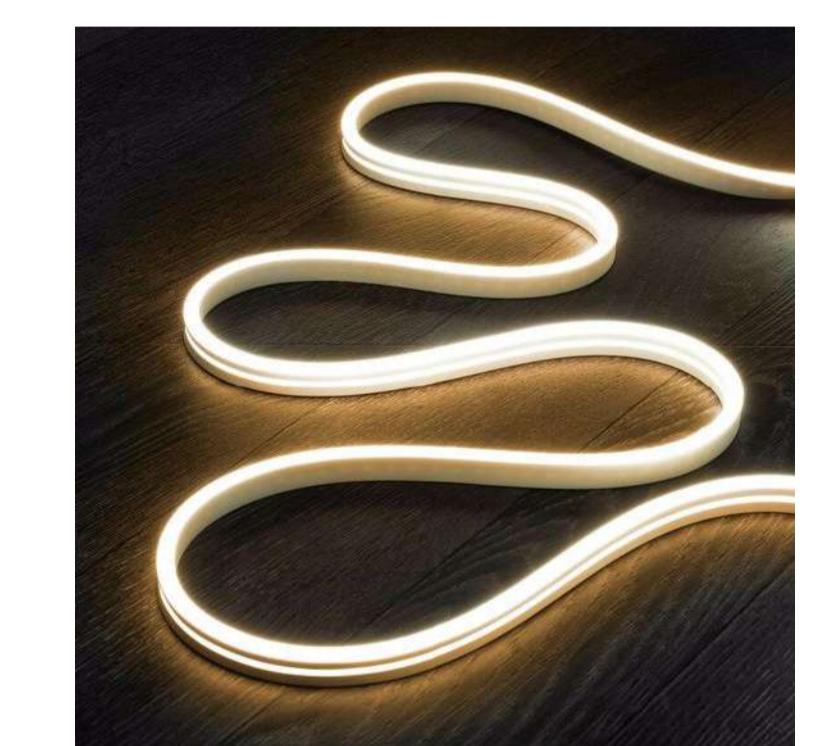


NÉON LED FLEXIBLE BLANC CHAUD



PLAN PLAFOND
1ER ÉTAGE

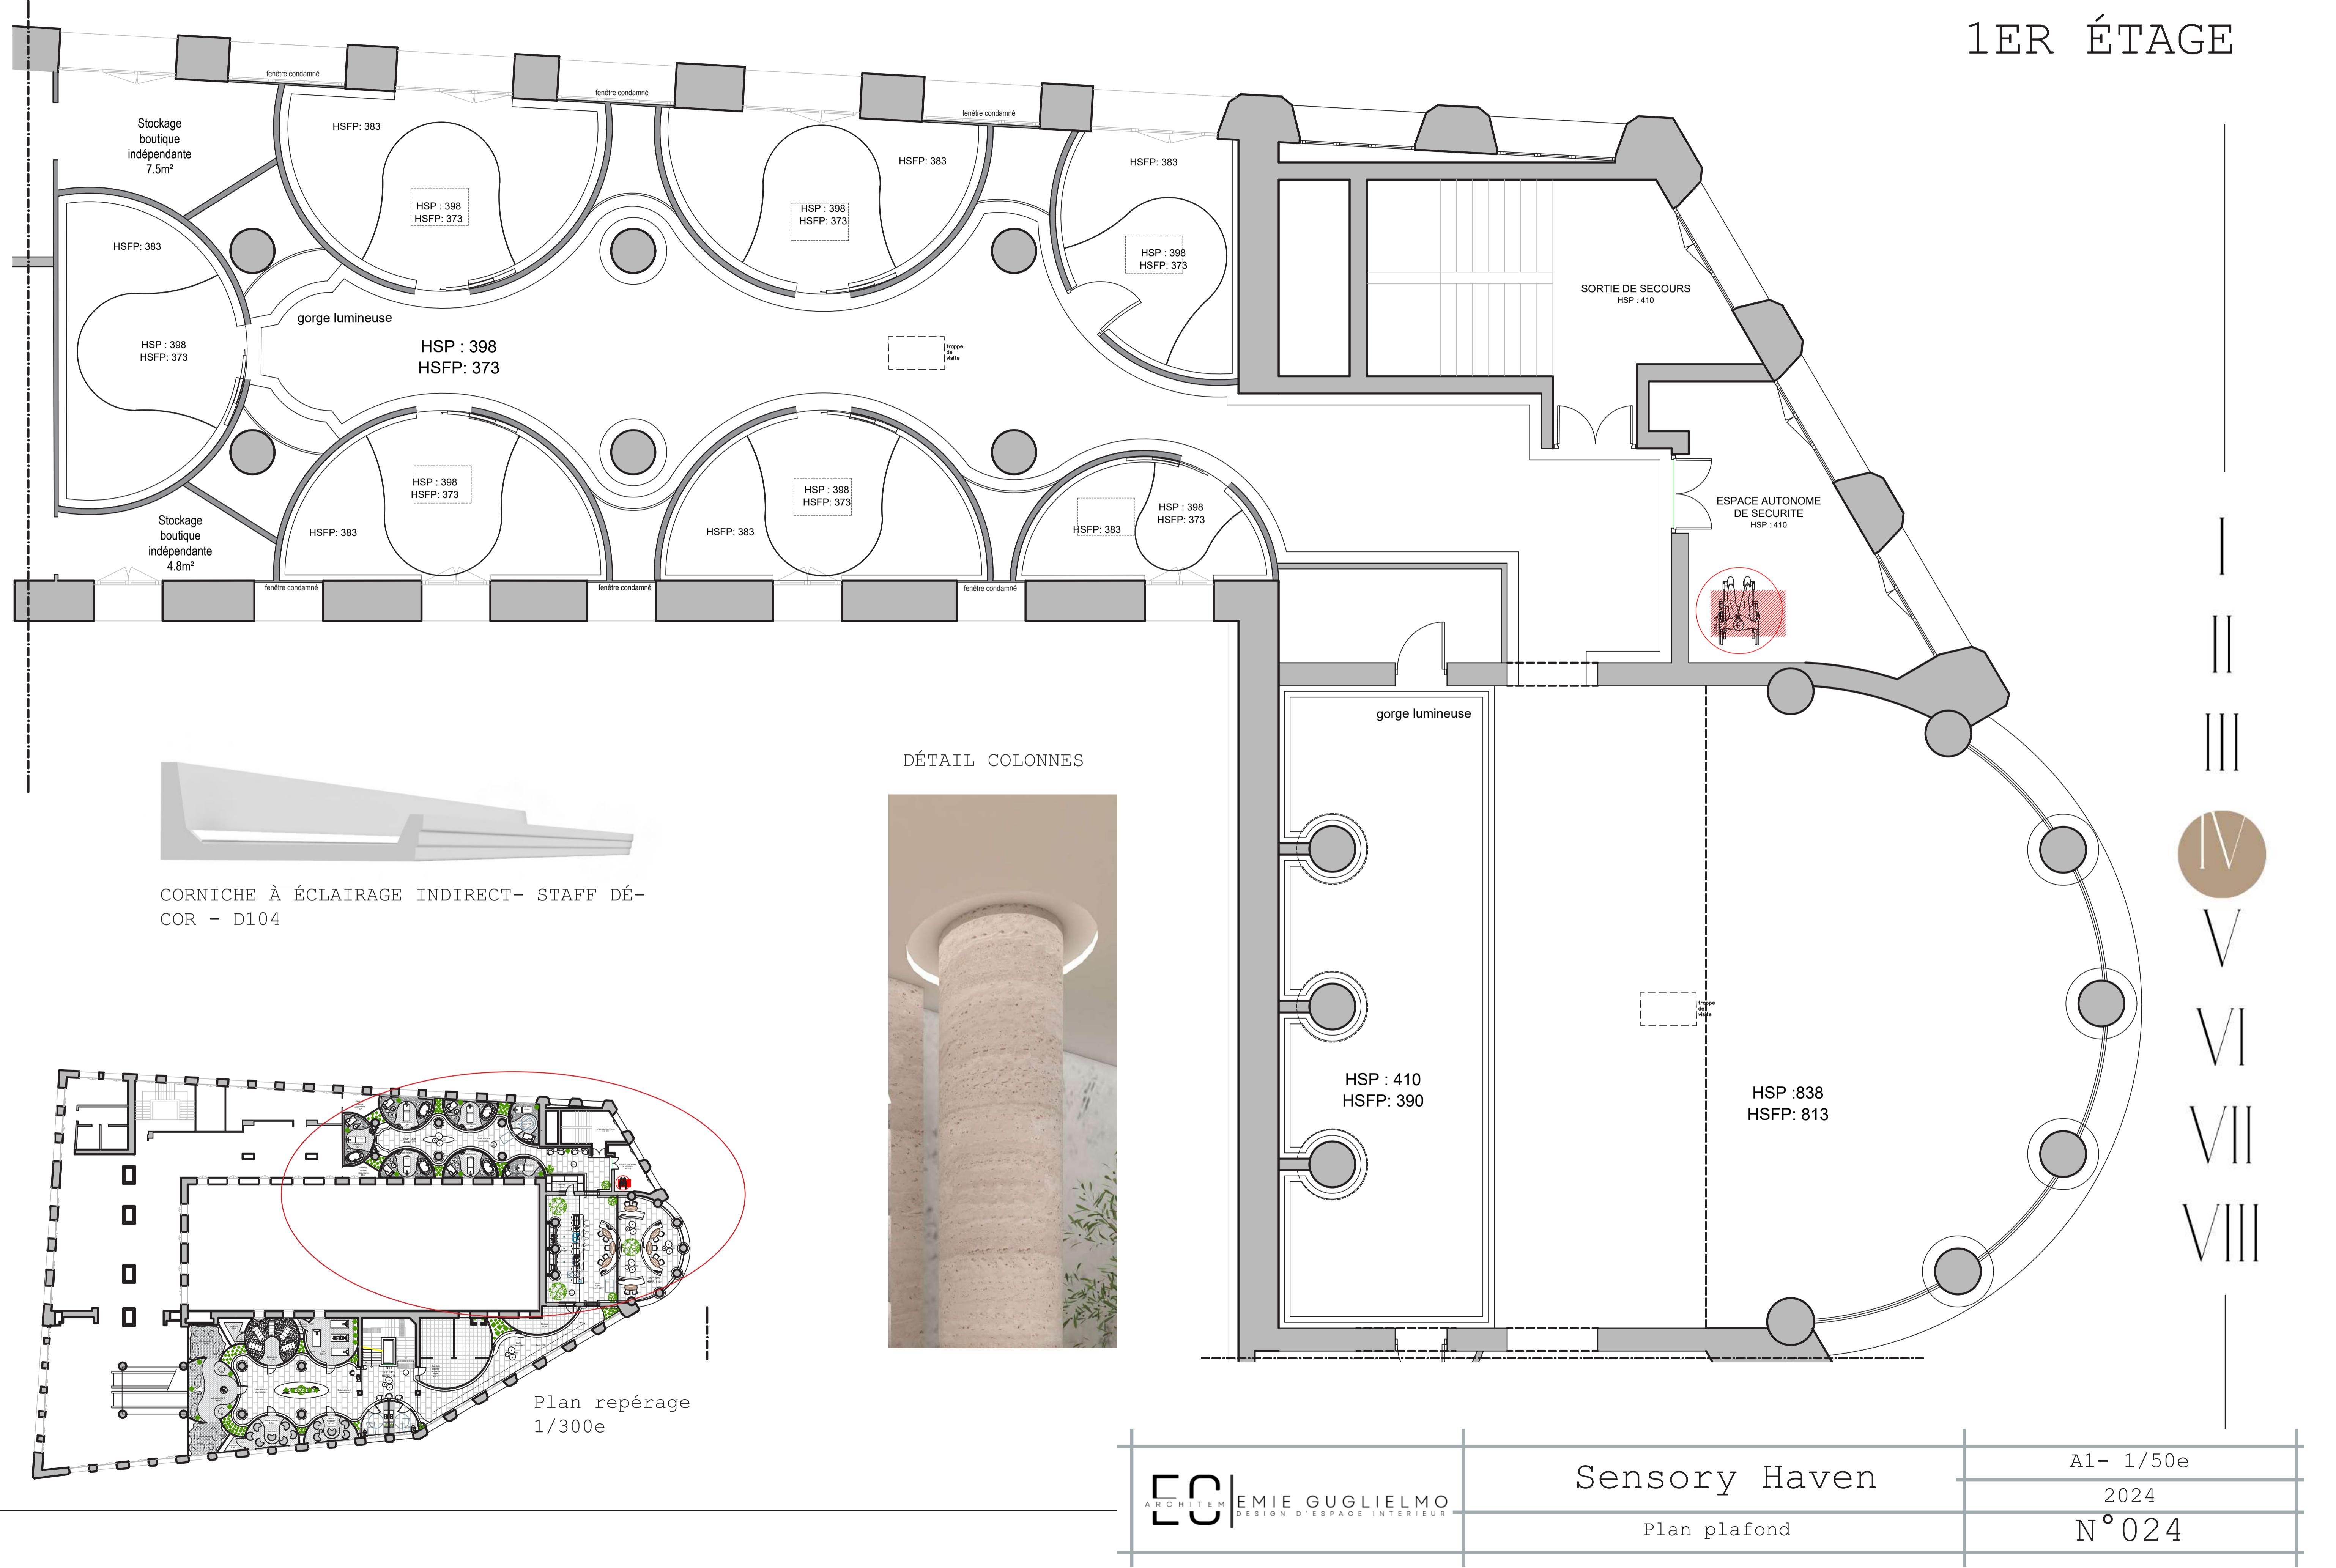



PLAN ELECTRIQUE ET SÉCURITÉ REZ -DE-CHAUSSÉE

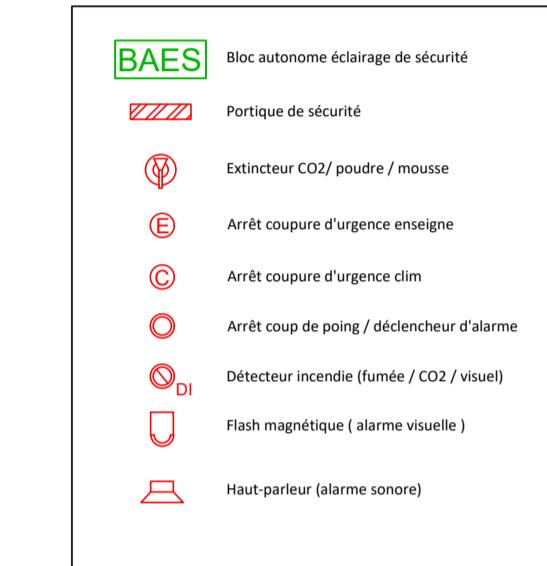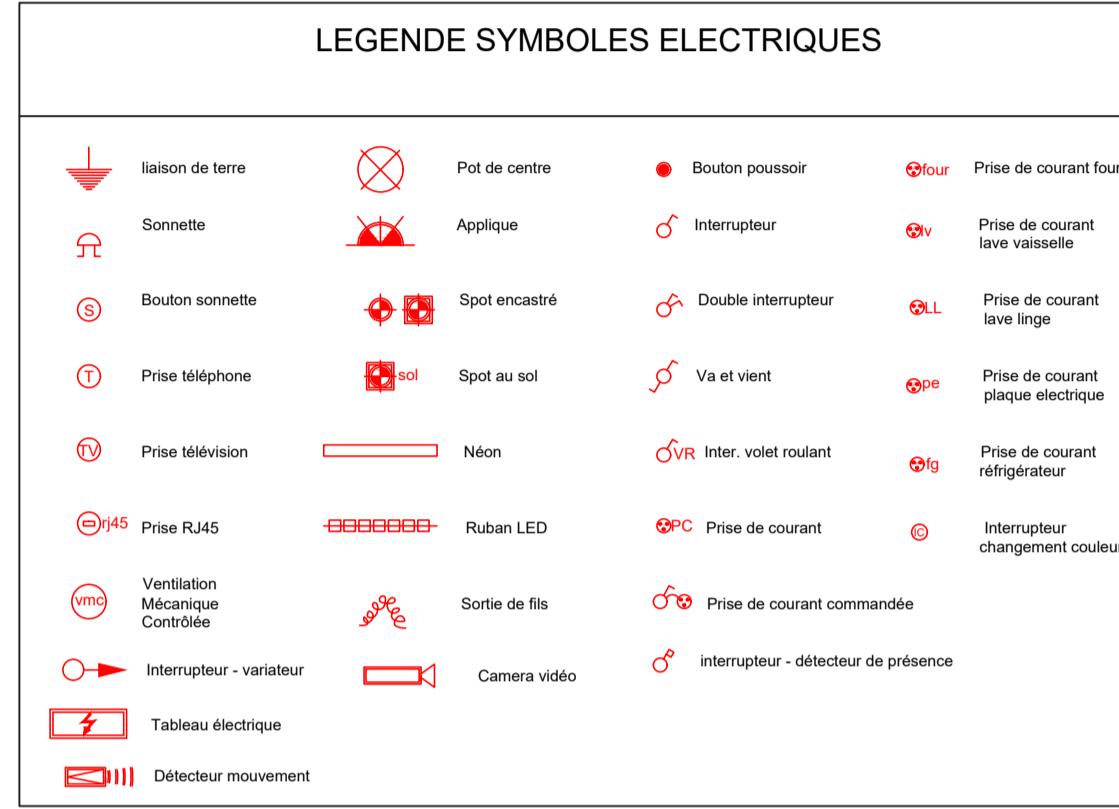

LA SÉCURITÉ DE NOTRE ESPACE EST ASSURÉE PAR PLUSIEURS SYSTÈMES. DES DISPOSITIFS SONORES ET VISUELS, AINSI QUE DES DÉTECTEURS D'INCENDIE, SONT INSTALLÉS À DIVERS ENDROITS. DES BORNES BAES SONT ÉGALEMENT DISPOSÉES POUR GUIDER LES VISITEURS VERS LES SORTIES DE SECOURS LES PLUS PROCHES. CES MESURES PERMETTENT DE GARANTIR UNE PROTECTION OPTIMALE ET UNE ÉVACUATION RAPIDE EN CAS D'URGENCE.

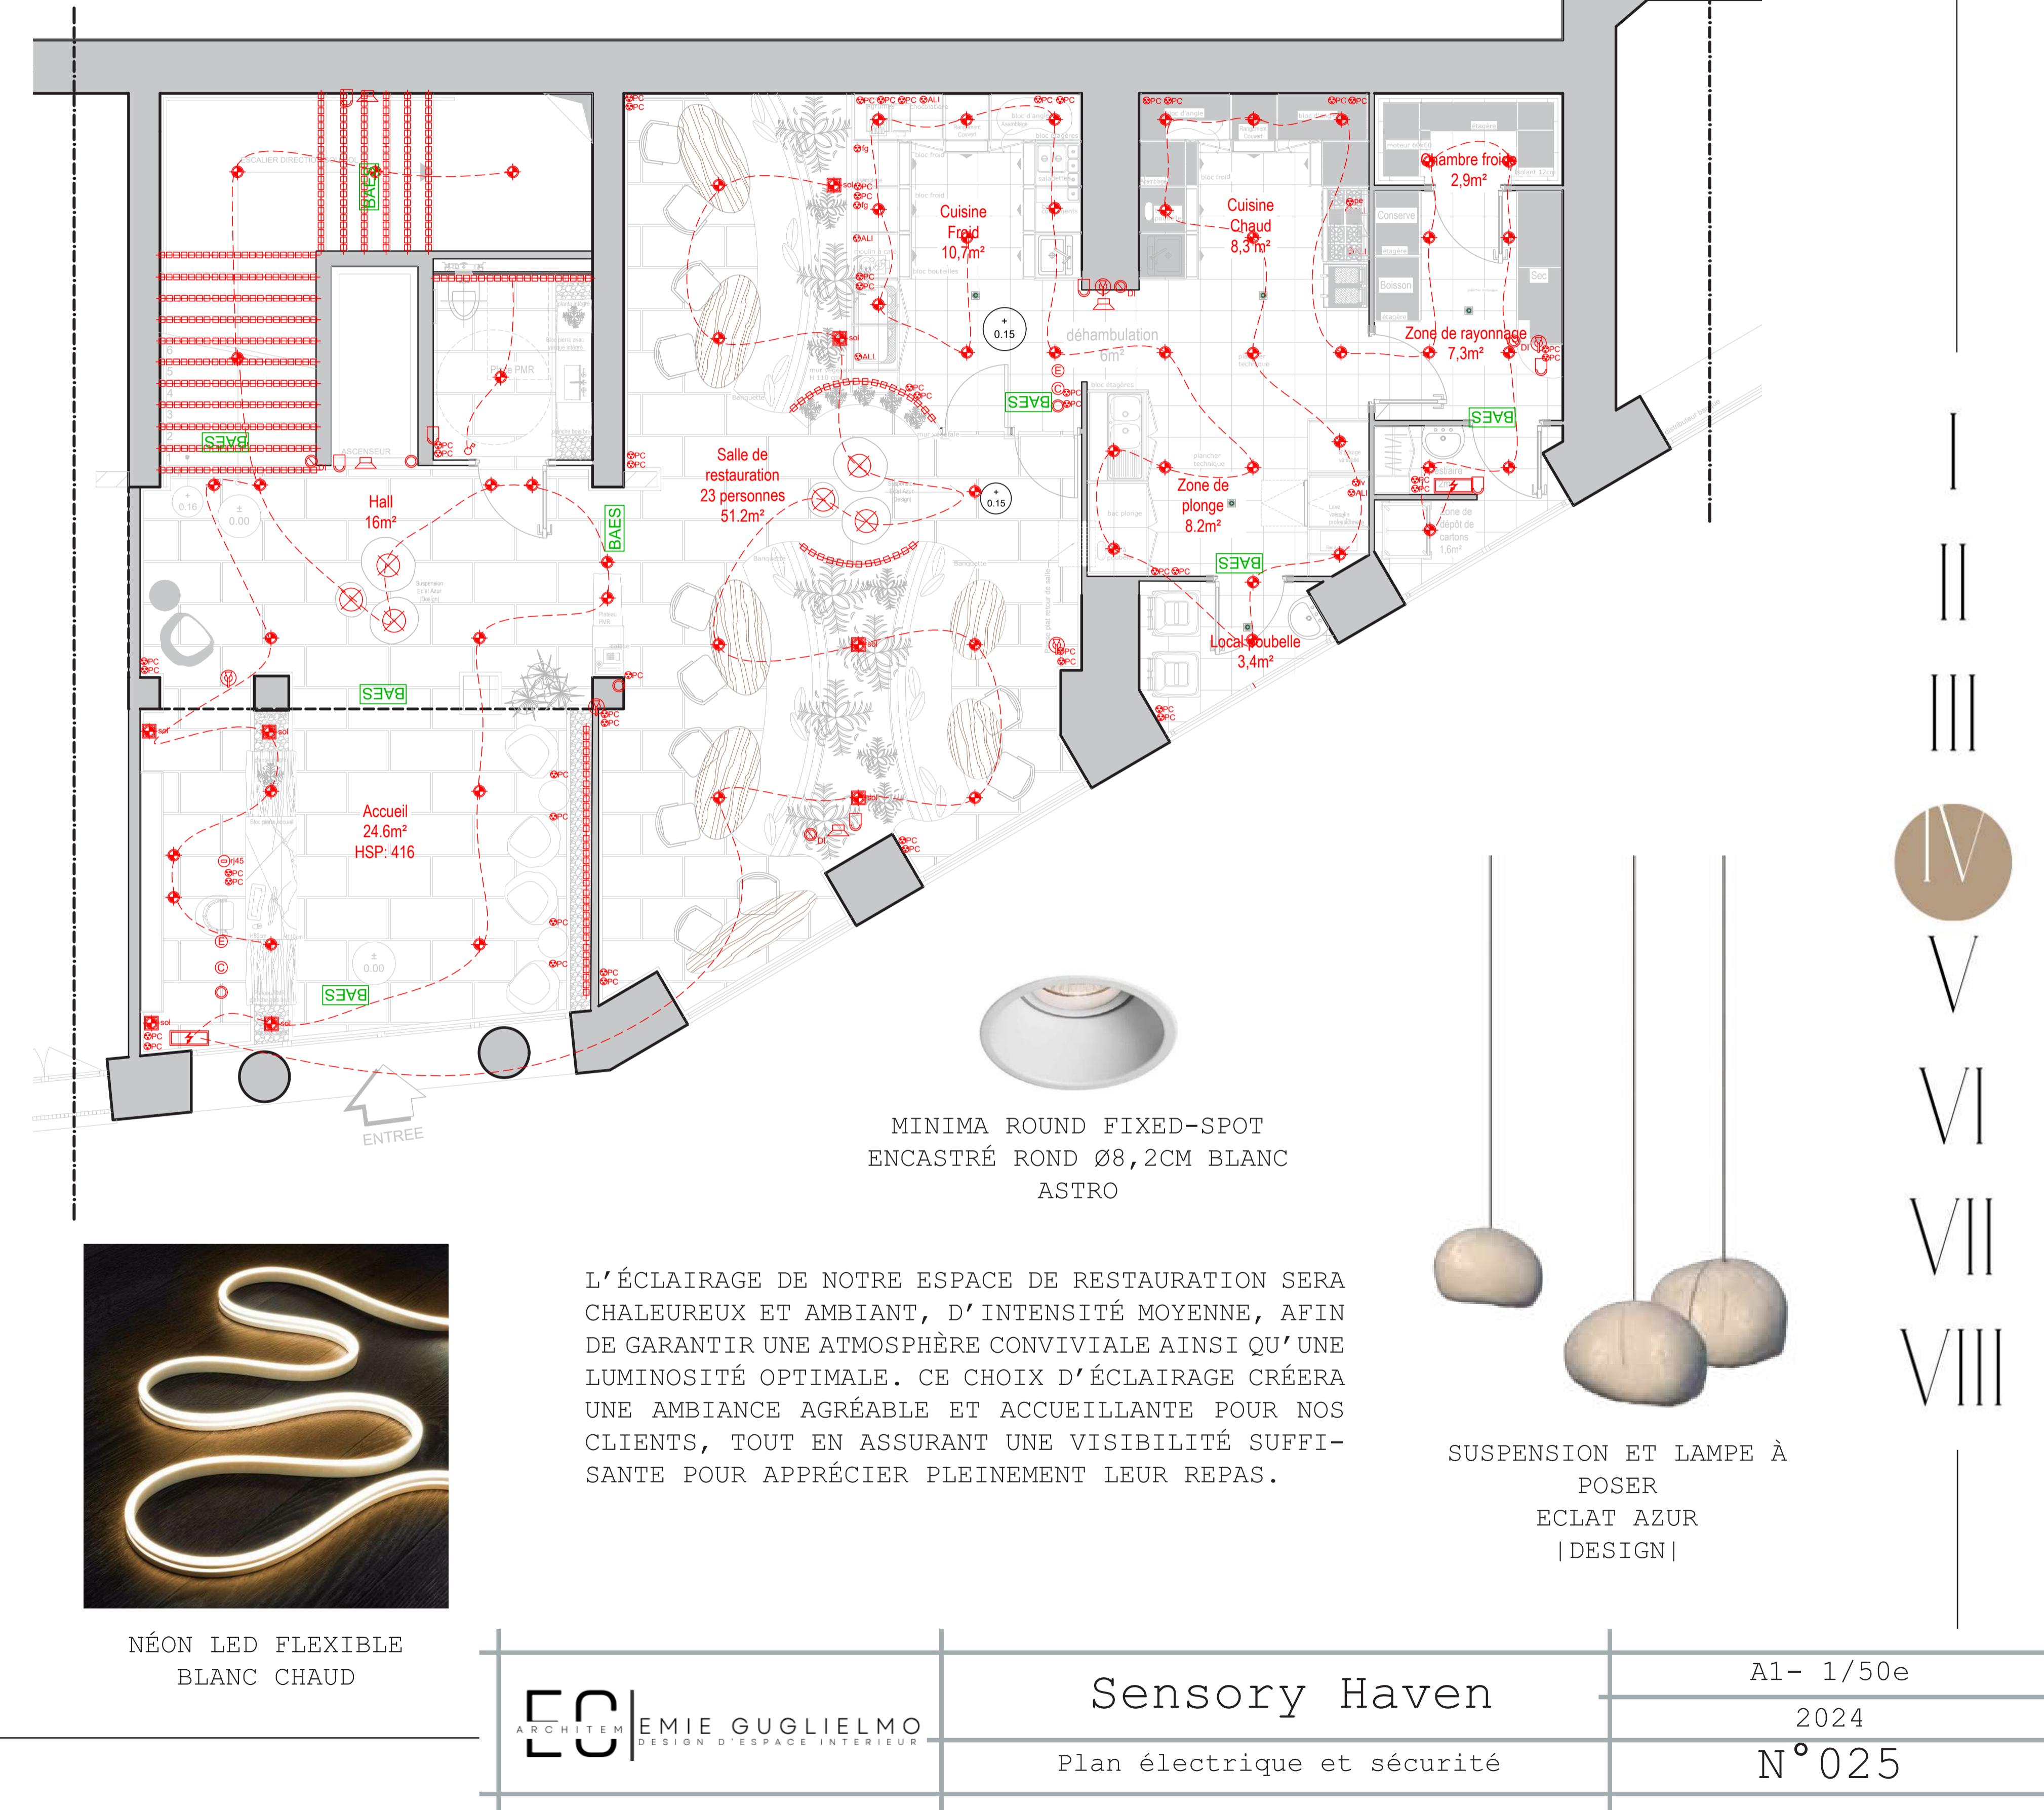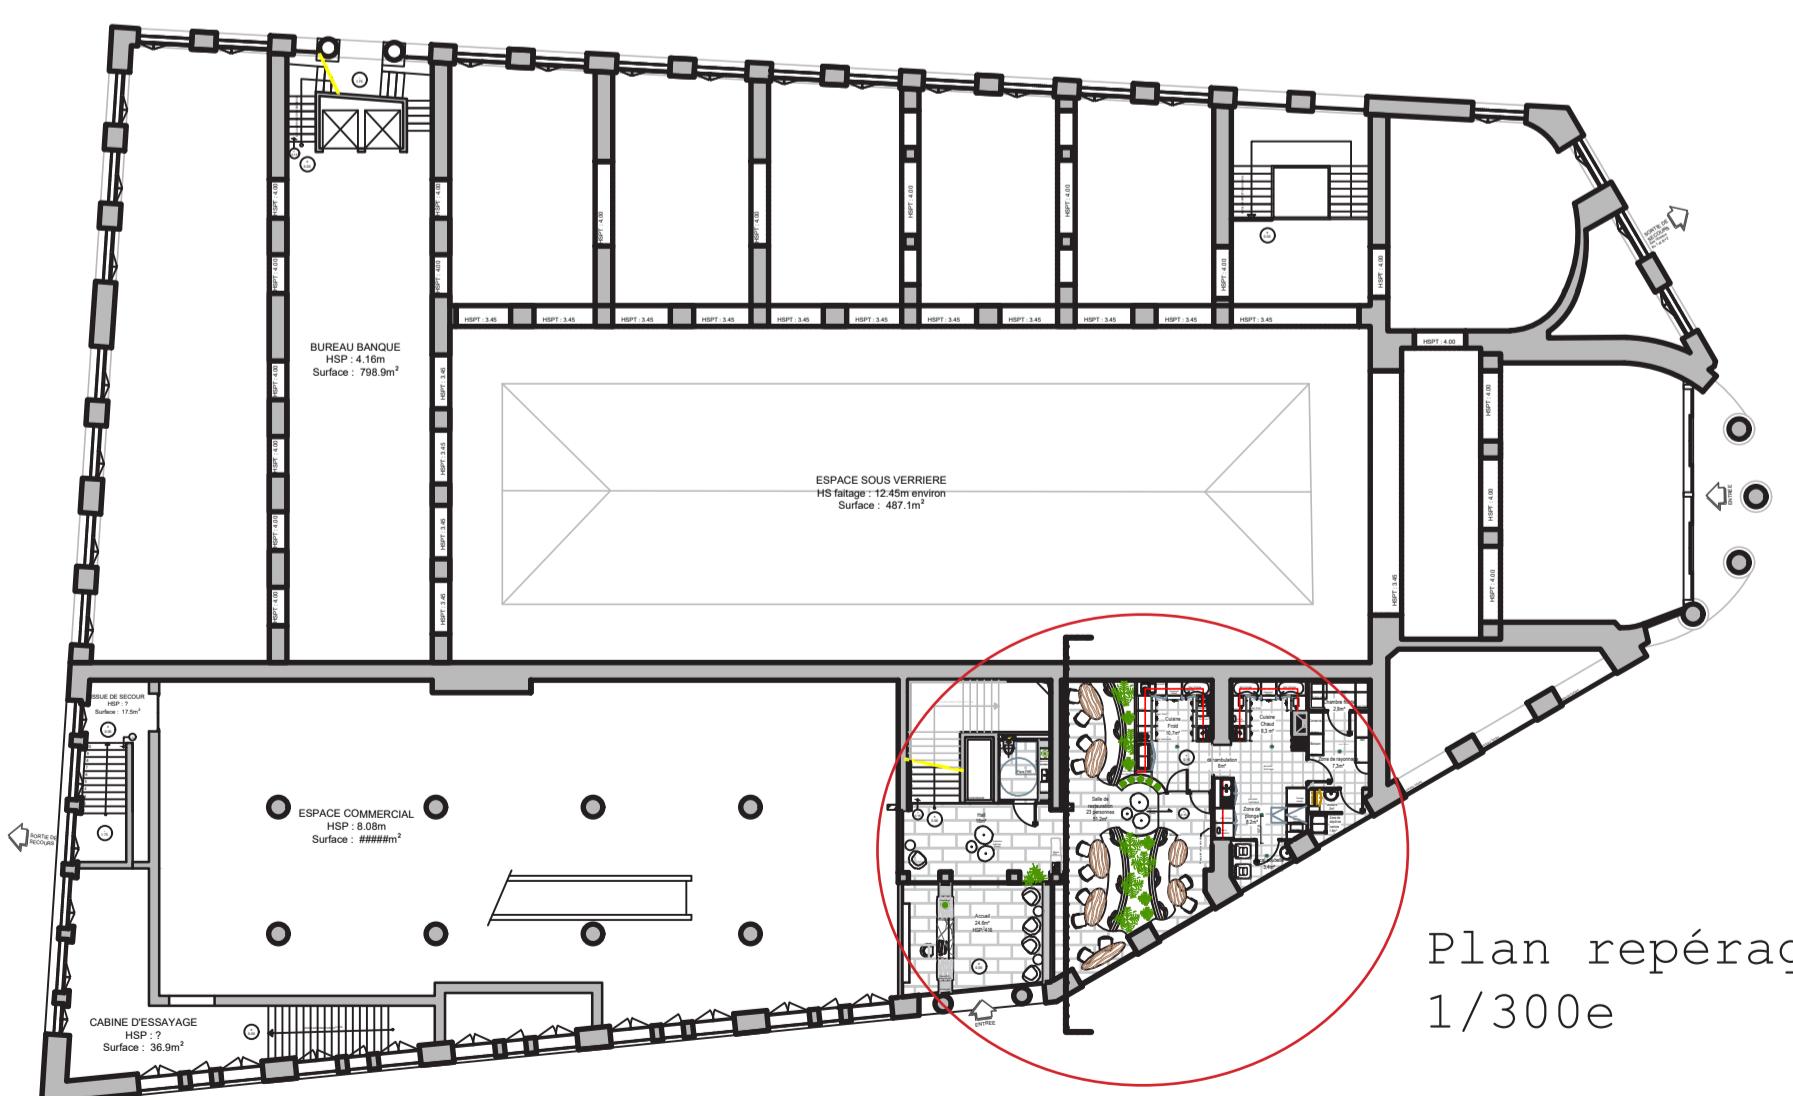

PLAN ELECTRIQUE
ET SÉCURITÉ
1ER ÉTAGE

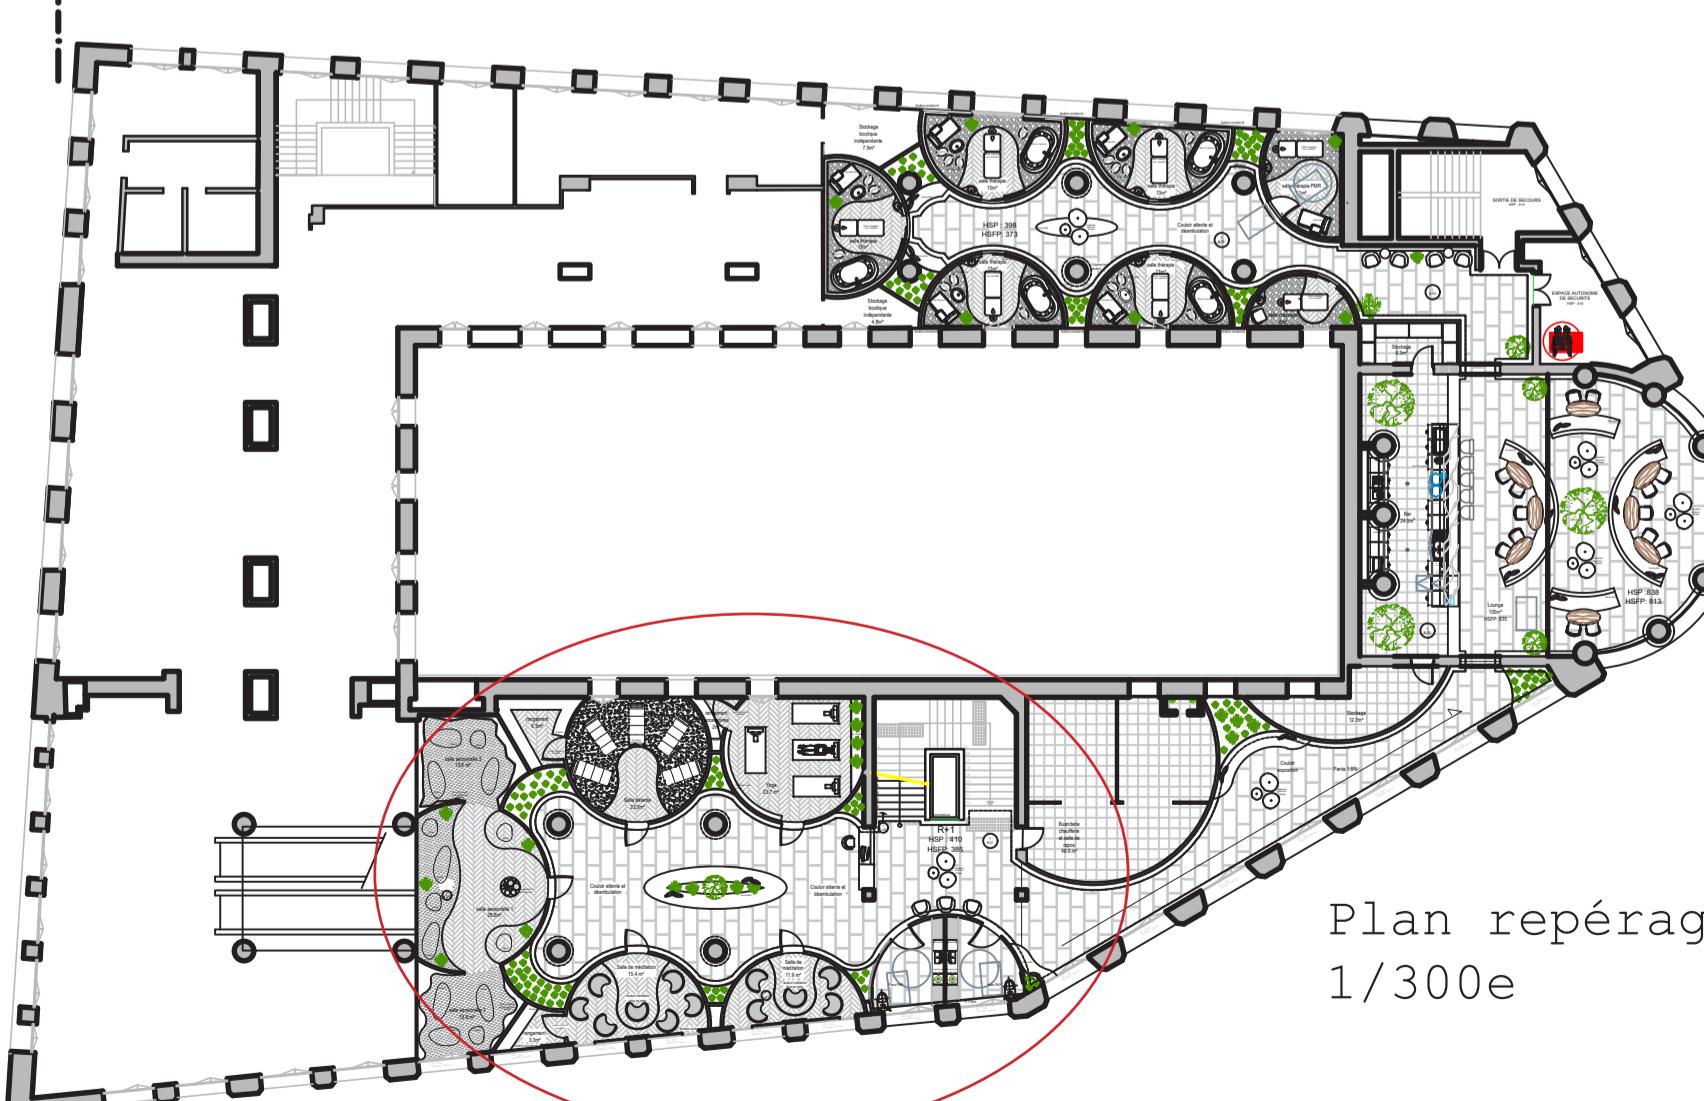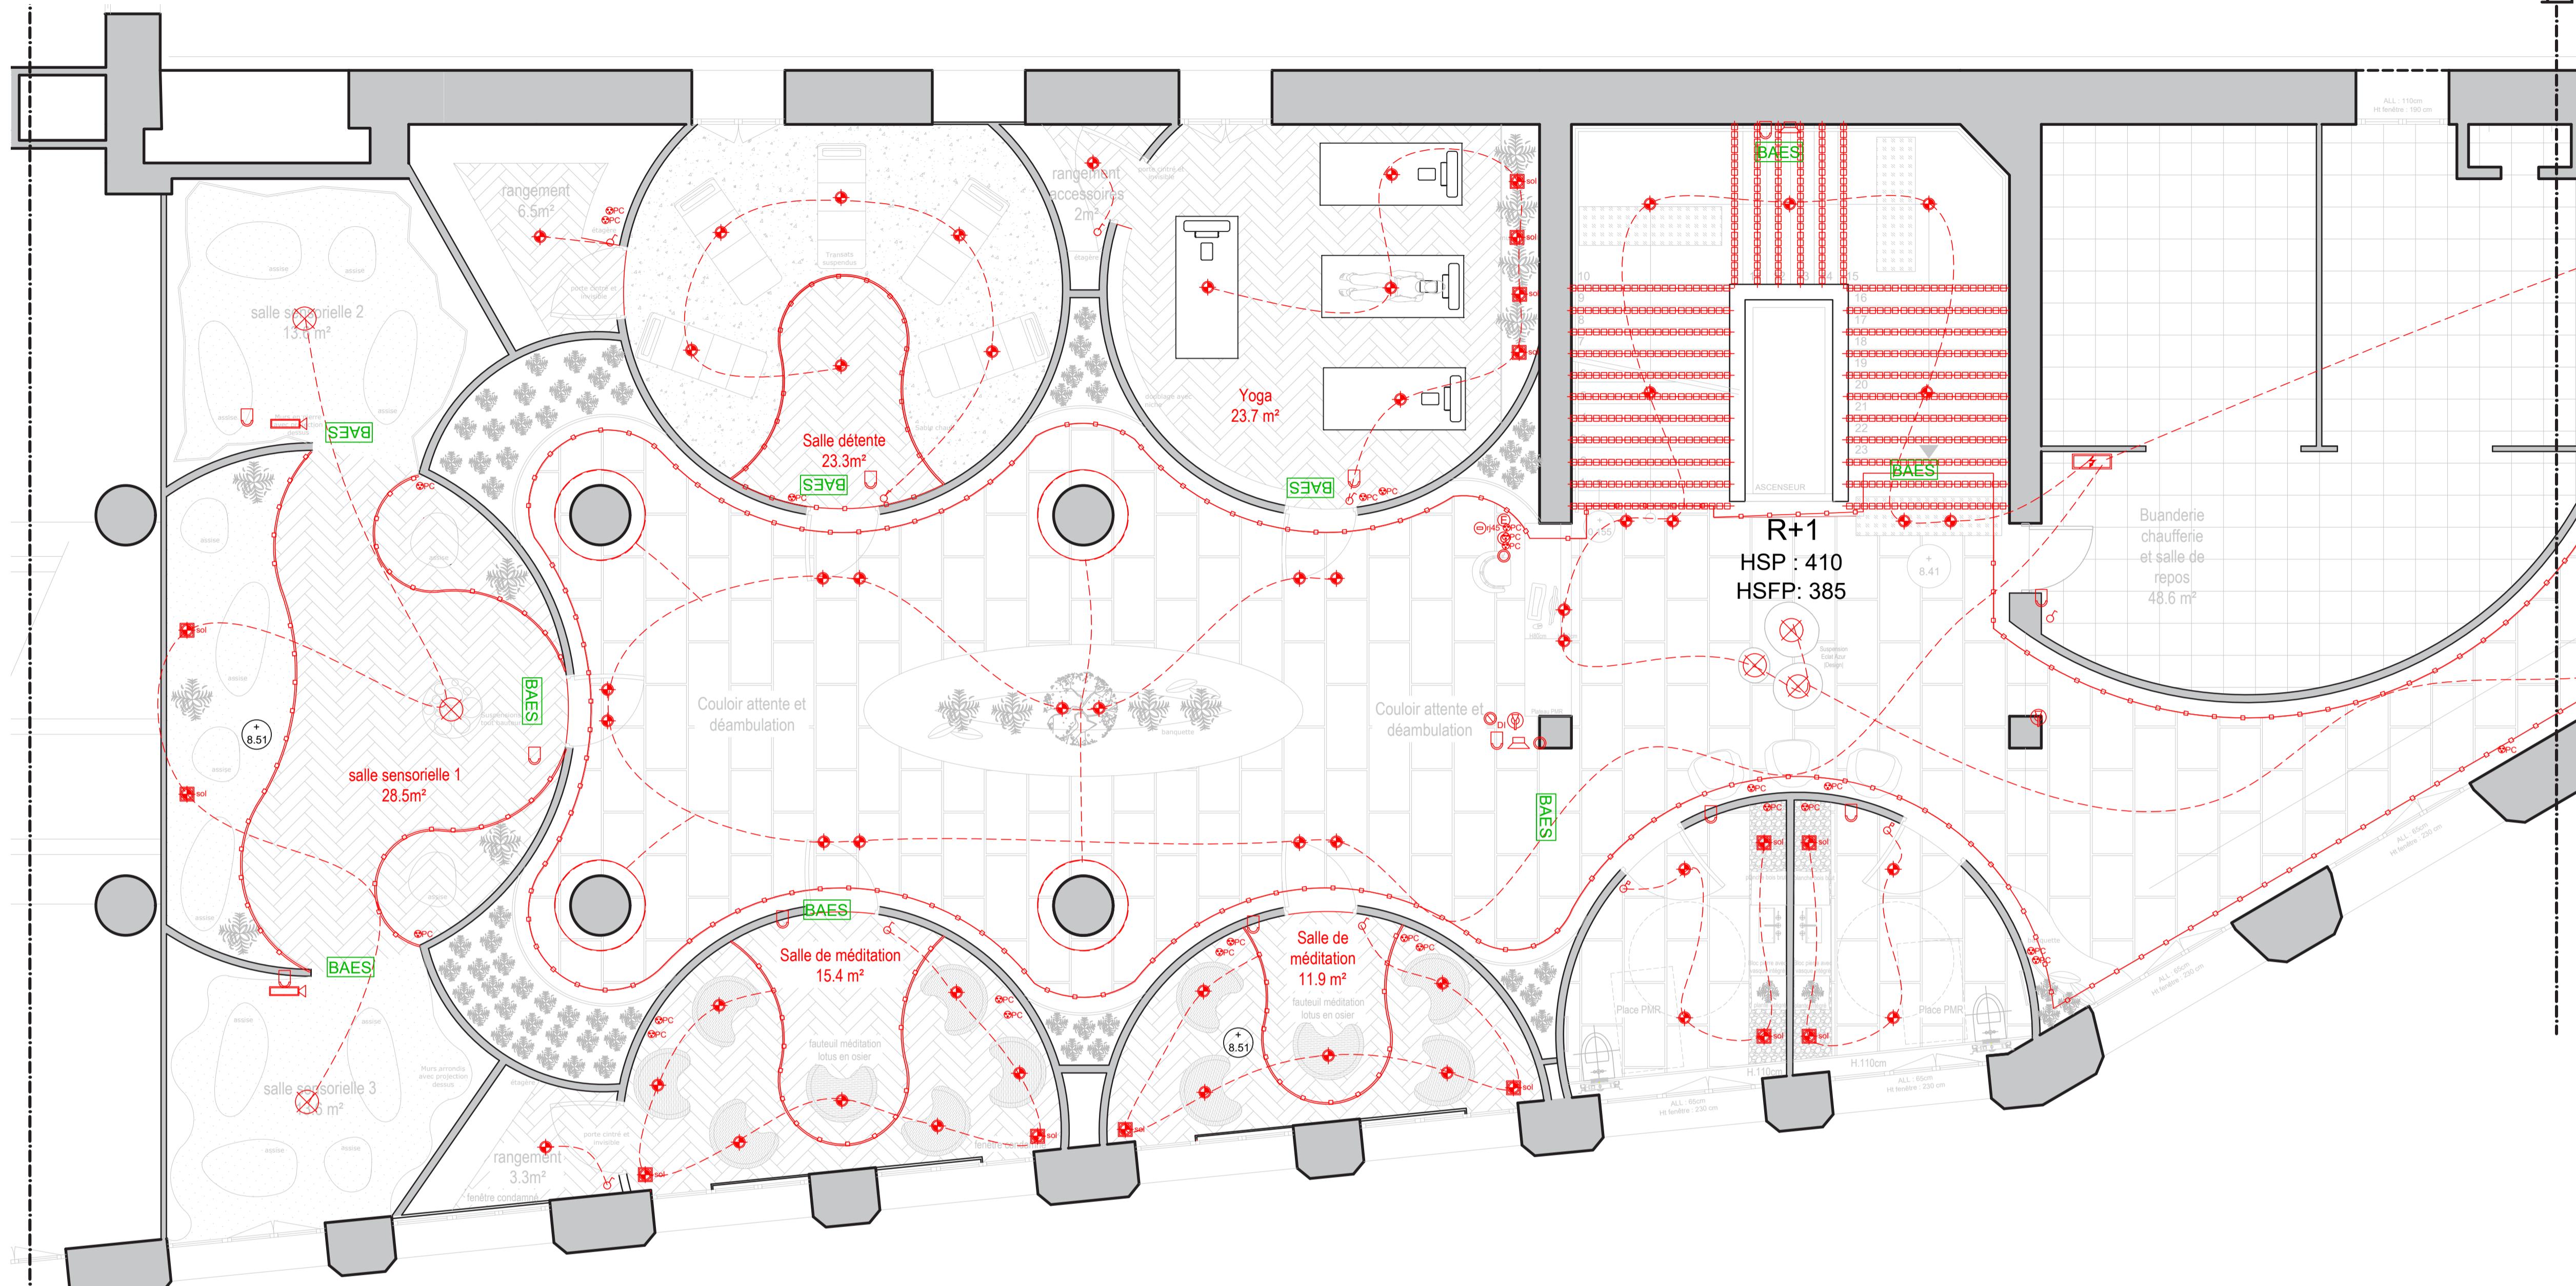


Plan repérage
1/300e

LEGENDE SYMBOLES ELECTRIQUES

liaison de terre	Pot de centre	Bouton poussoir	Prise de courant four
Sonnette	Applique	Interrupteur	Prise de courant lave vaisselle
Bouton sonnette	Spot encastré	Double interrupteur	Prise de courant lave linge
Prise téléphone	Spot au sol	Va et vient	Prise de courant plaque électrique
Prise télévision	Néon	Int. volet roulant	Prise de courant réfrigérateur
Prise RJ45	Ruban LED	Prise de courant	Interrupteur changement couleur
Ventilation Mécanique Contrôlée	Sortie de fil	Prise de courant commande	Interrupteur - détecteur de présence
Interrupteur - variateur	Camera vidéo		
Tableau électrique			
Détecteur mouvement			


BAES	Bloc autonome éclairage de sécurité
	Portique de sécurité
	Extincteur CO2 poudre / mousse
	Arrêt coupure d'urgence enseigne
	Arrêt coupure d'urgence clim
	Arrêt coup de poing / déclencheur d'alarme
	Détecteur incendie (fumée / CO2 / visuel)
	Flash magnétique (alarme visuelle)
	Haut-parleur (alarme sonore)

PLAN ELECTRIQUE
ET SÉCURITÉ
1ER ÉTAGE

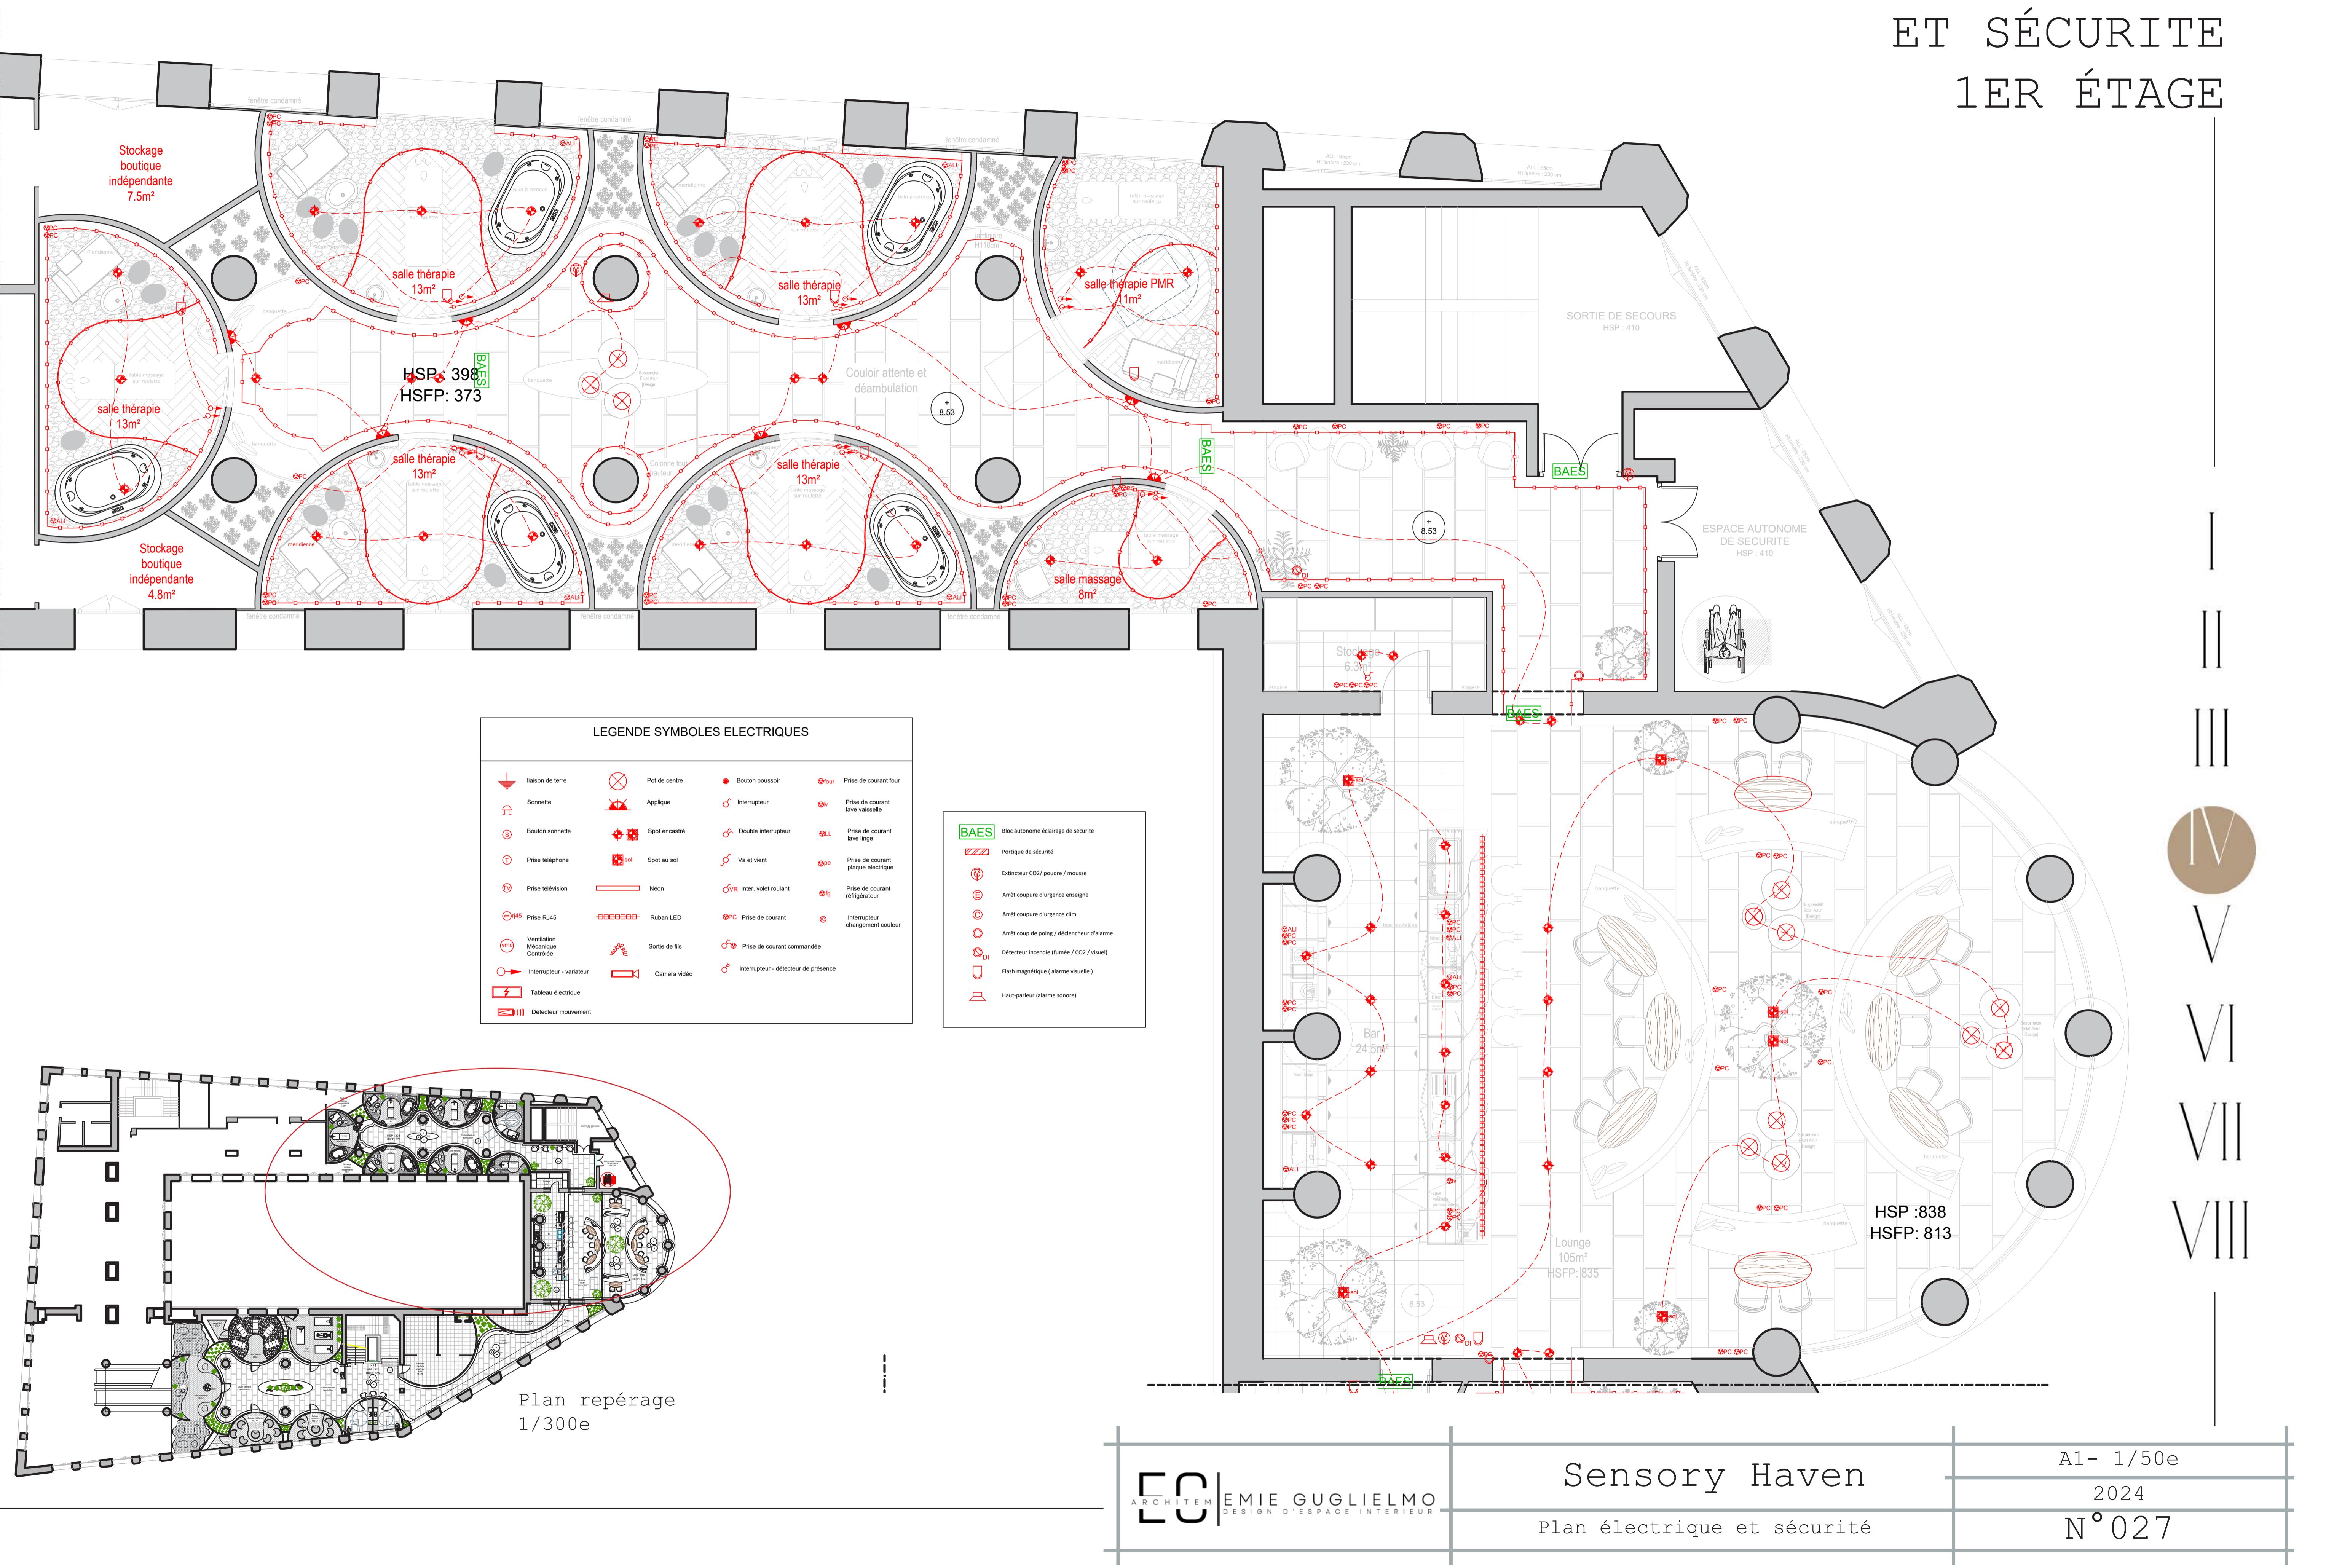


PLAN CLIMATISATION REZ -DE-CHAUSSÉE


LA CLIMATISATION DE NOTRE ESPACE SERA ASSURÉE PAR DES CLIMATISEURS GAINABLES, AVEC DES SORTIES ET DES REPRISES JUDICIEUSEMENT DISPOSÉES. CELA PERMETTRA UNE BONNE AÉRATION DE L'ENSEMBLE DE L'ESPACE, GARANTISSANT AINSI UN ENVIRONNEMENT AGRÉABLE ET FRAIS POUR TOUS.

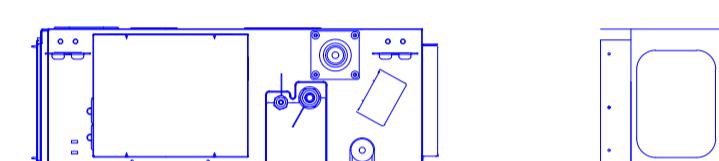


Plan et
coupe
1/10e

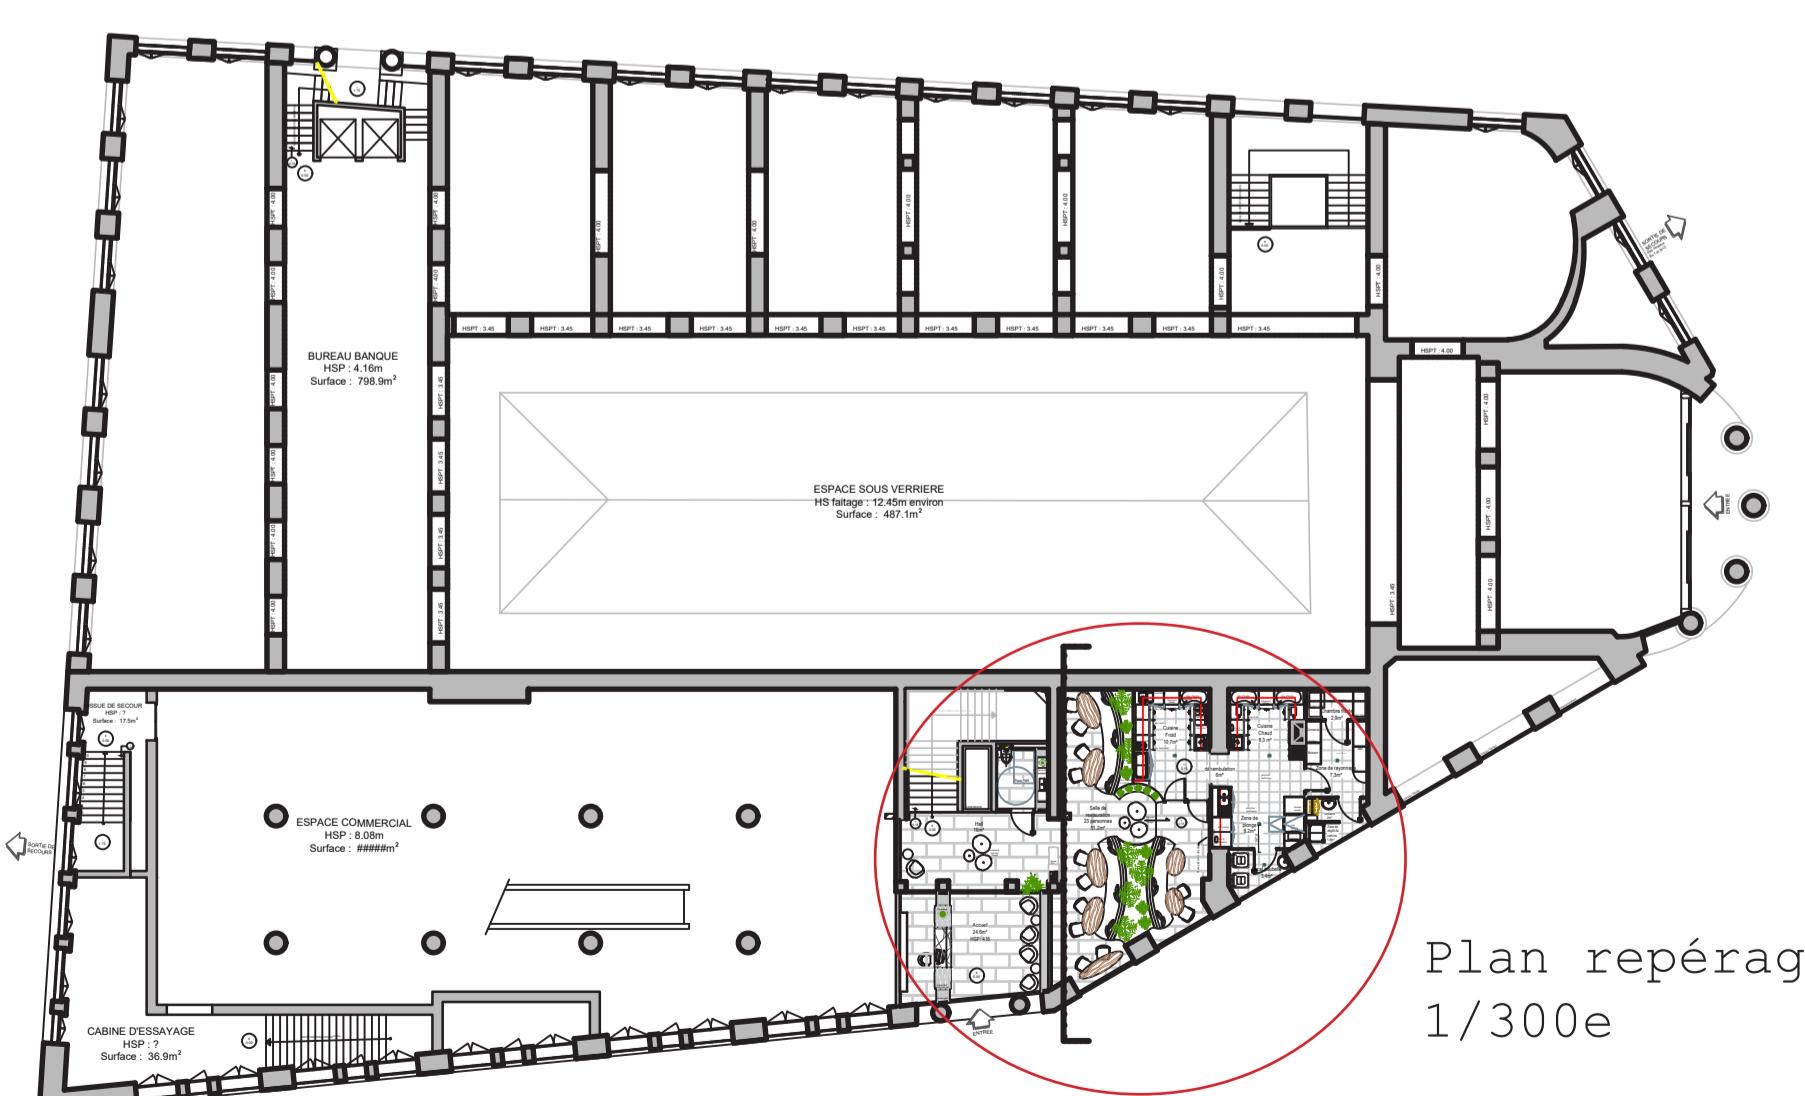

Plan repérage
1/300e

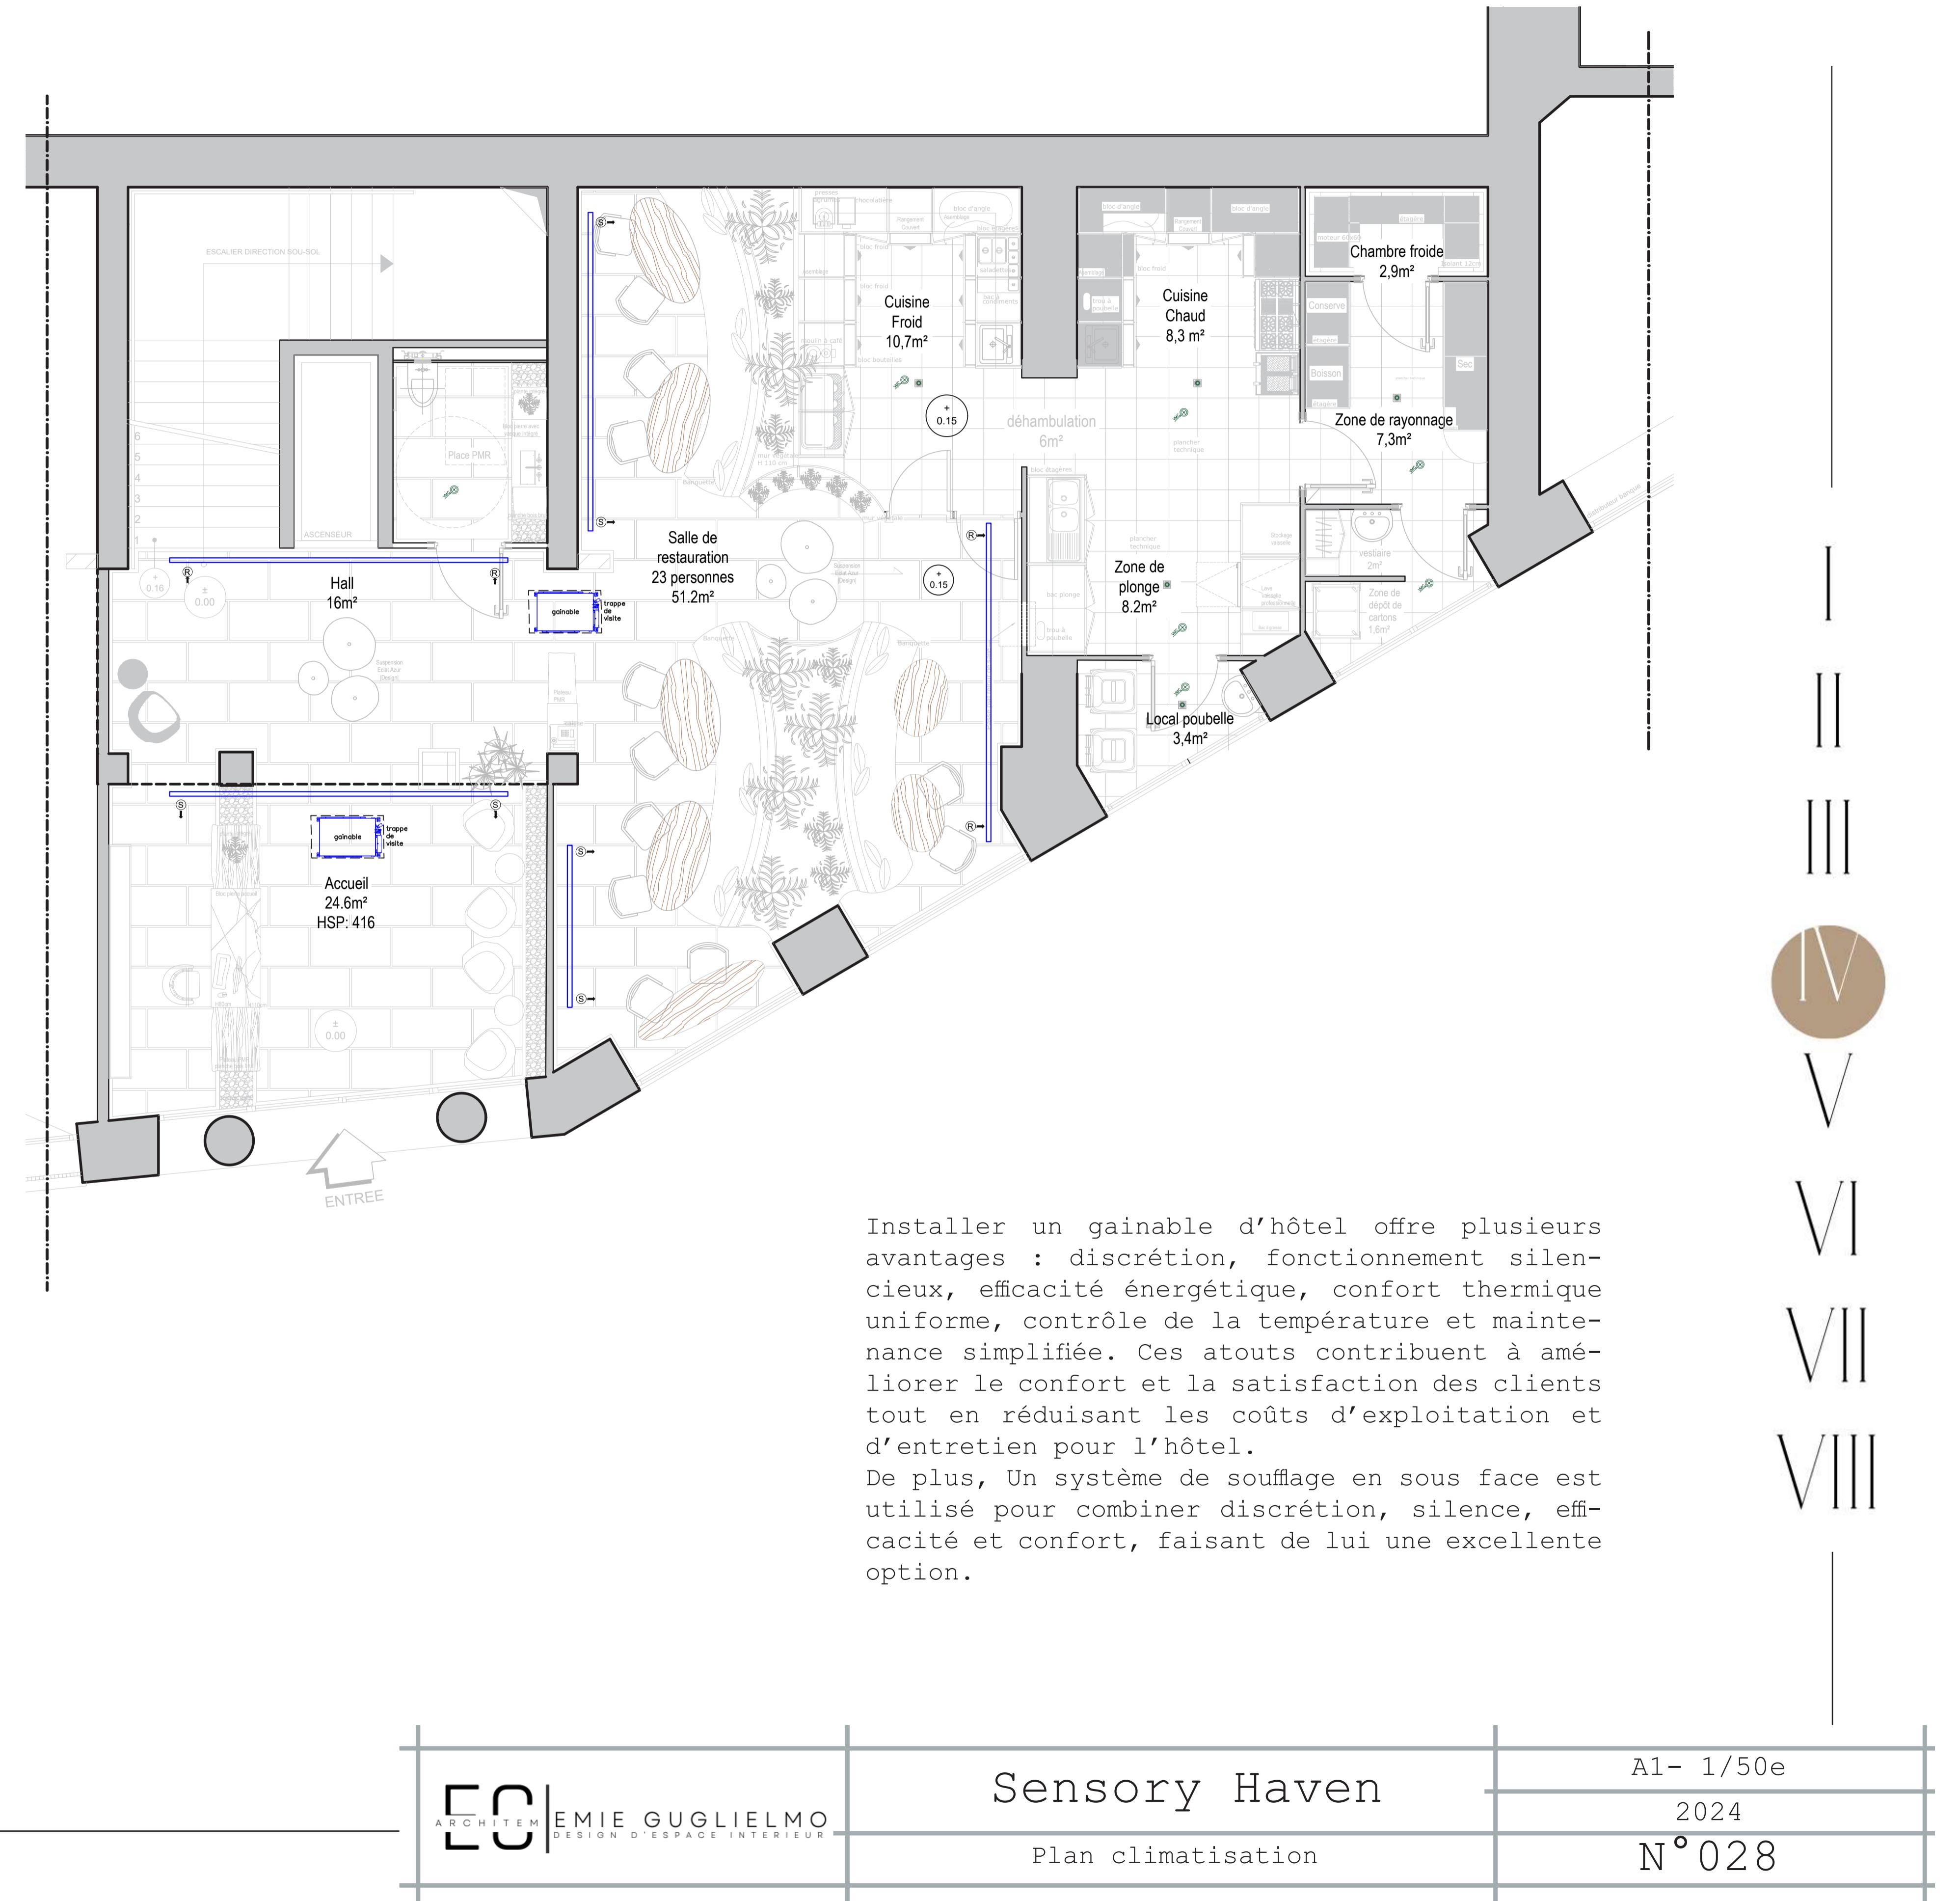

PLAN CLIMATISATION
1ER ÉTAGE

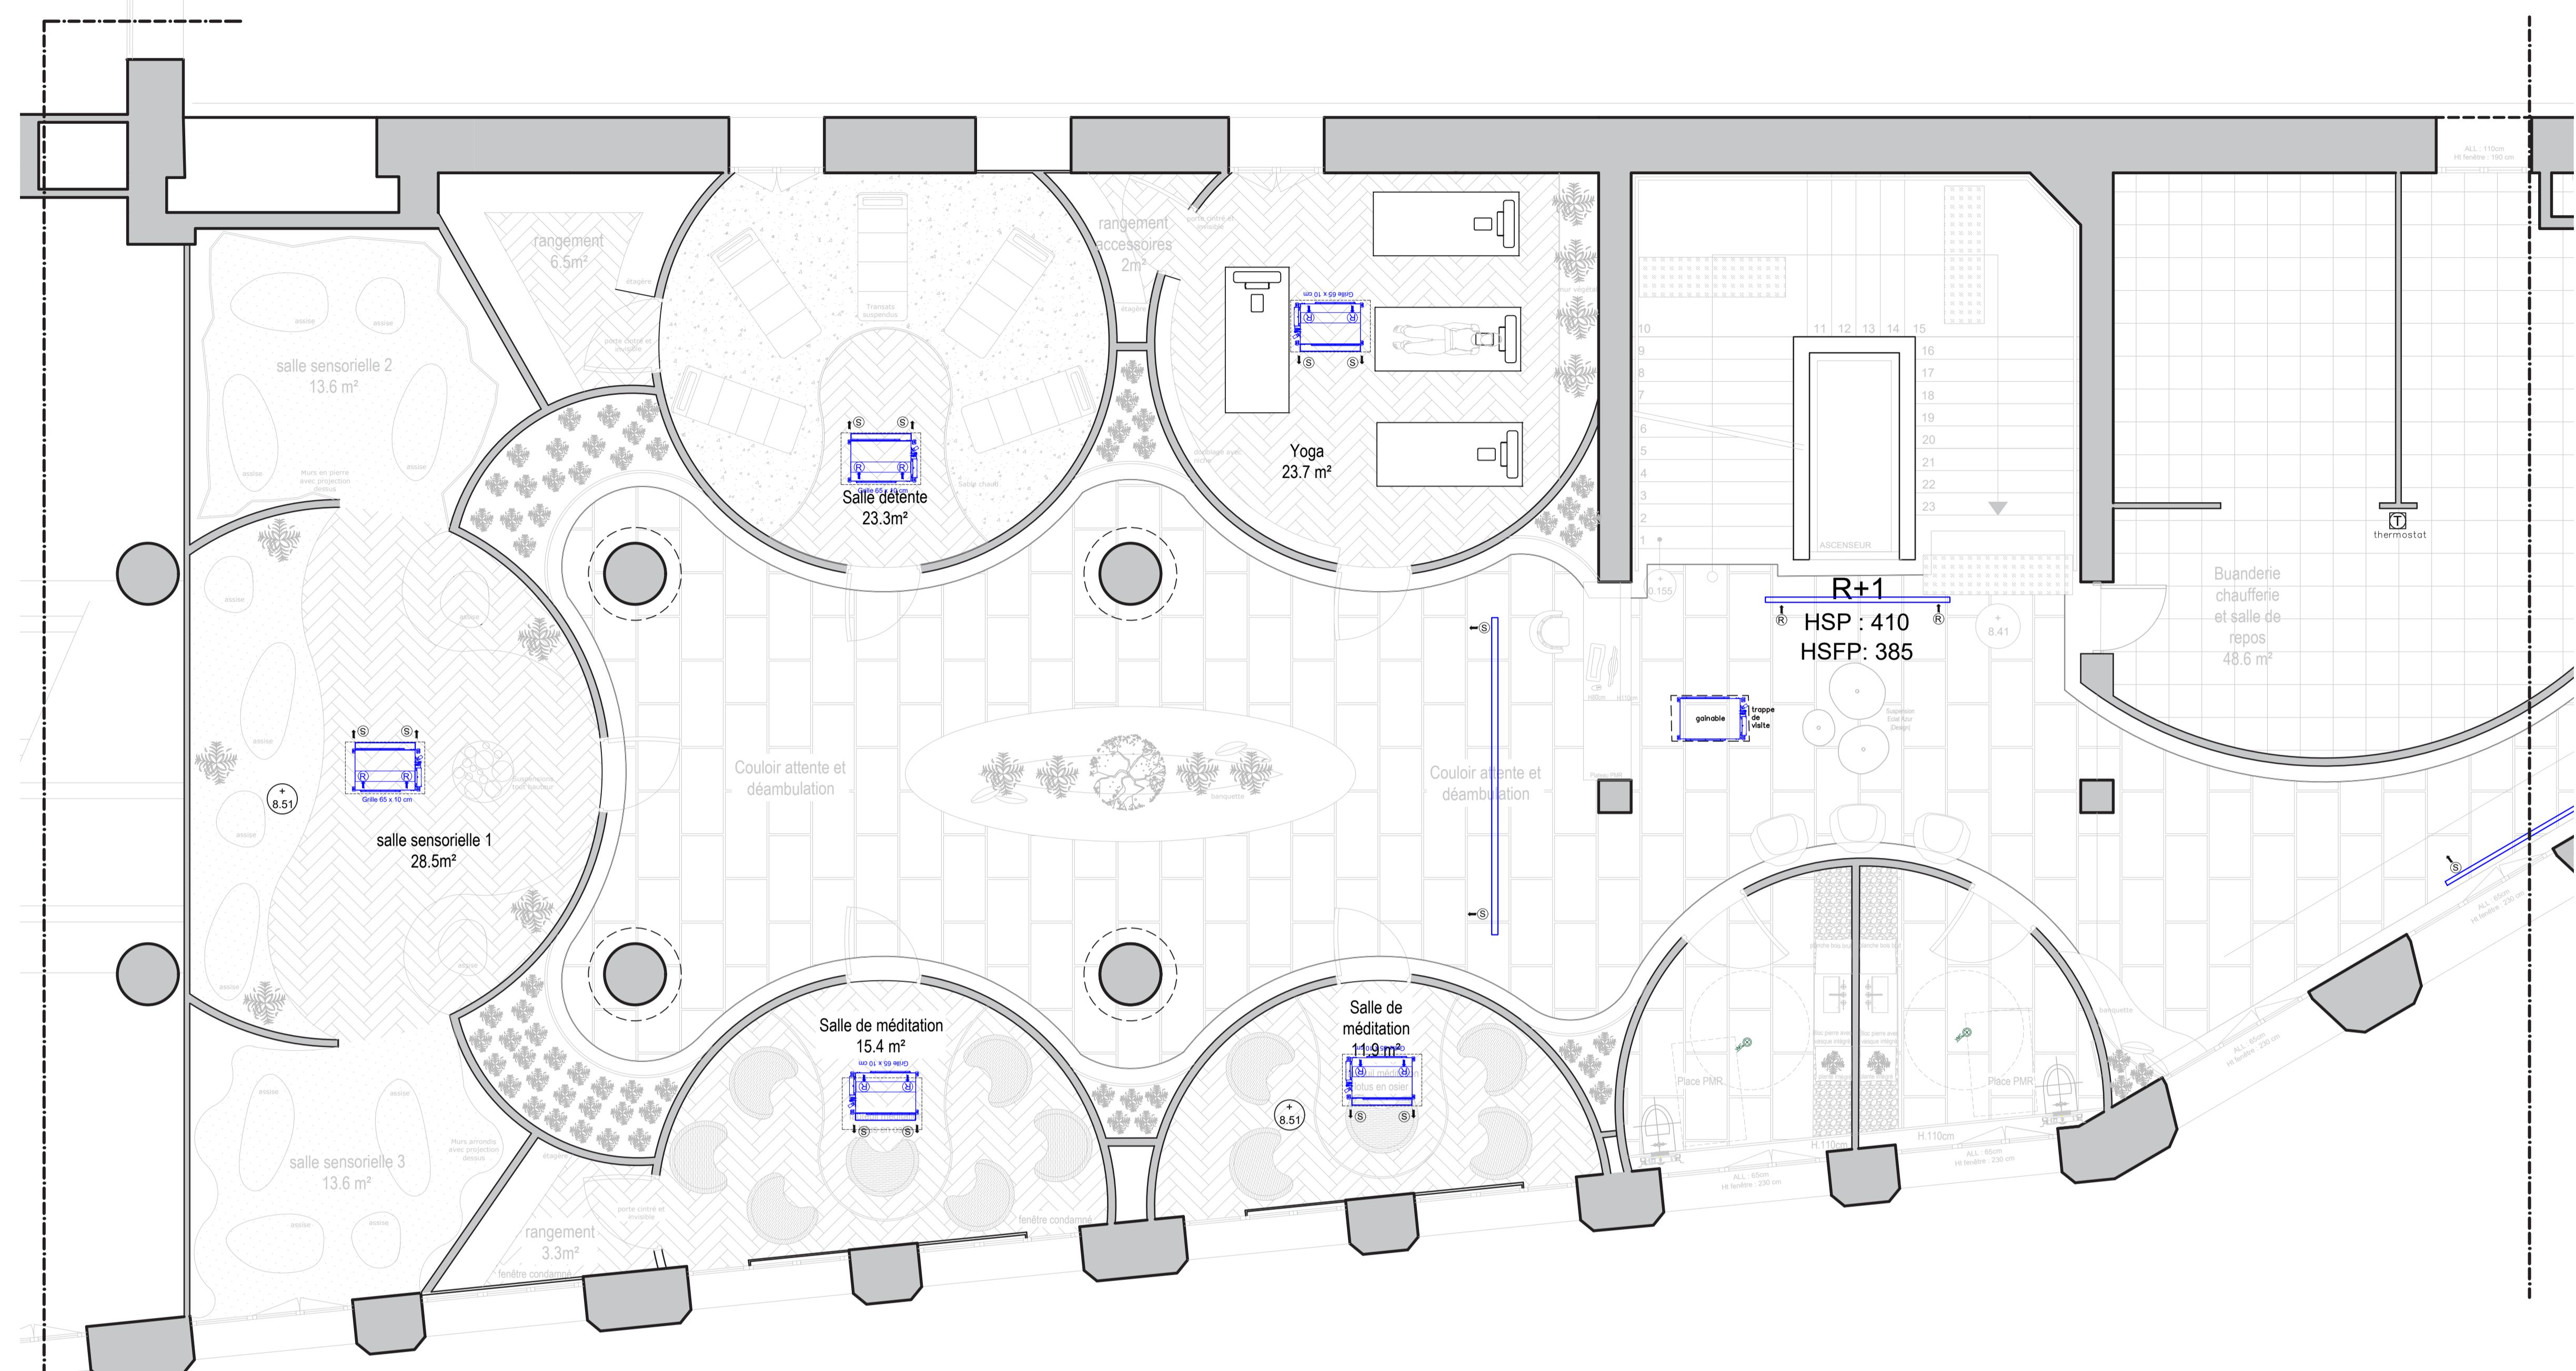

I
II
III


IV

V

VI

VII


VIII

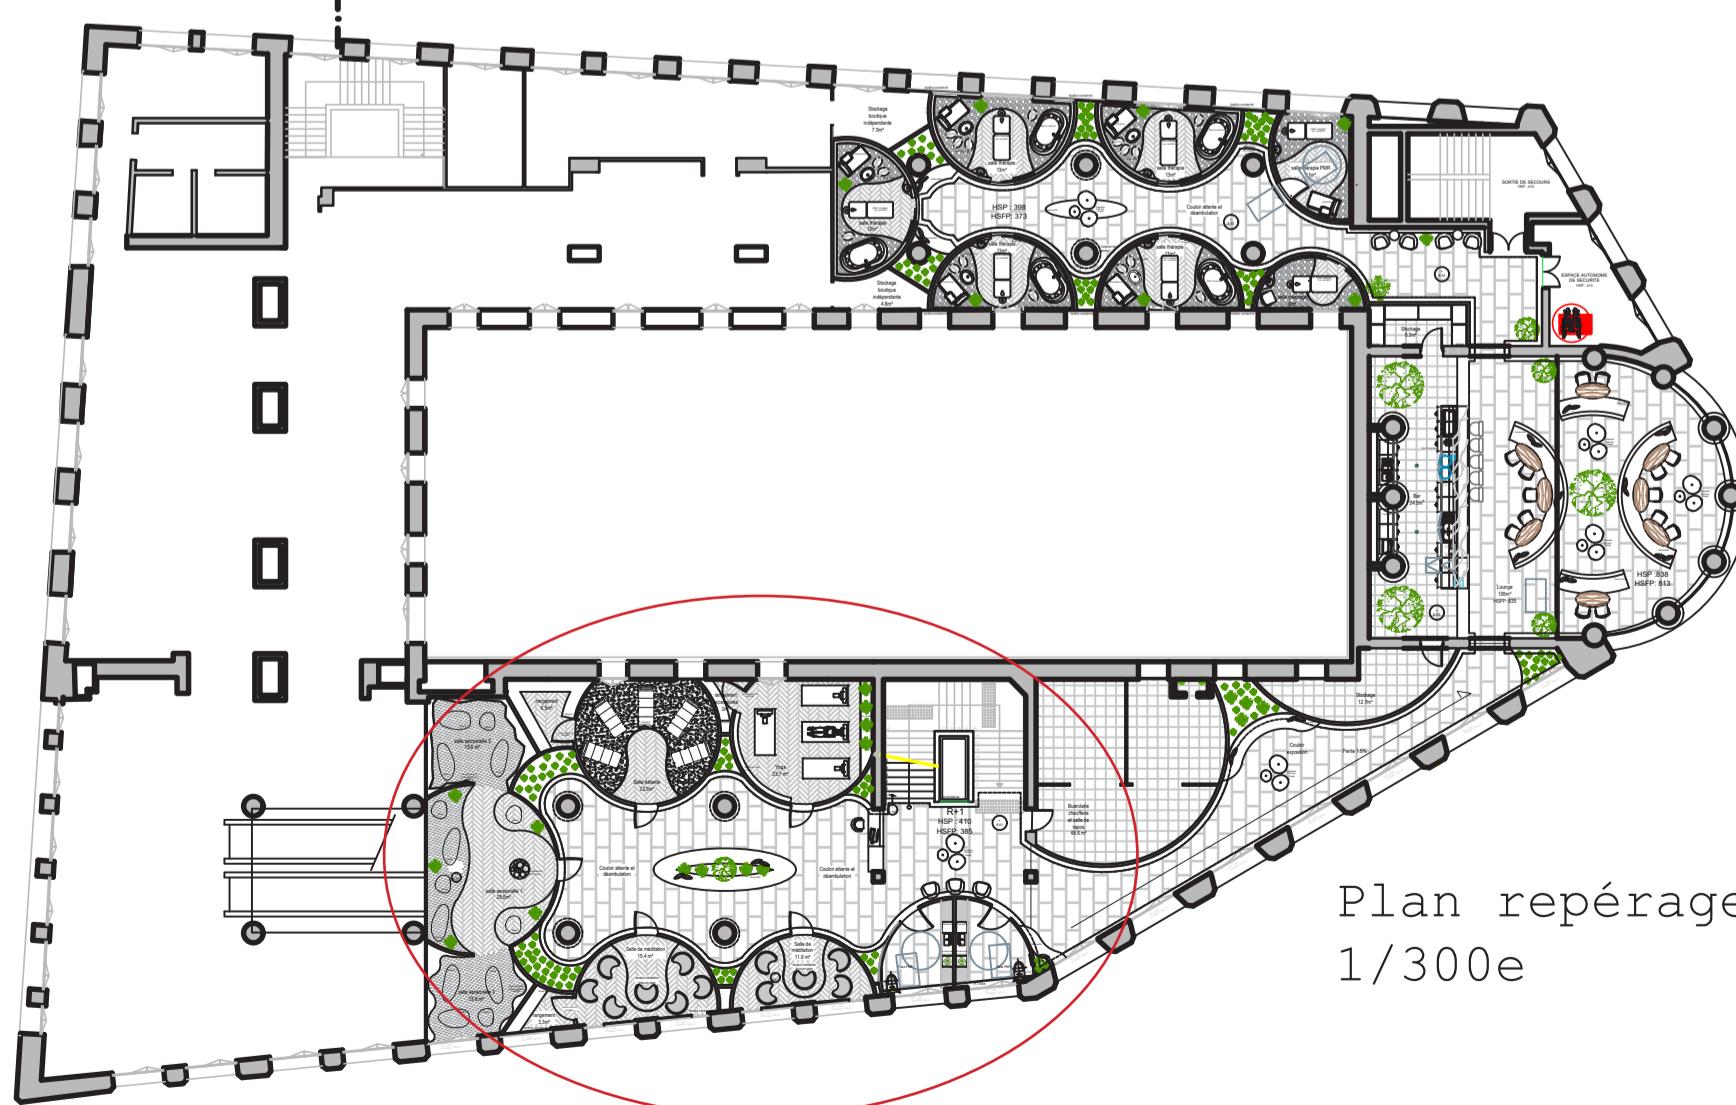

Plan repérage
1/300e

PLAN CLIMATISATION



1ER ÉTAGE

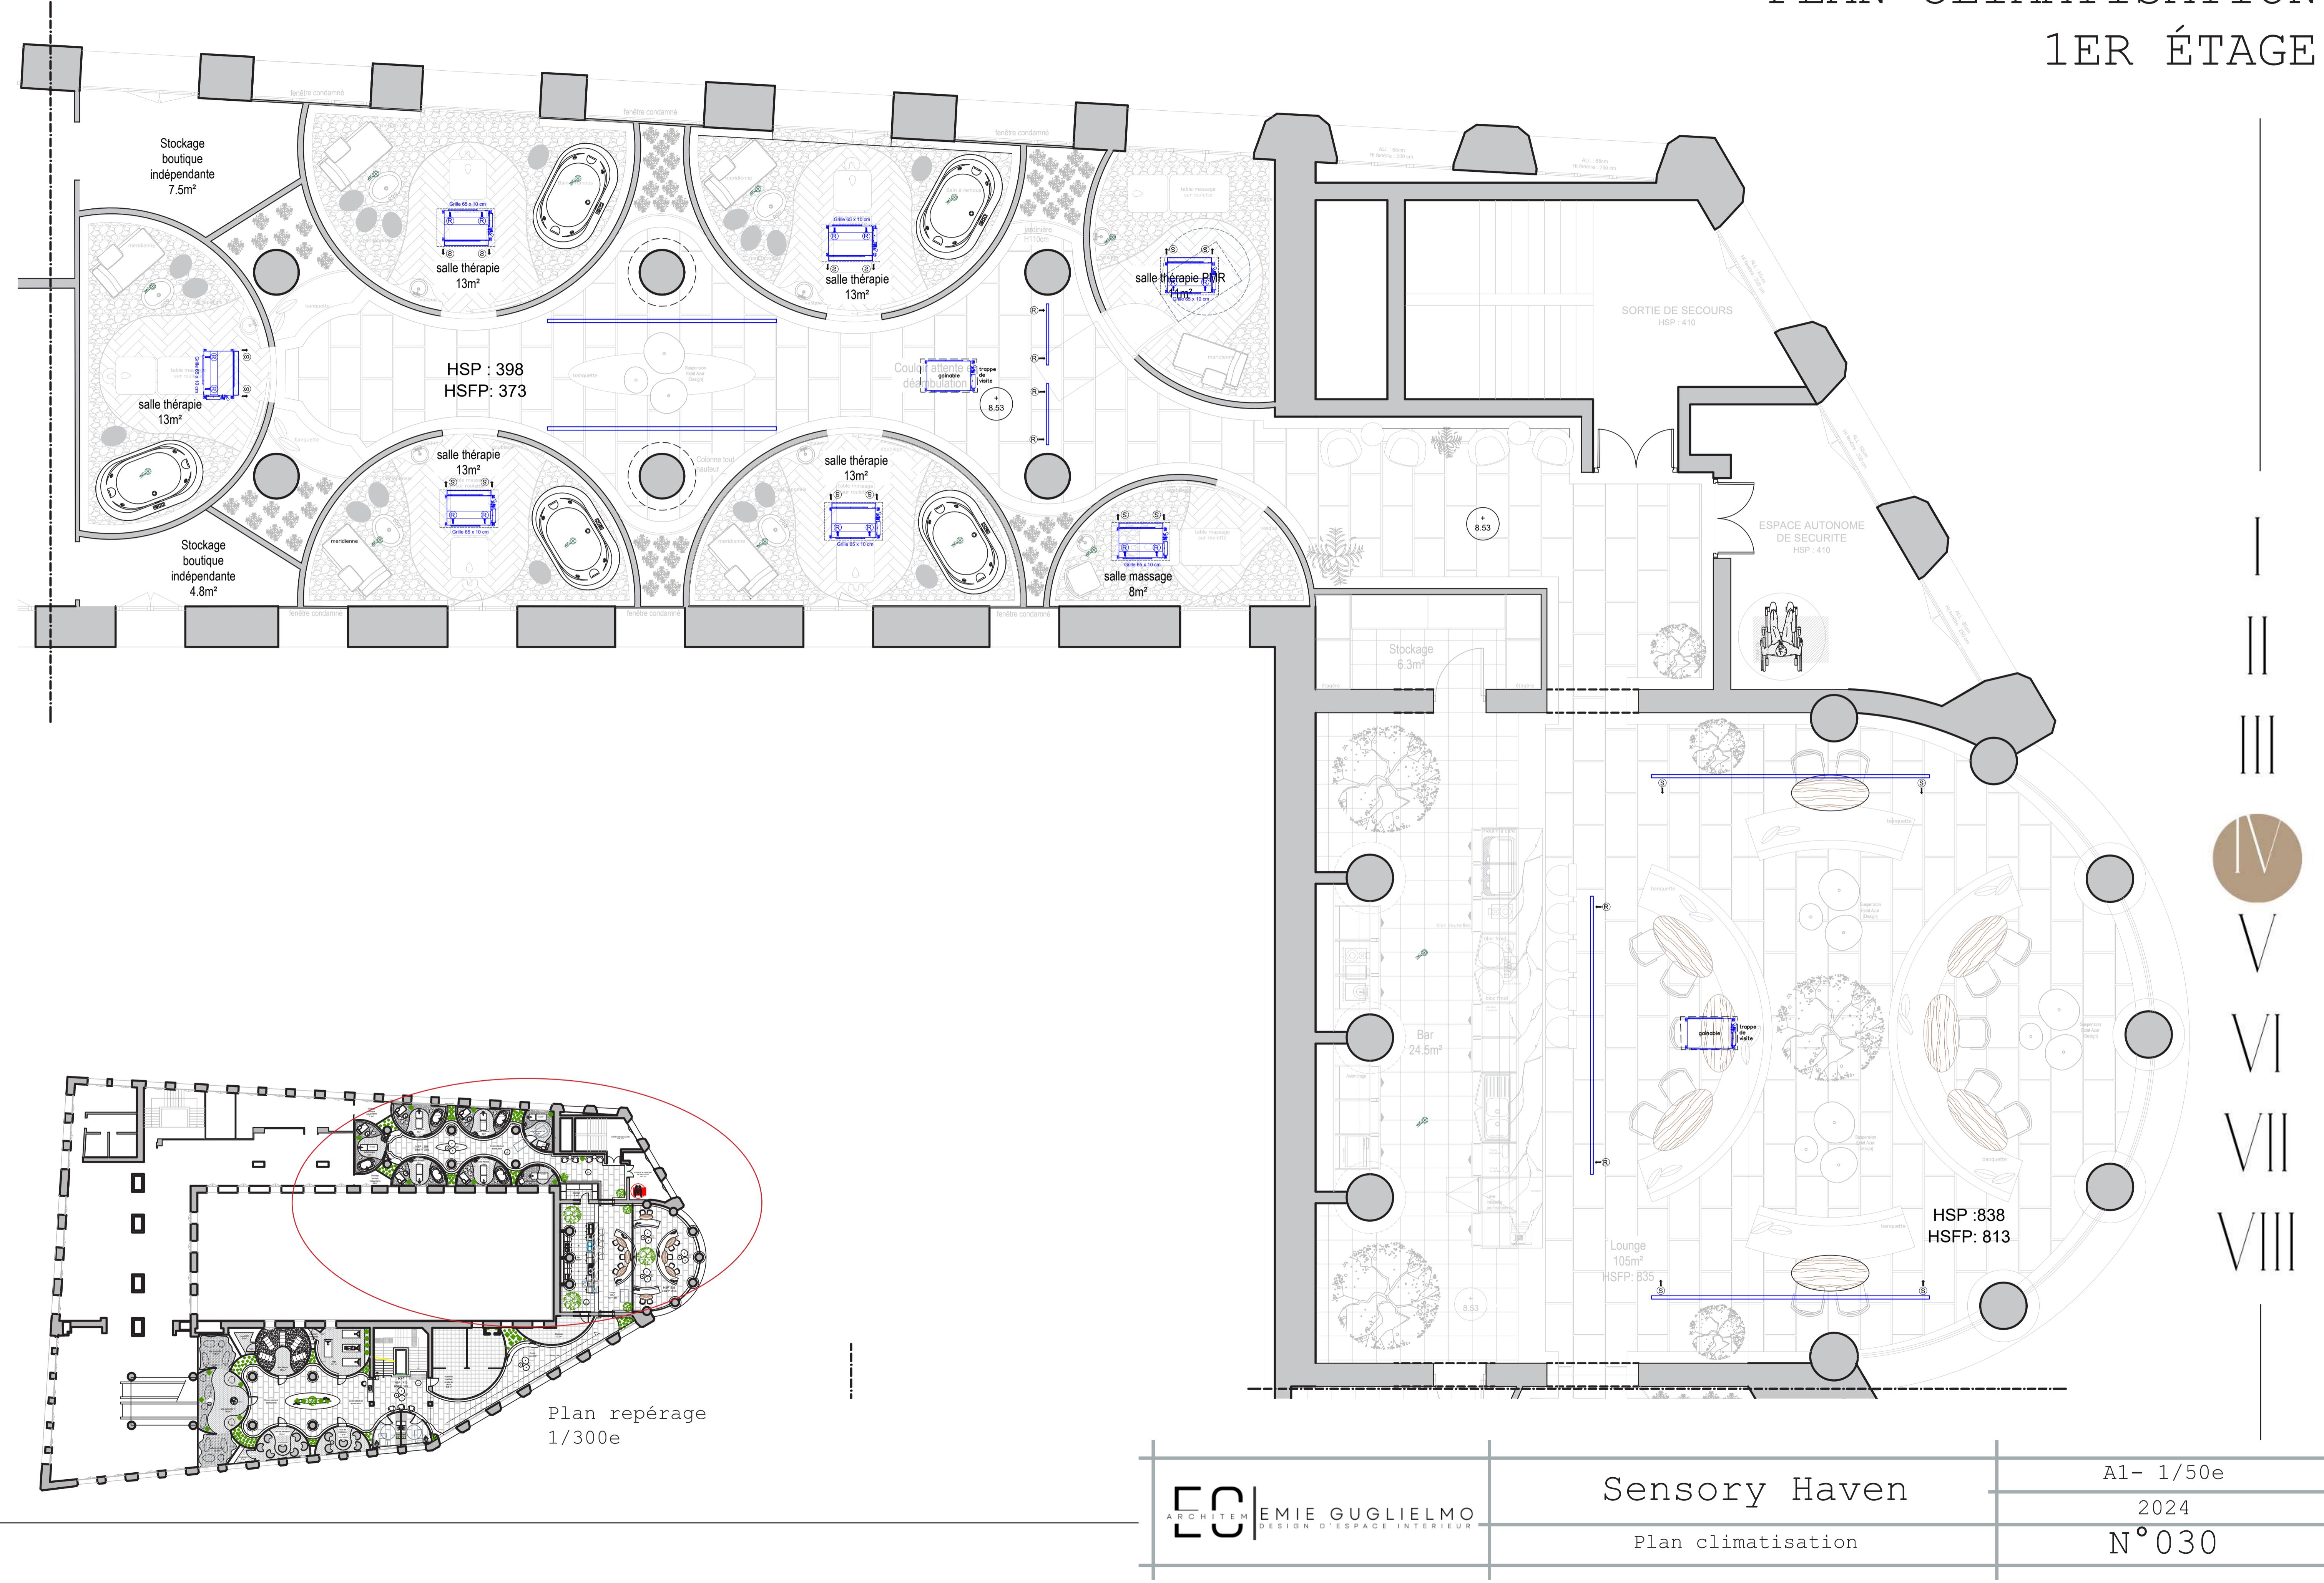

PLAN PLOMBERIE REZ - DE - CHAUSSÉE

La distribution de l'eau fonctionne de la manière suivante : l'eau arrive d'abord à la chaudière centrale, puis elle est redistribuée vers des nourrices principales par zone. Ensuite, ces nourrices principales acheminent l'eau aux nourrices secondaires, qui se chargent de distribuer l'eau là où elle est nécessaire.

Pour le système d'évacuation des eaux usées et des eaux vannes, celles-ci sont acheminées vers un regard collectif, lequel est connecté au collecteur public. Cela assure une gestion centralisée et efficace des eaux usées.

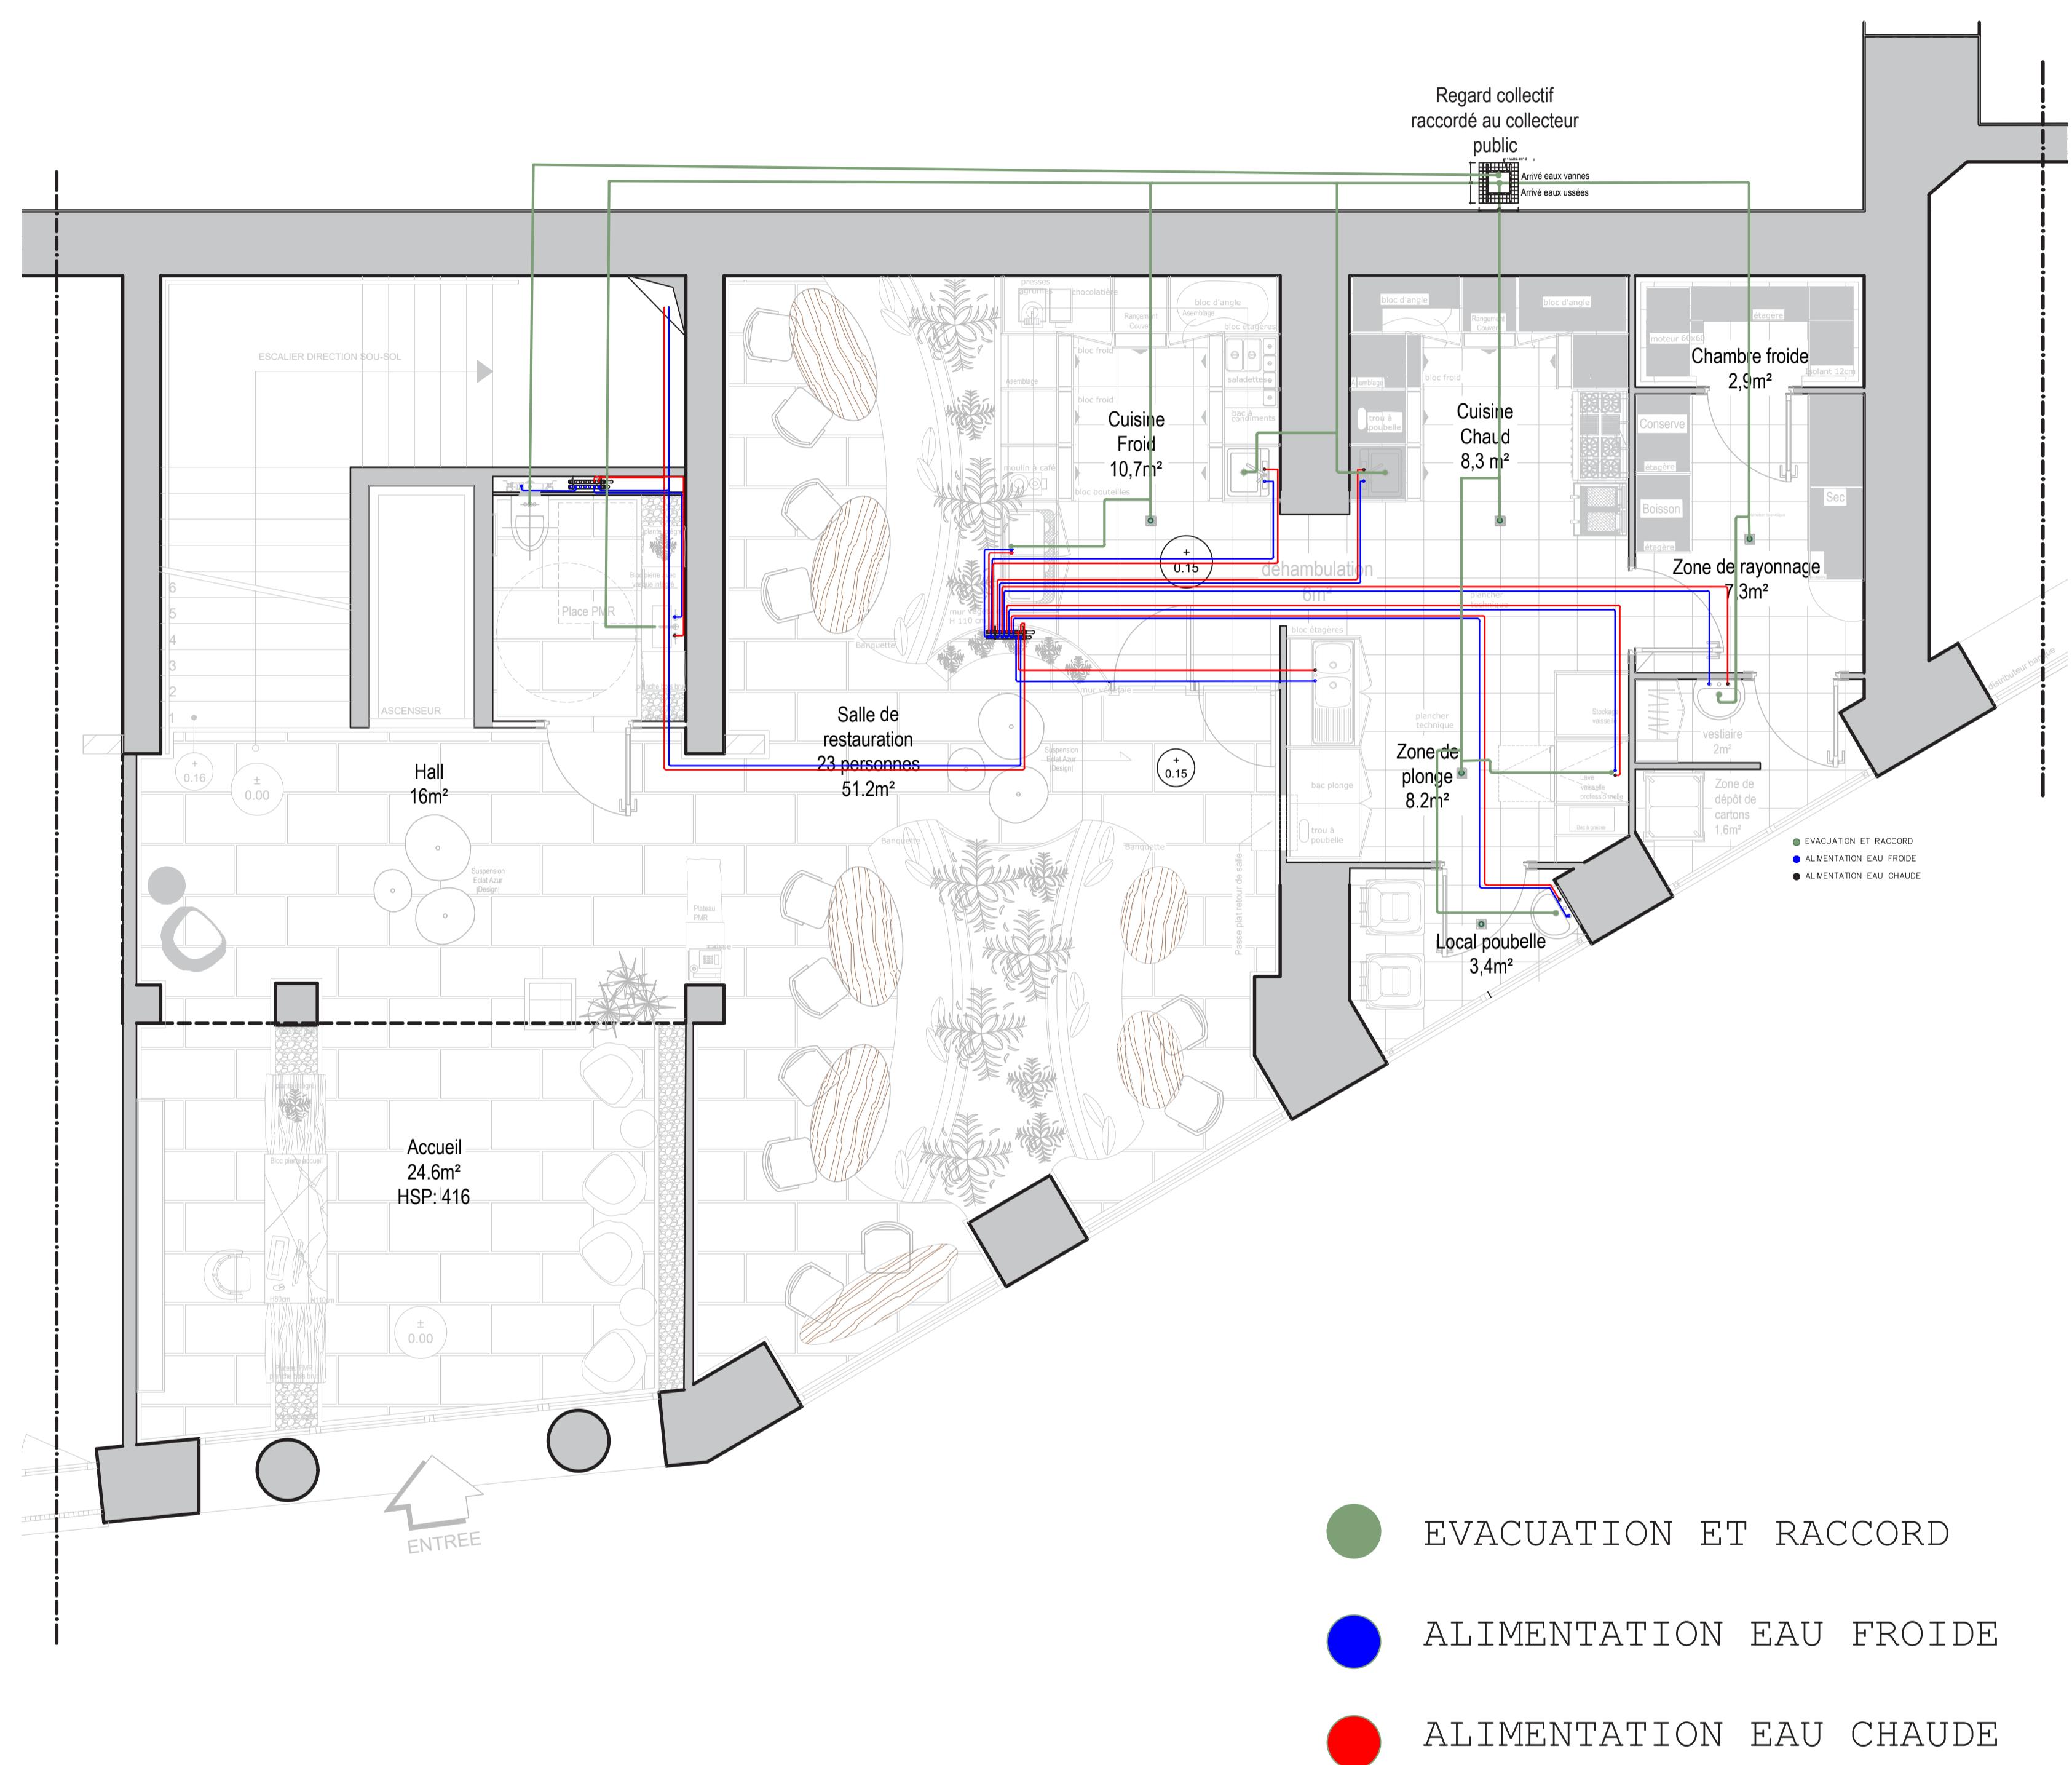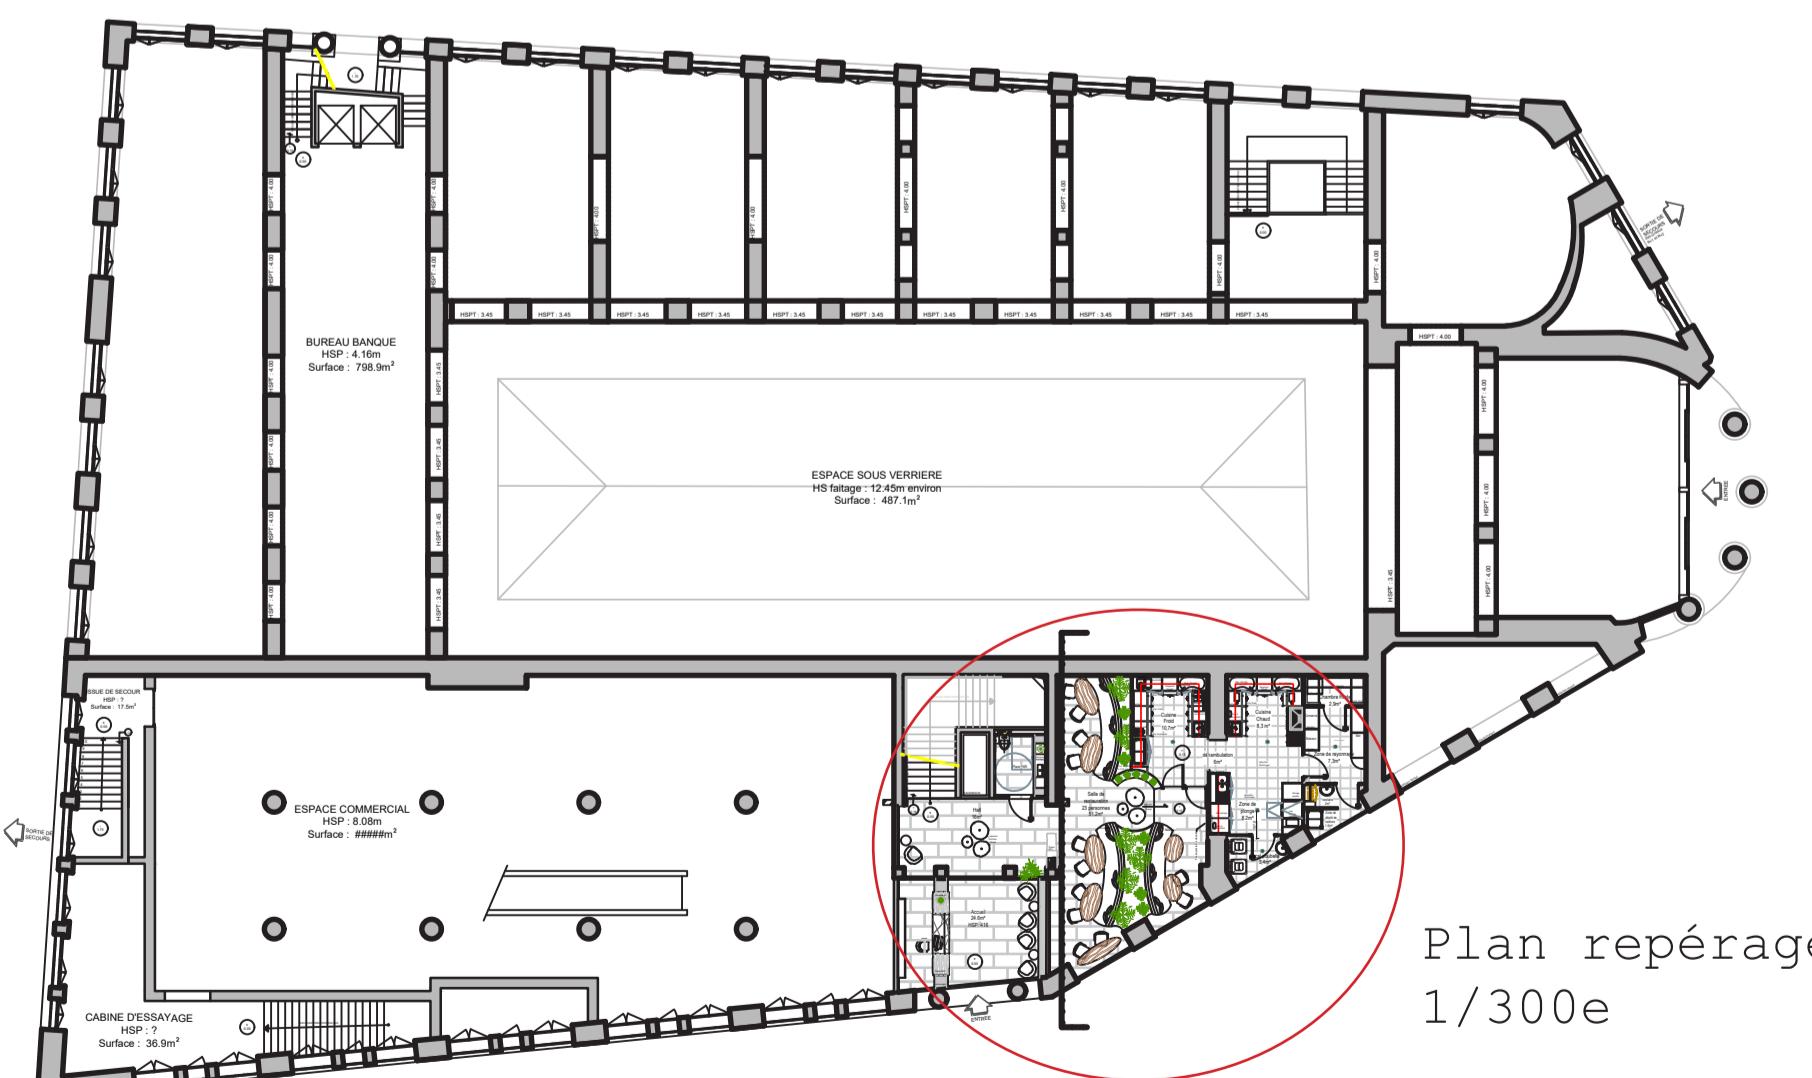

IV


V

VI

VII

VIII

PLOMBERIE
1ER ÉTAGE

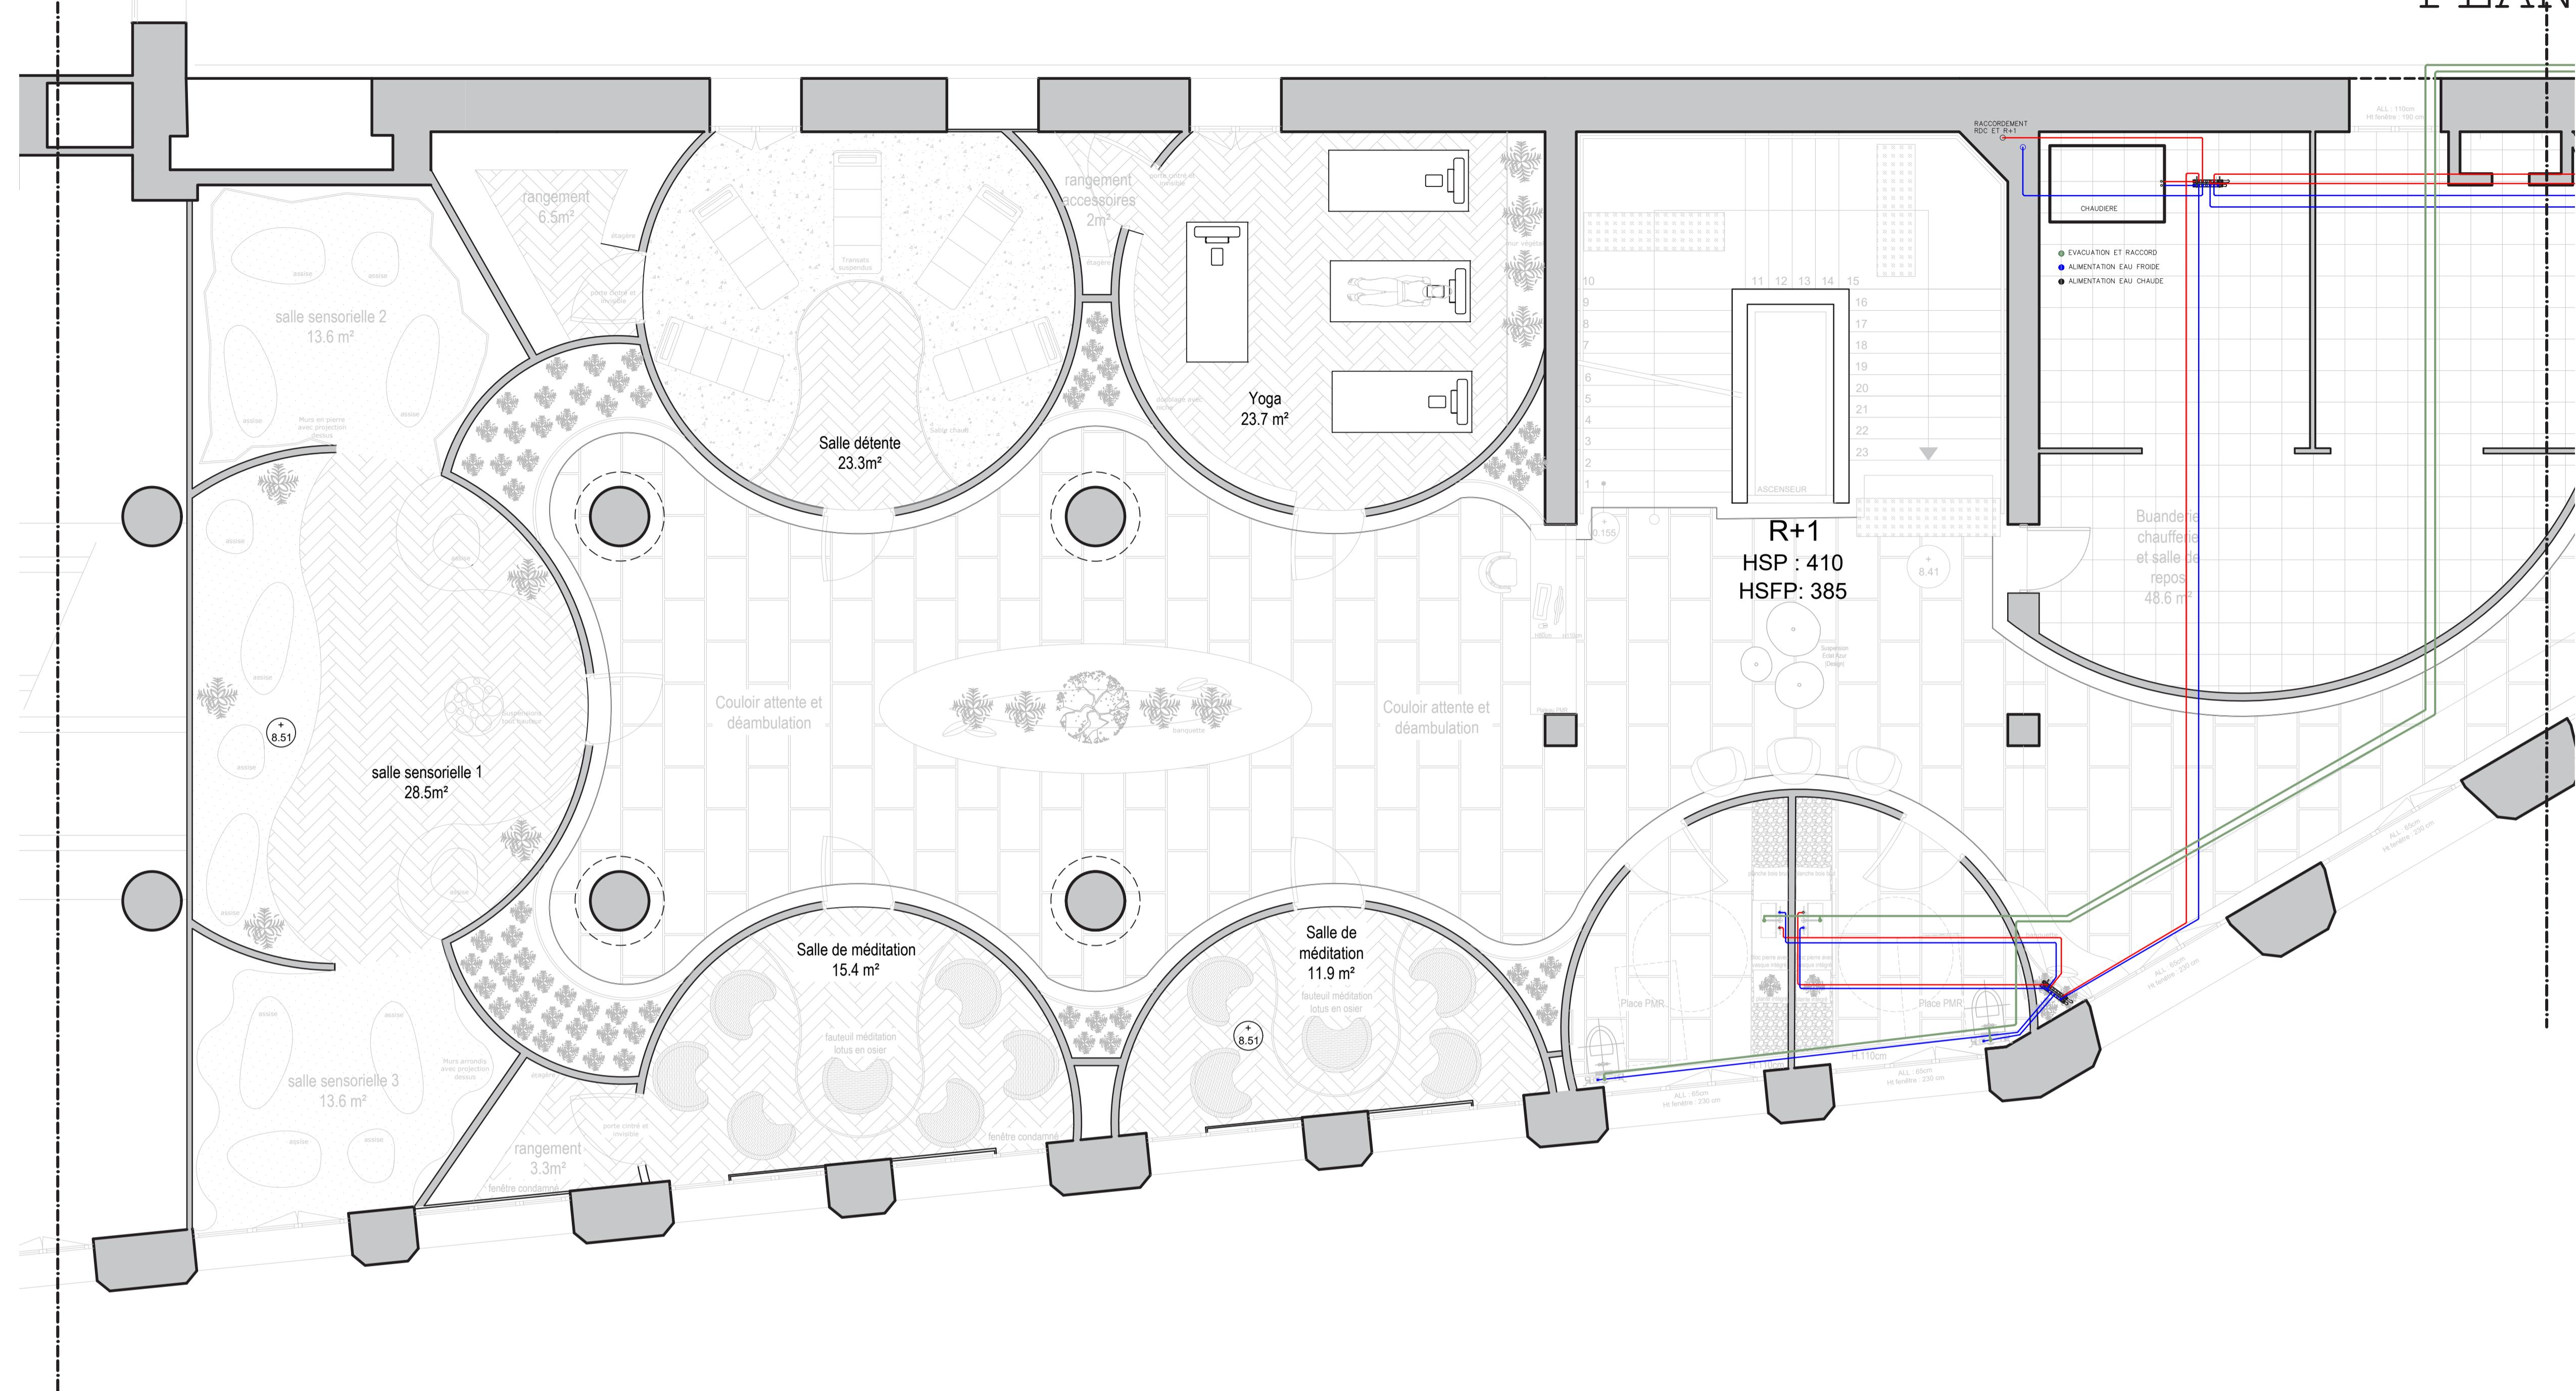


IV

V

VI

VII


VIII

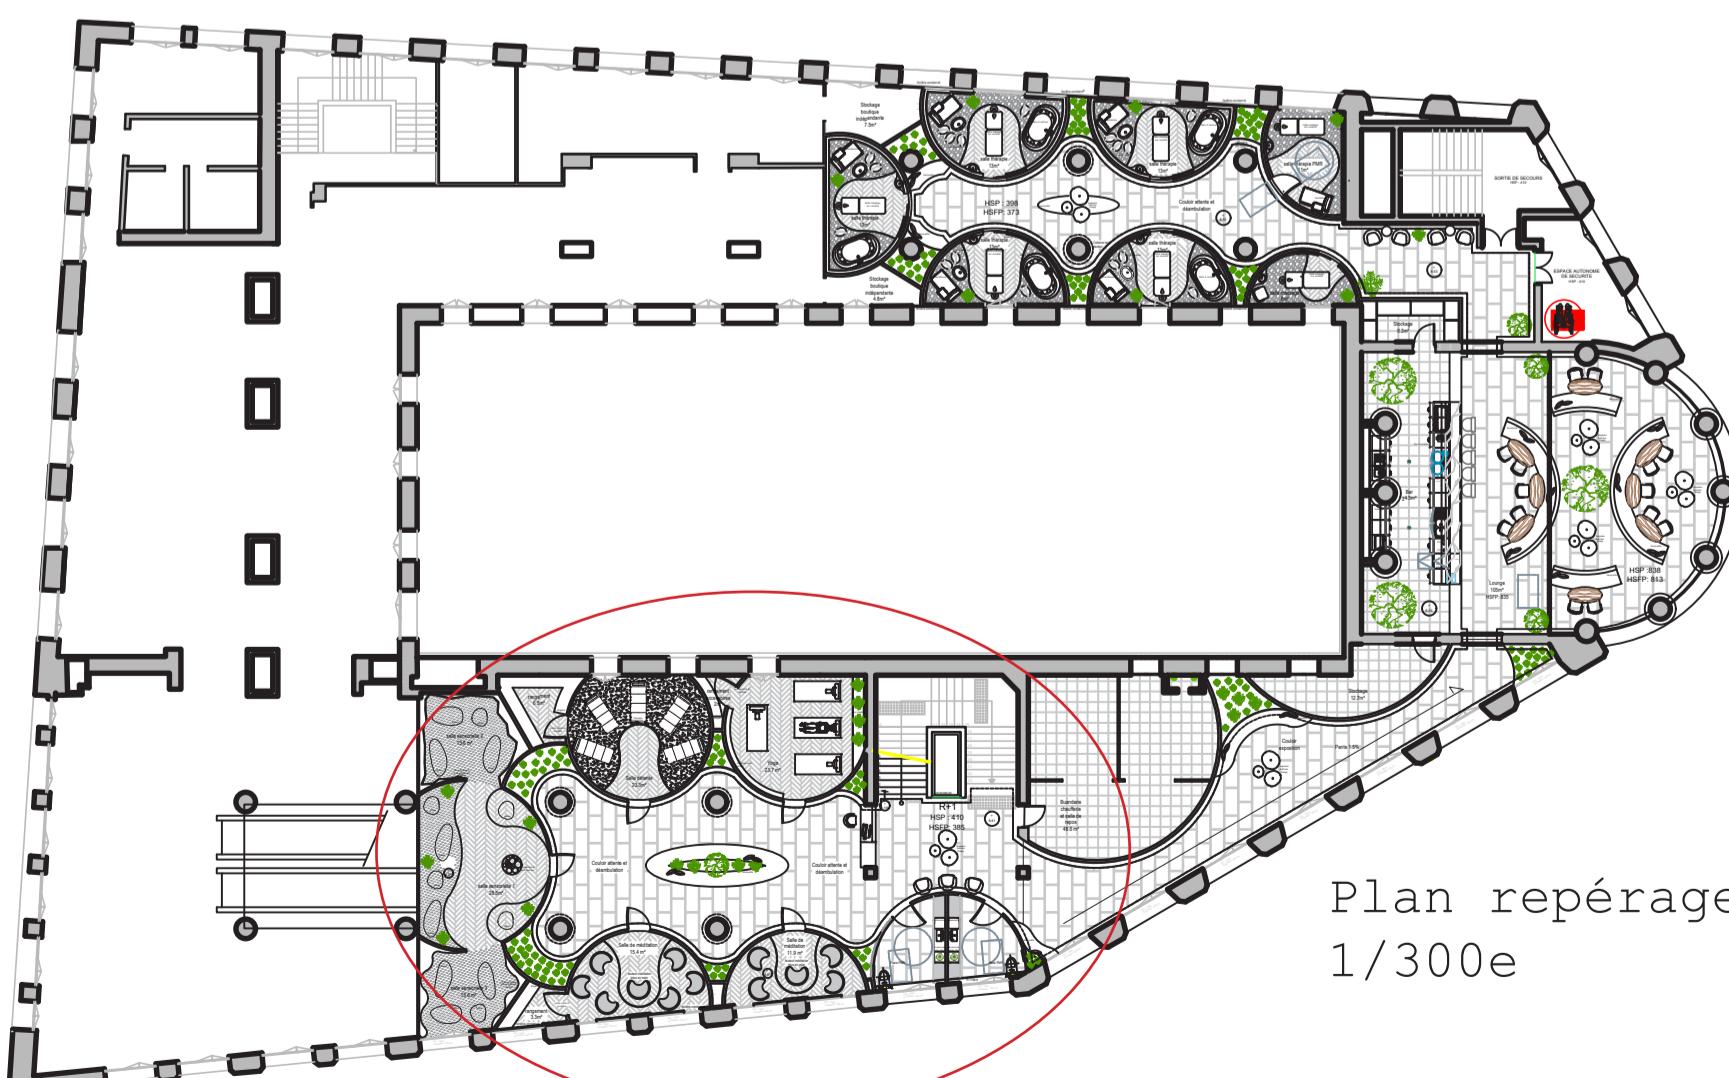


- EVACUATION ET RACCORD
- ALIMENTATION EAU FROIDE
- ALIMENTATION EAU CHAUX

PLAN PLOMBERIE


1ER ÉTAGE

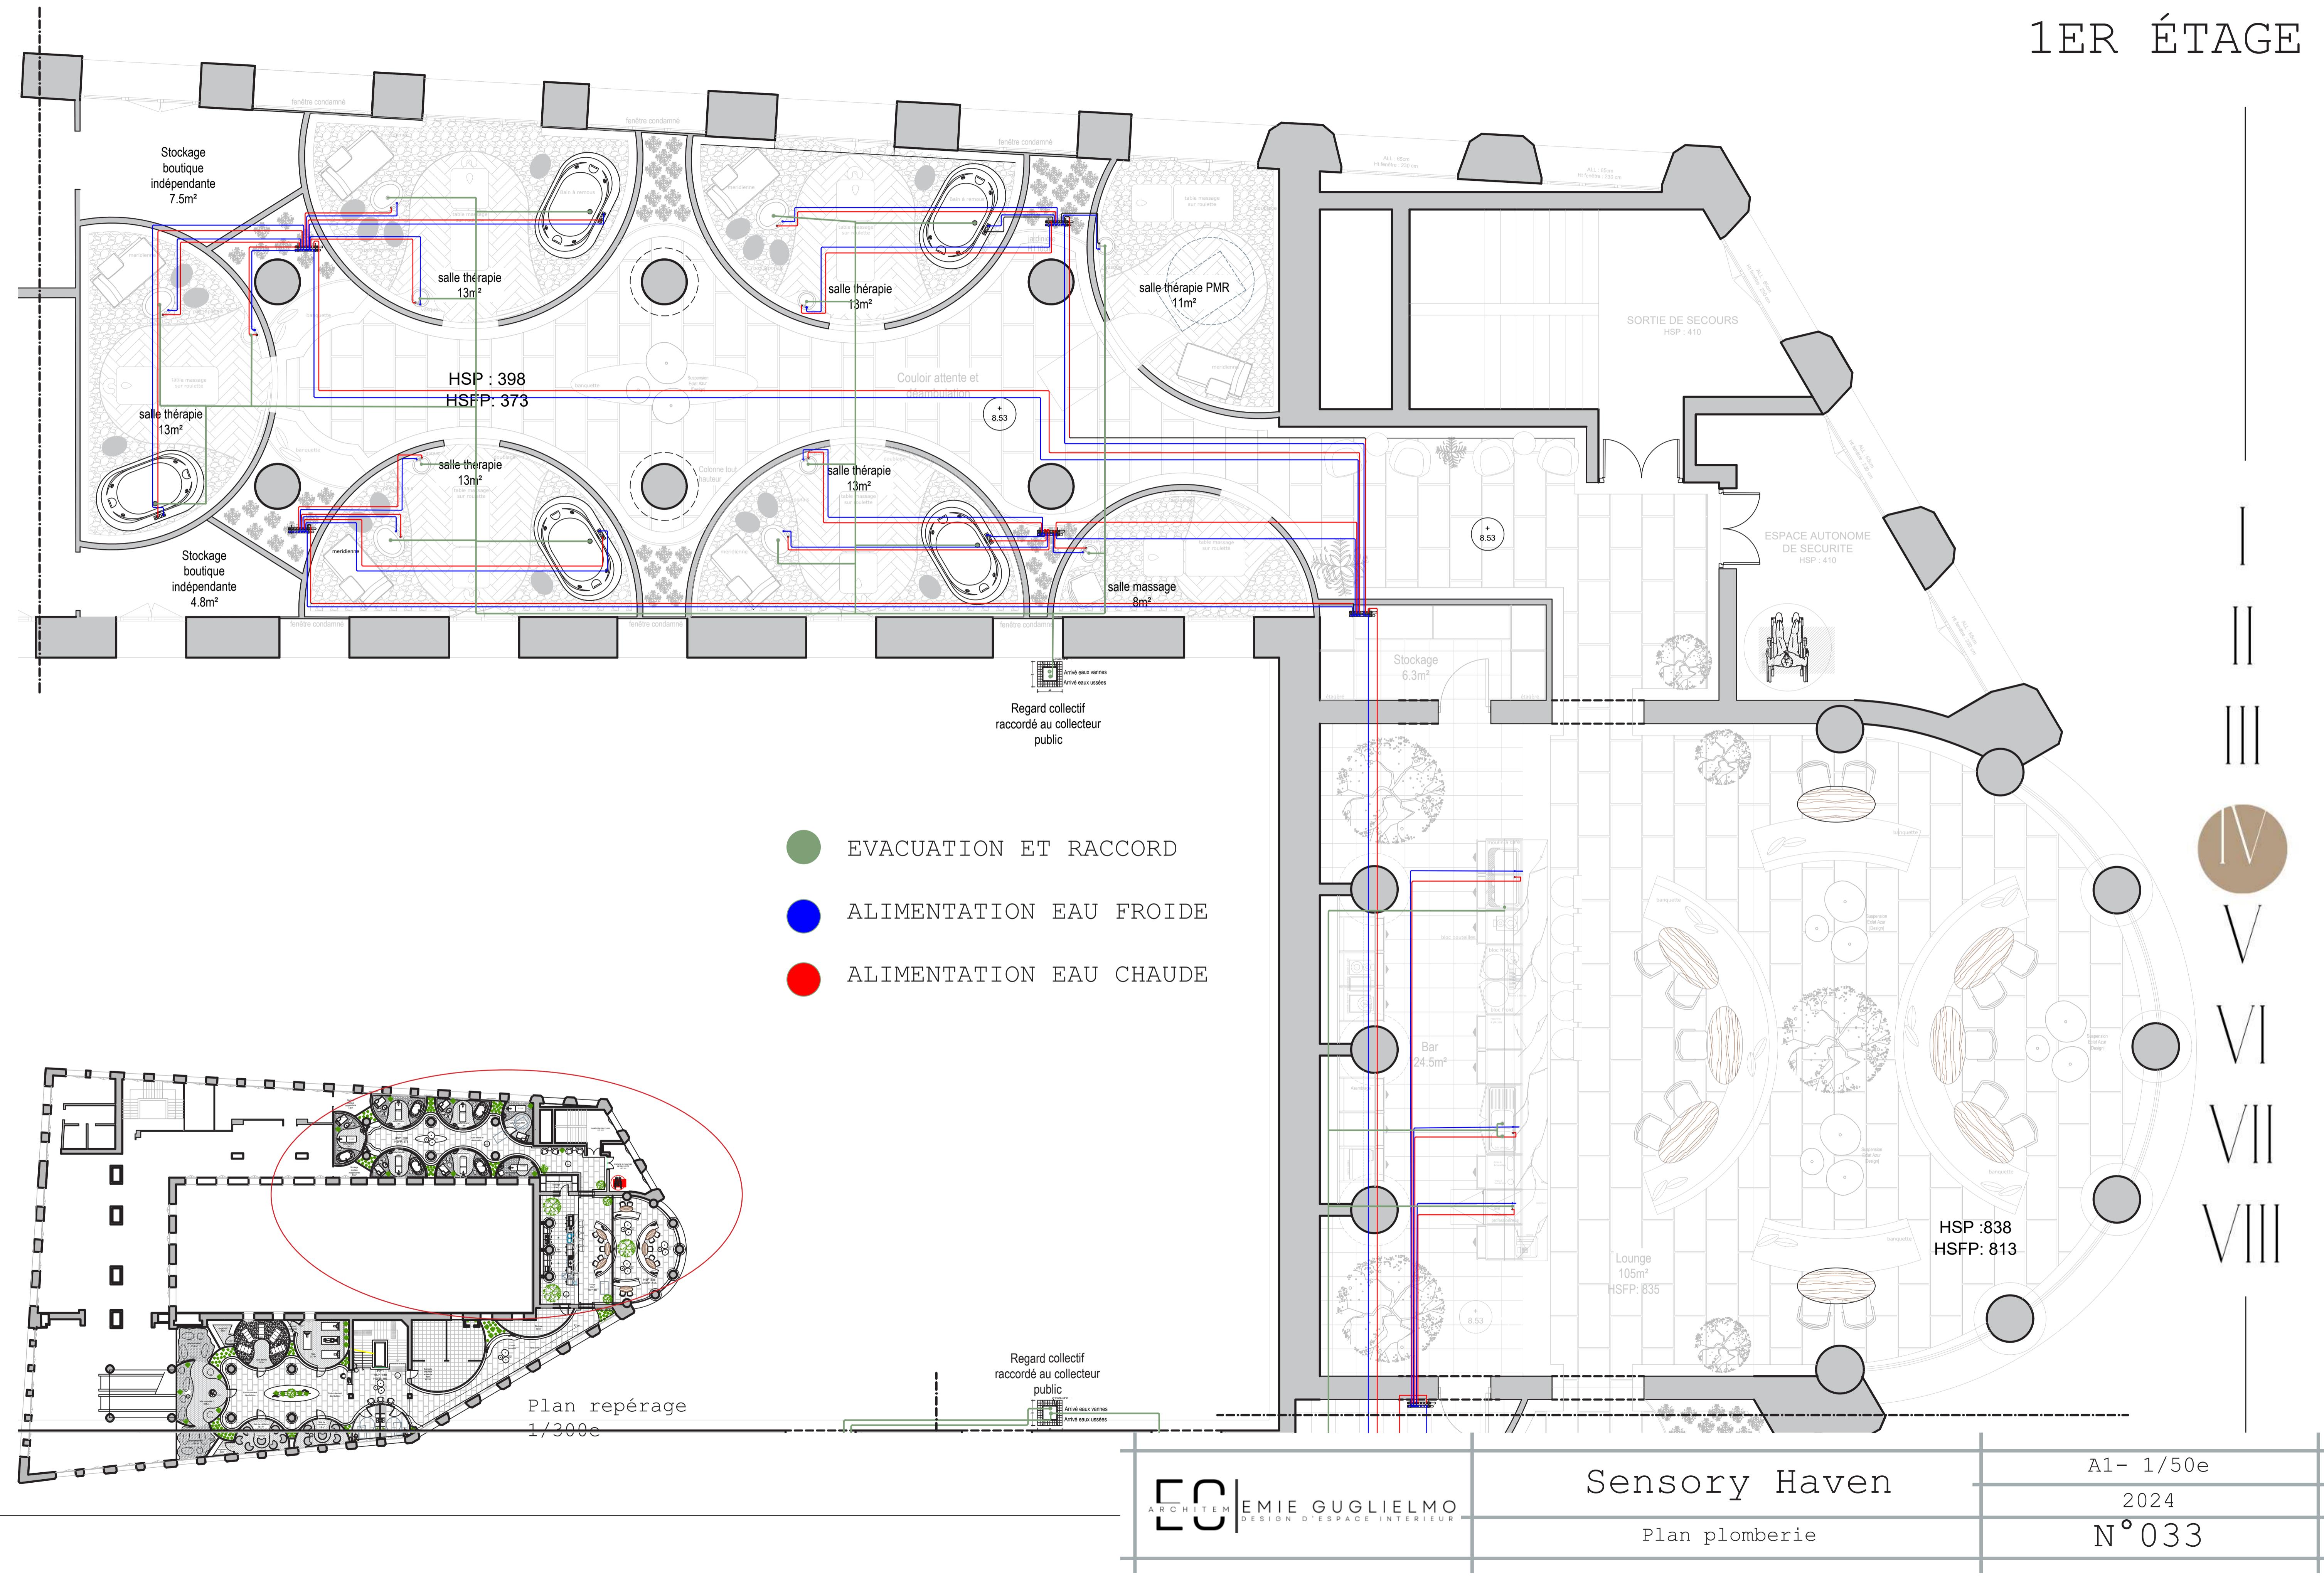


PLAN CIRCULATION REZ - DE - CHAUSSÉE

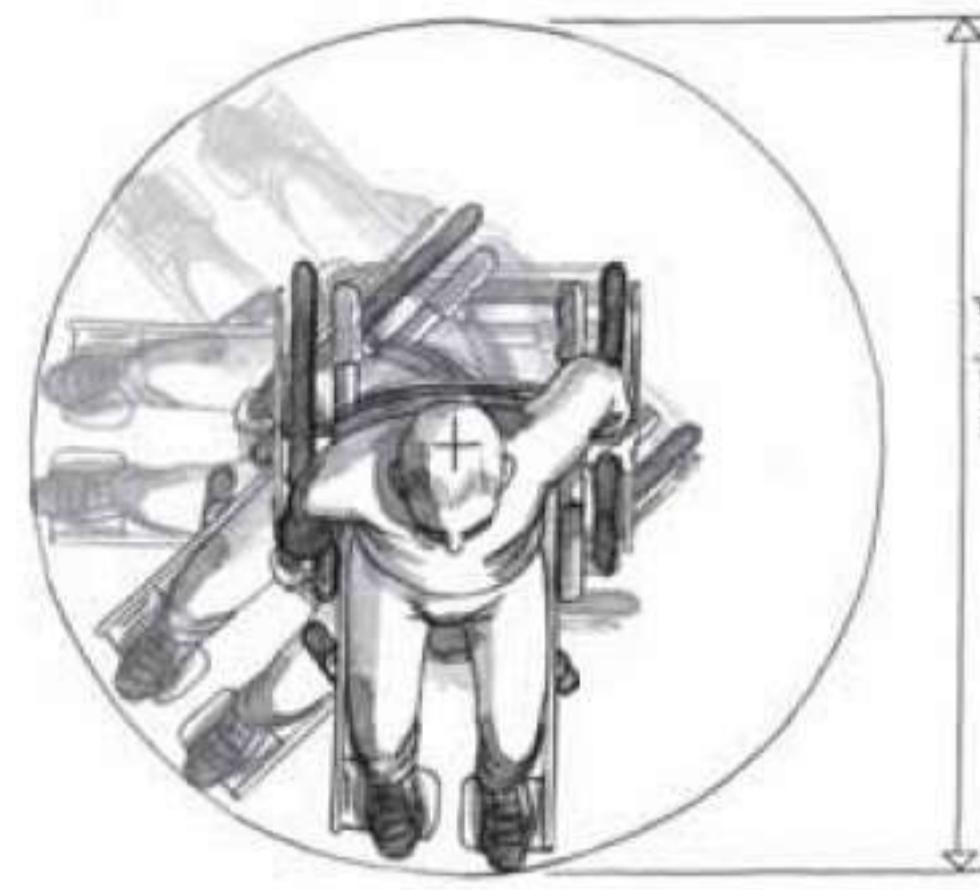


L'accessibilité pour les personnes à mobilité réduite (PMR) est fluide, leur permettant de se déplacer aisément et de profiter de tous les services proposés par notre espace. Des aires de retournement d'un diamètre minimum de 150 cm sont situées à divers endroits. Ces espaces circulaires sont positionnés sur un plan horizontal, sans pente ni dévers. Elles sont prévues en chaque point des cheminement intérieurs et extérieurs où un choix d'itinéraire est proposé, notamment à chaque intersection de couloirs ou d'allées, ainsi qu'à proximité des portes et des ascenseurs. De plus, des aires de retournement sont installées tous les 6 mètres au minimum.

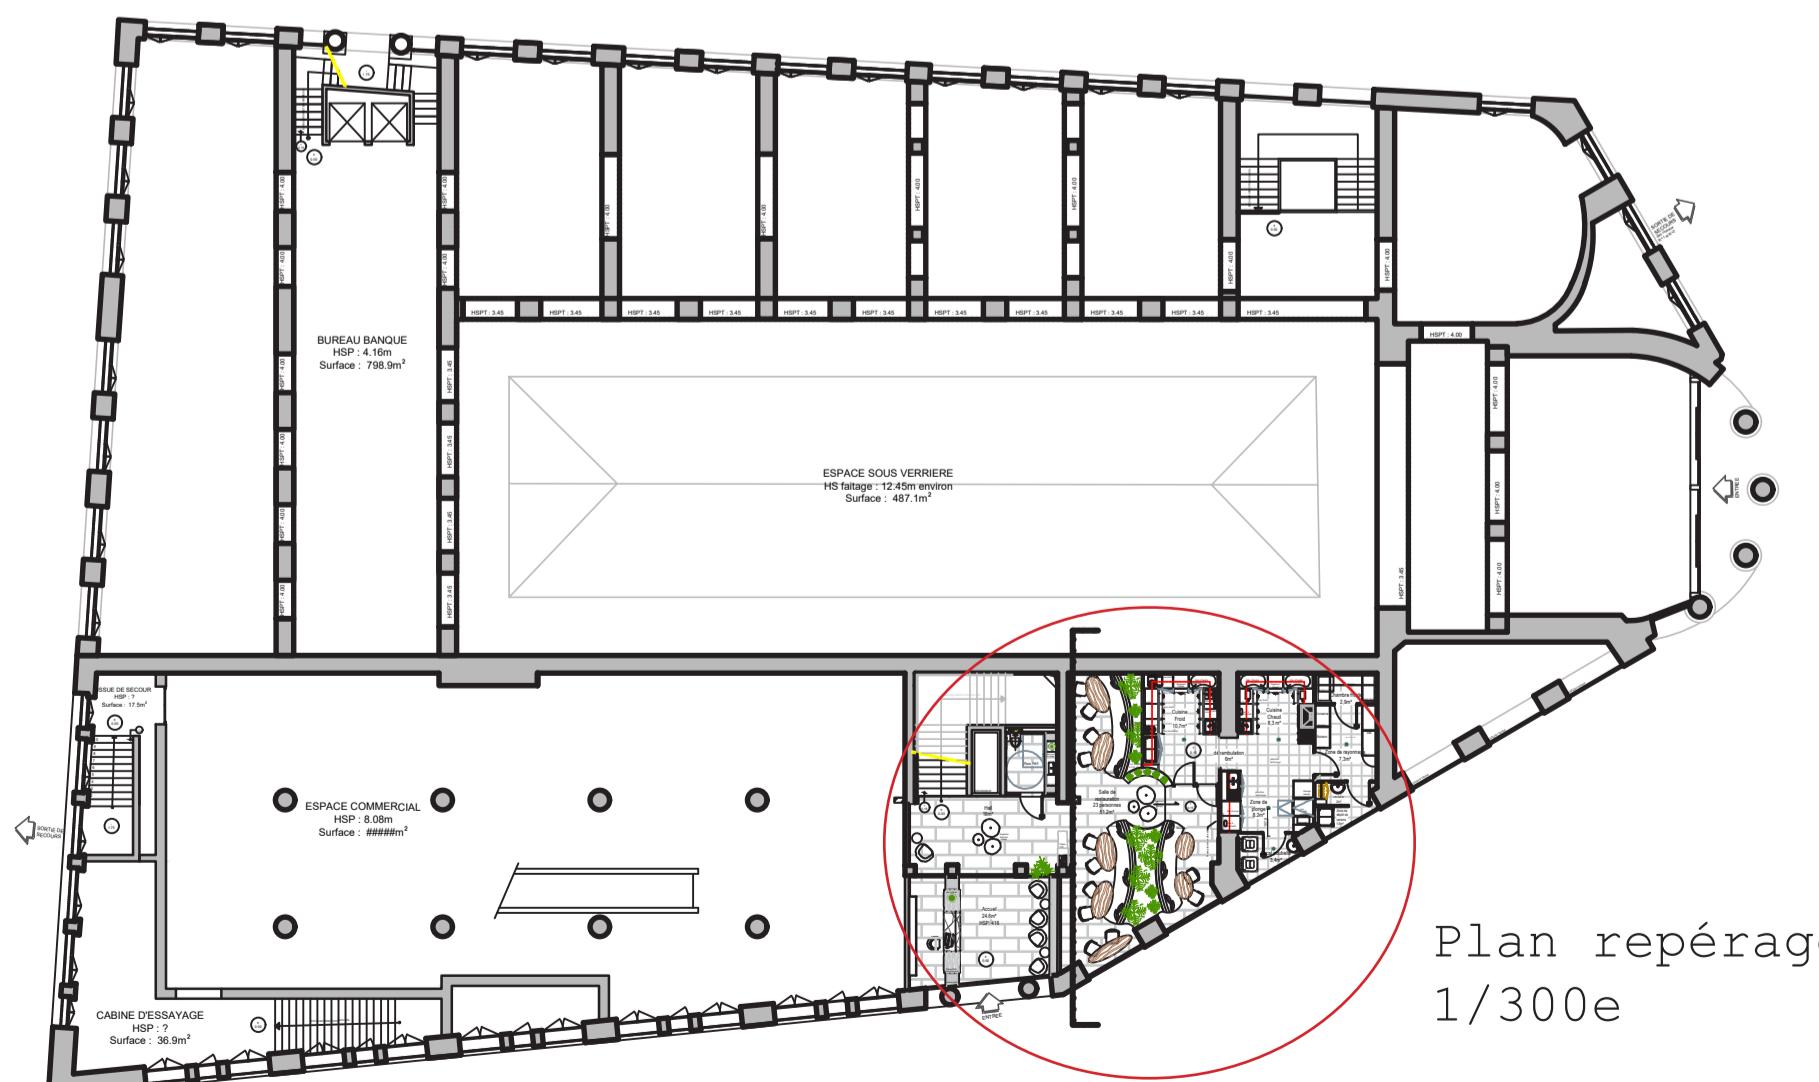

Plan repérage
1/300e

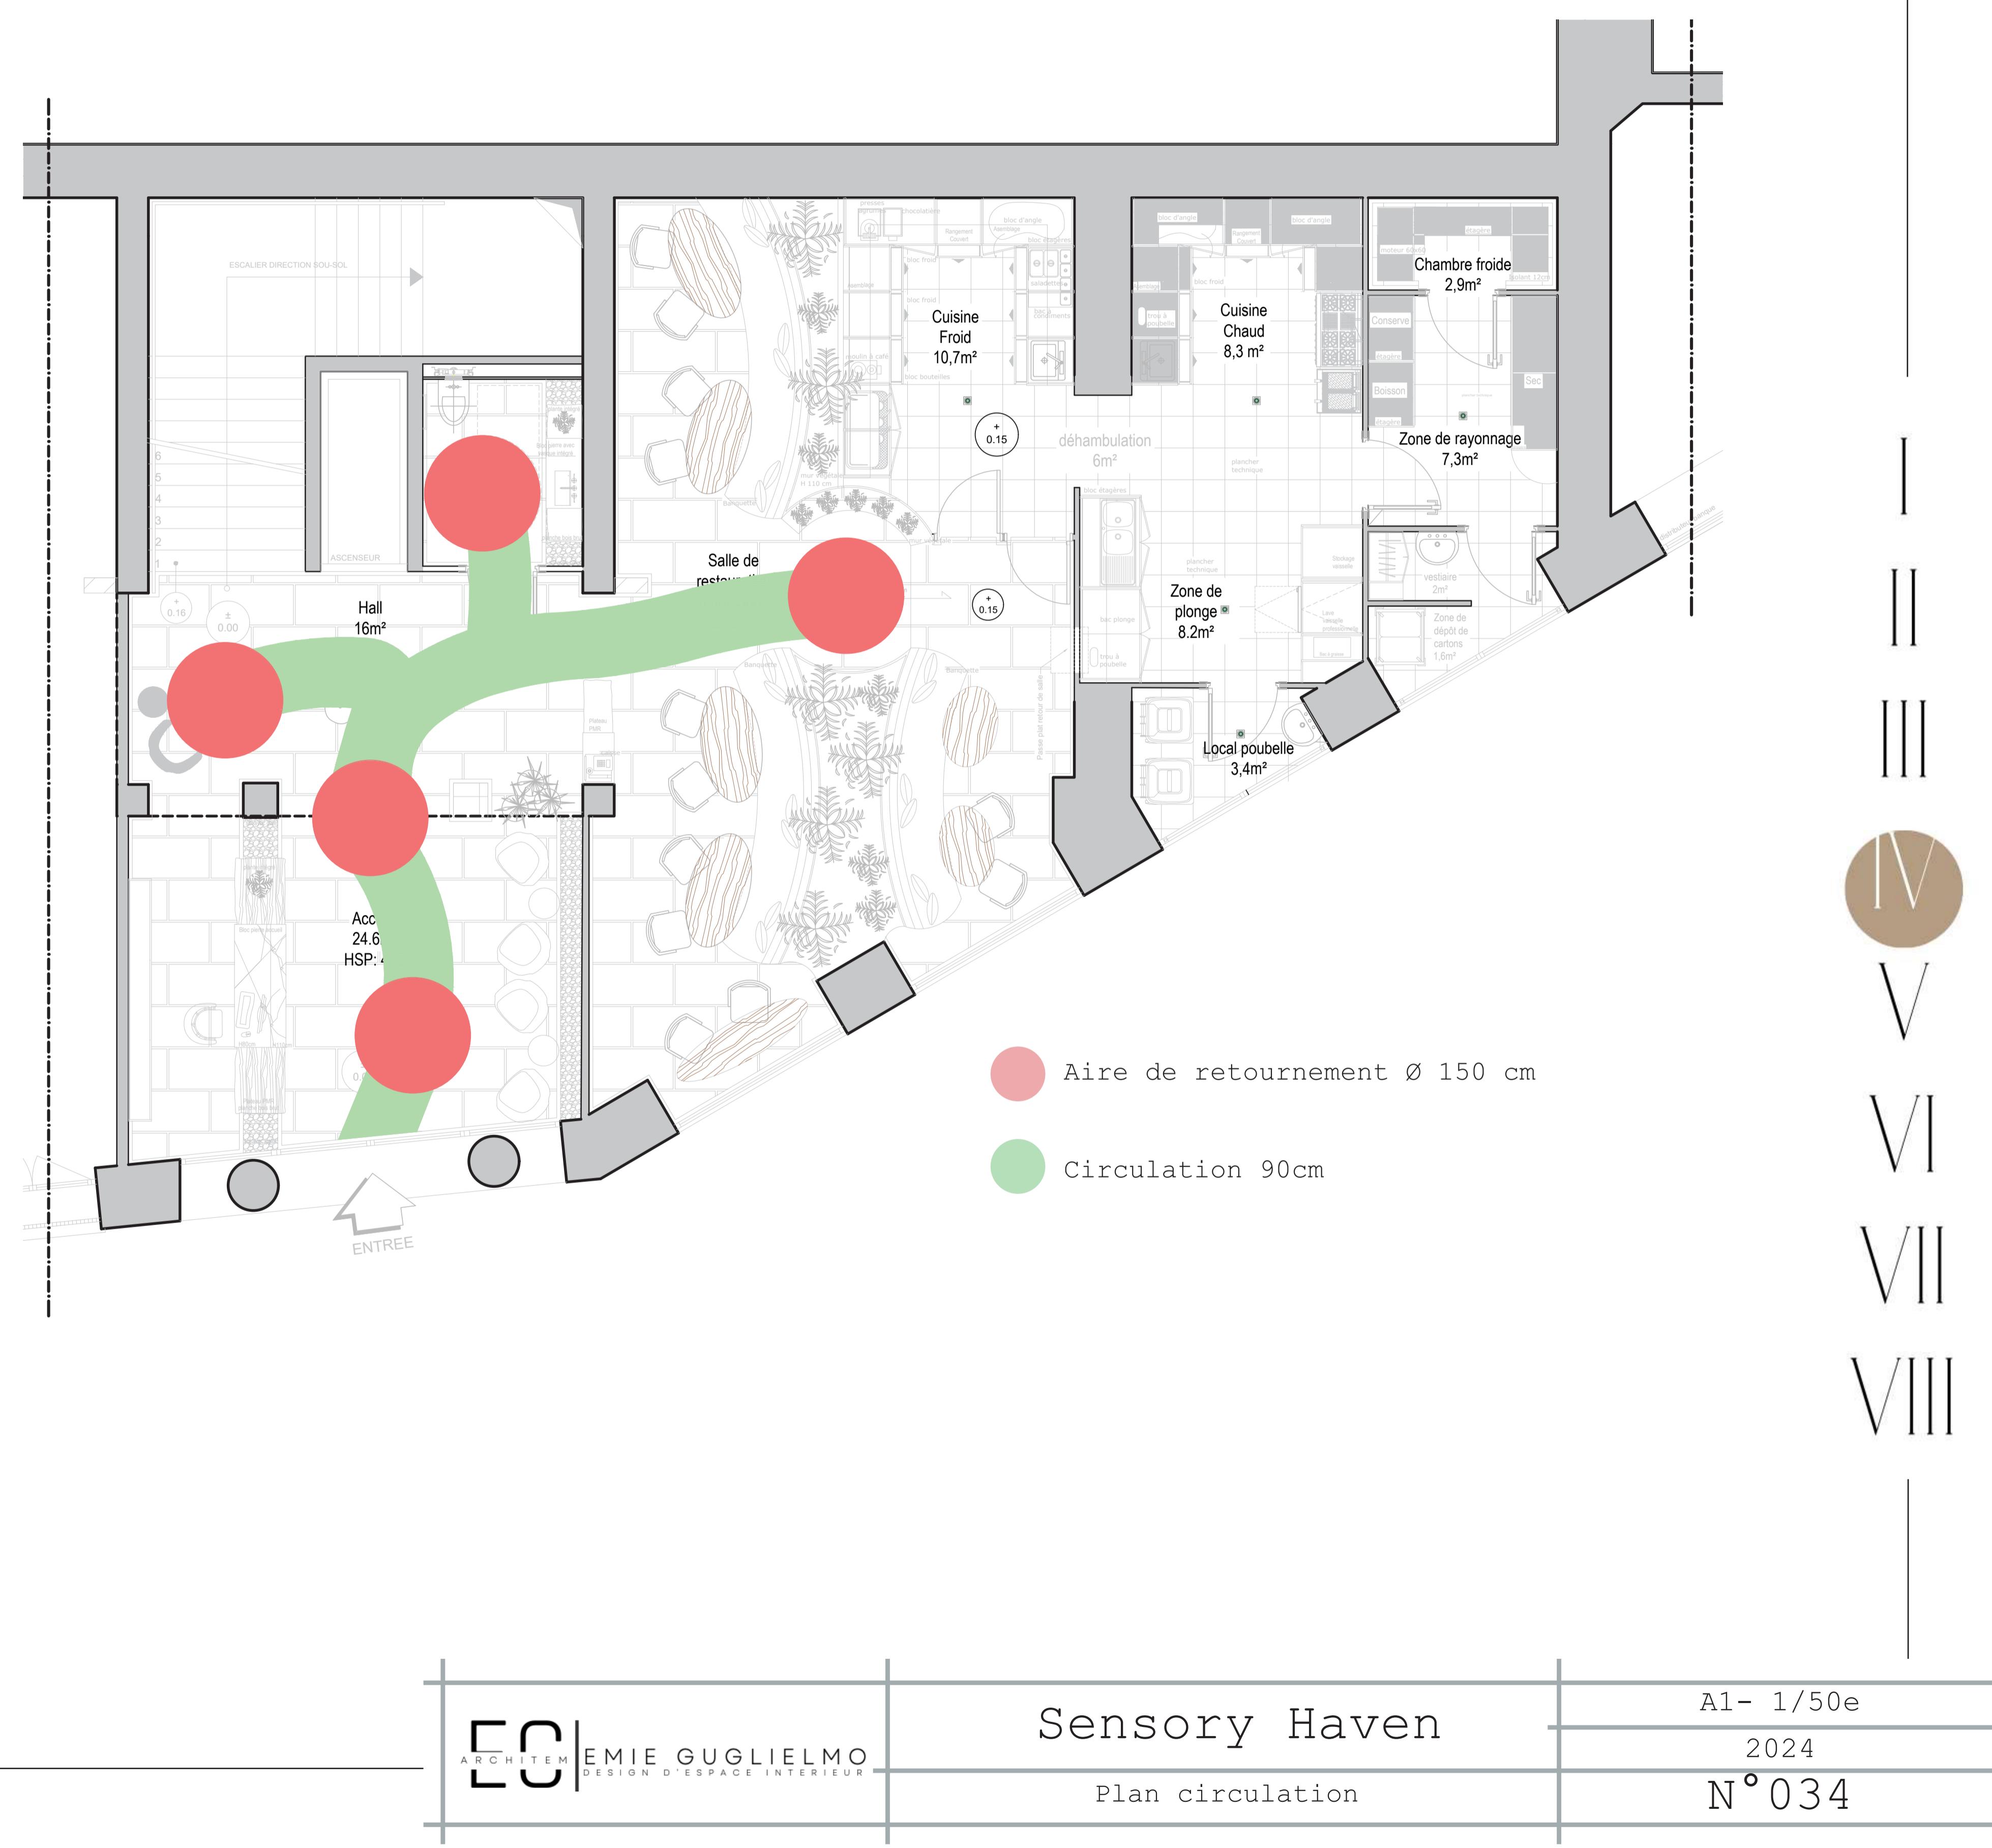

PLAN CIRCULATION
1ER ÉTAGE

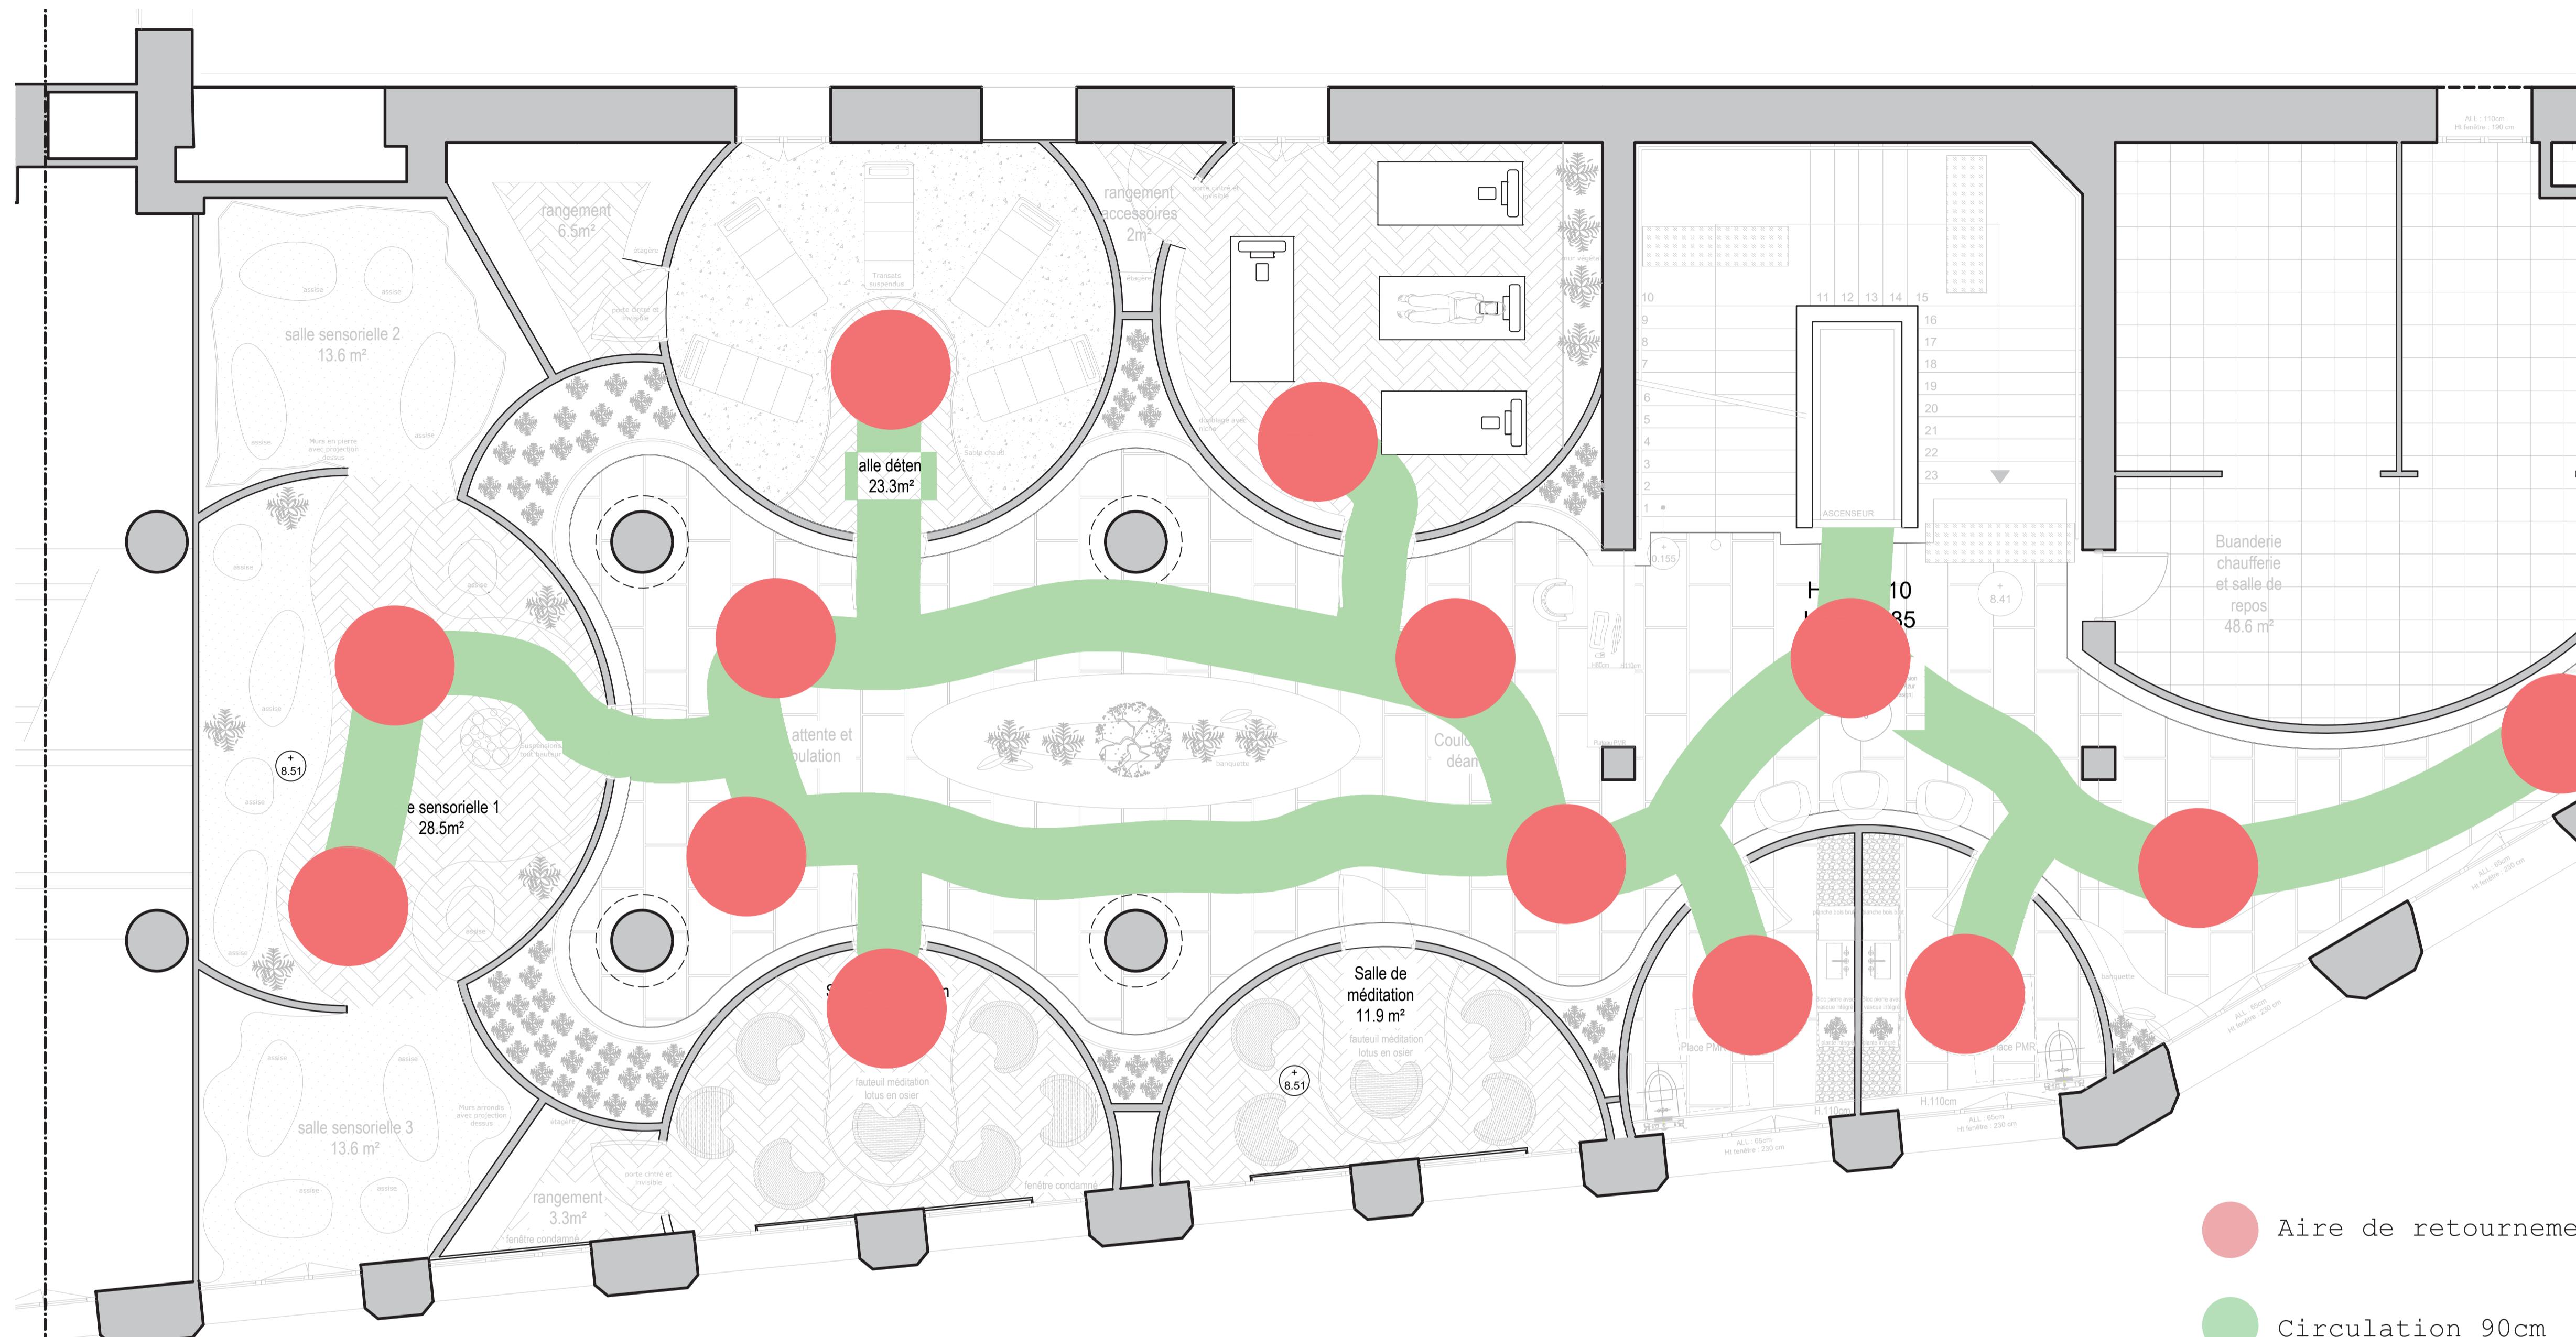


IV

V

VI

VII


VIII

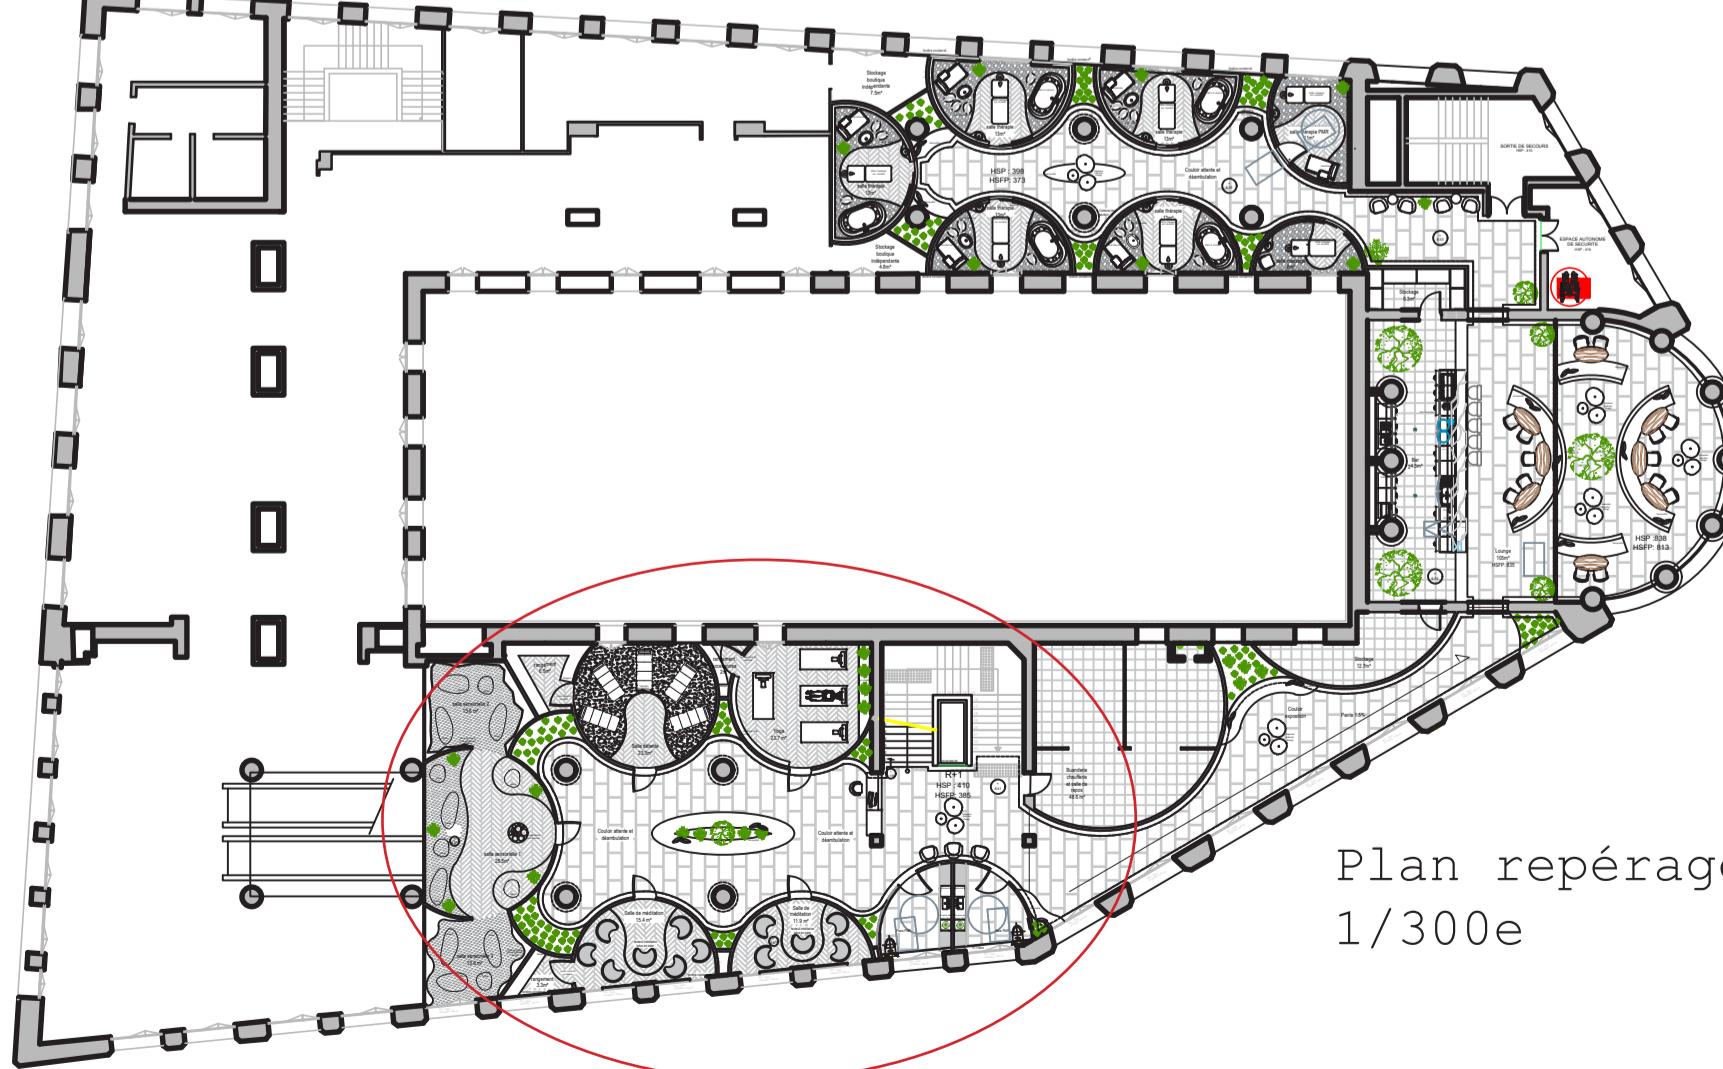






Plan repérage
1/300e

PLAN CIRCULATION

1ER ÉTAGE

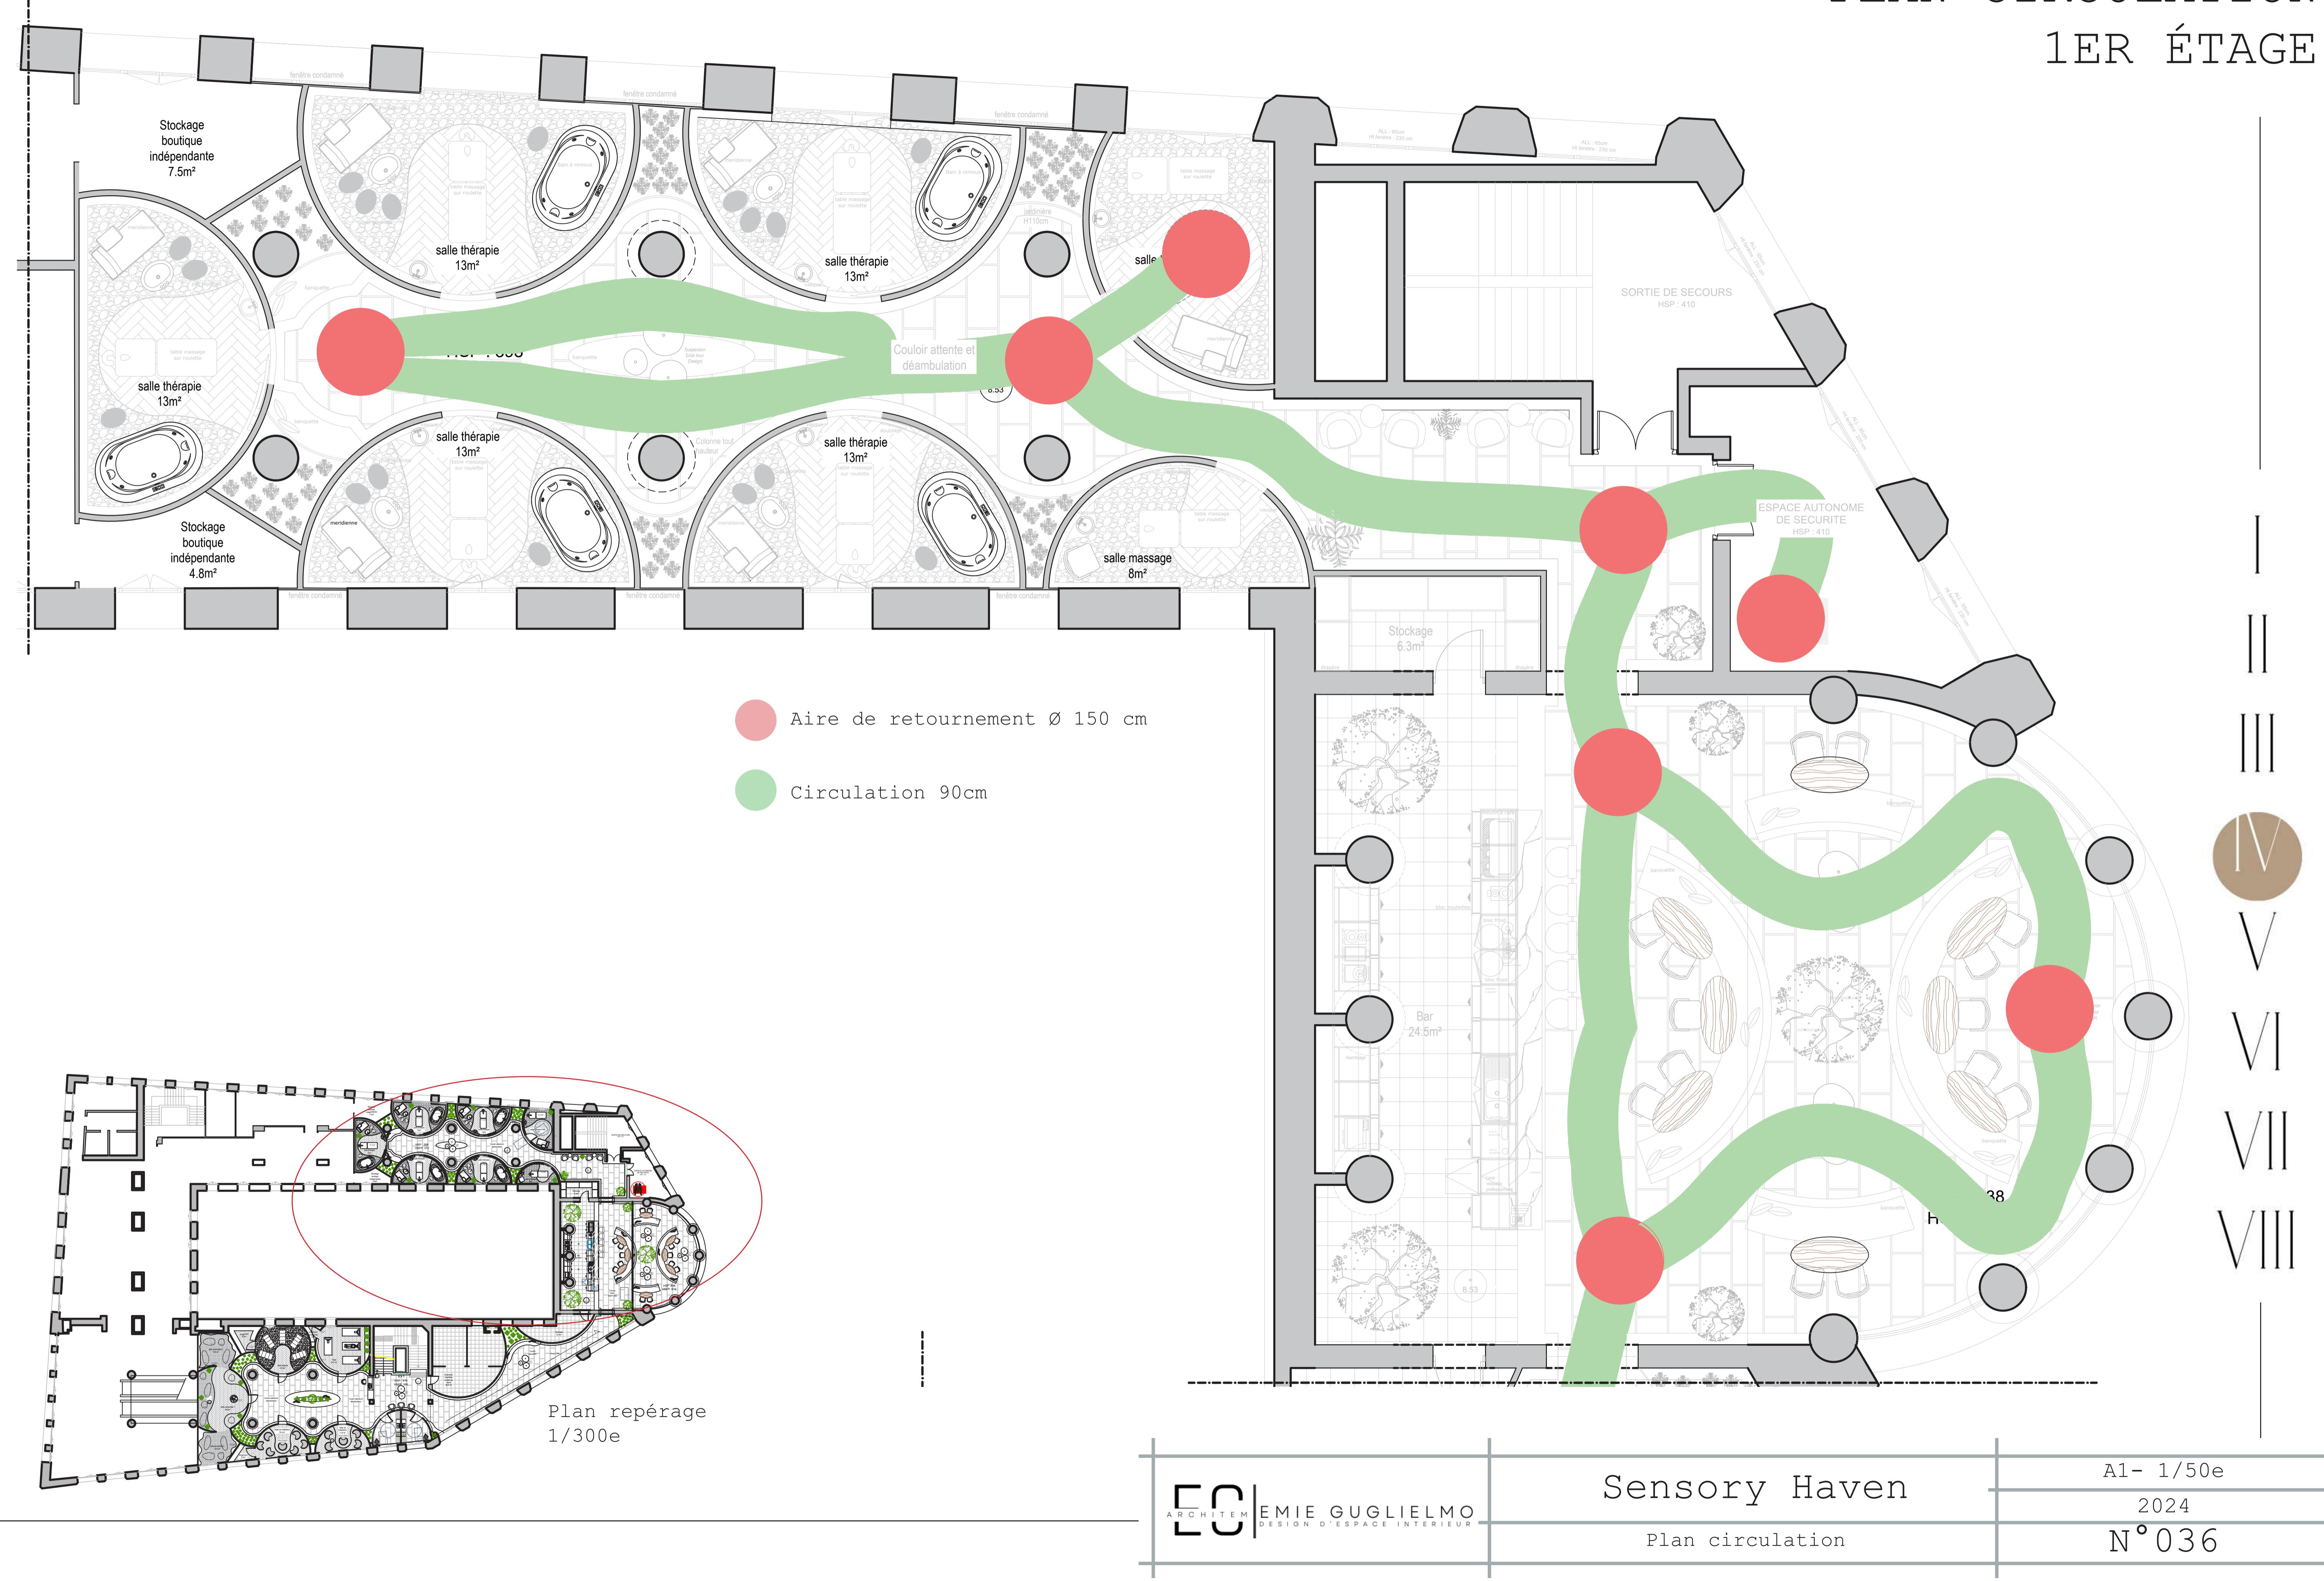

PLAN COULEUR REZ-DE-CHAUSSÉE

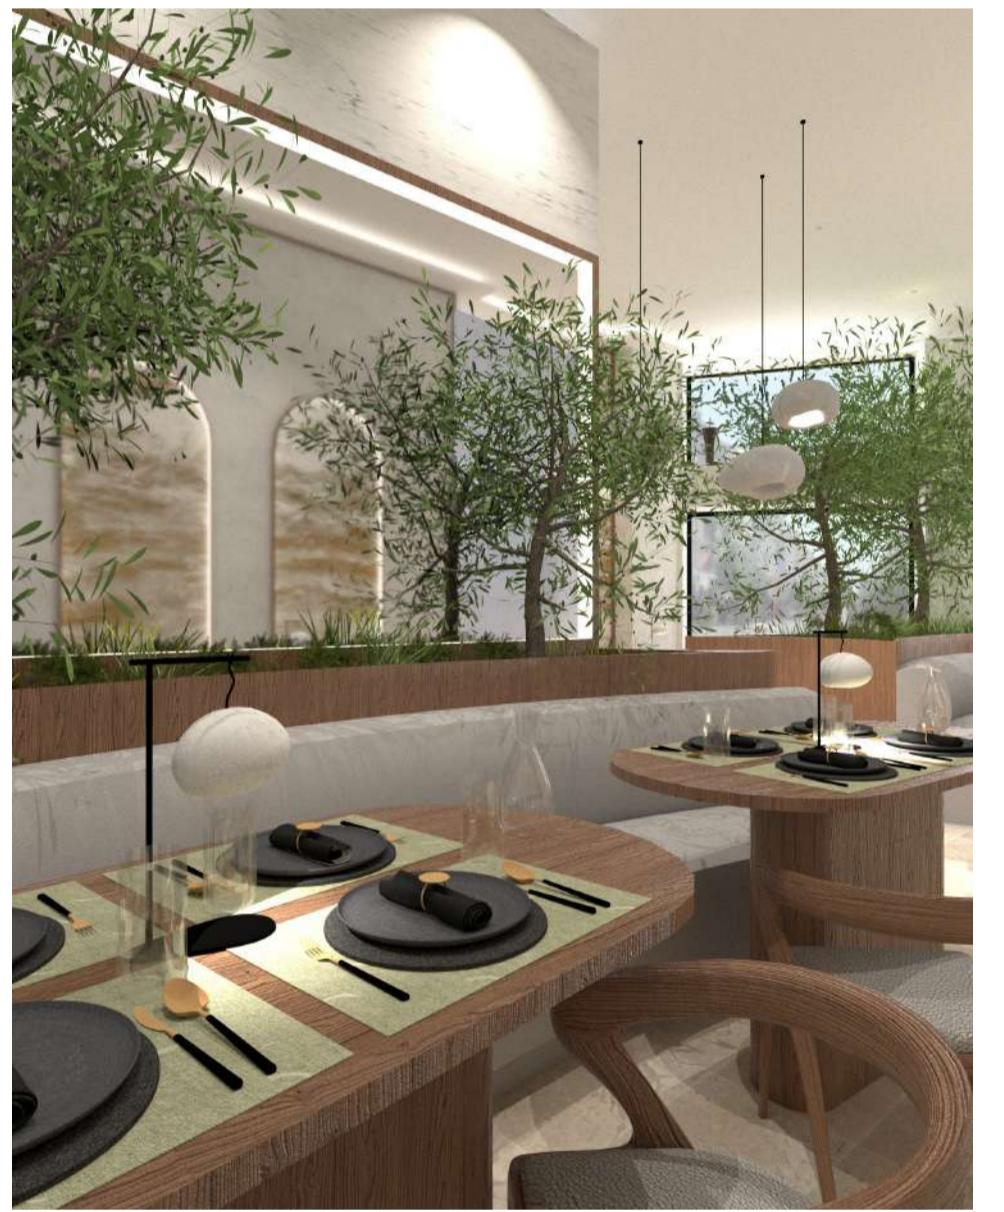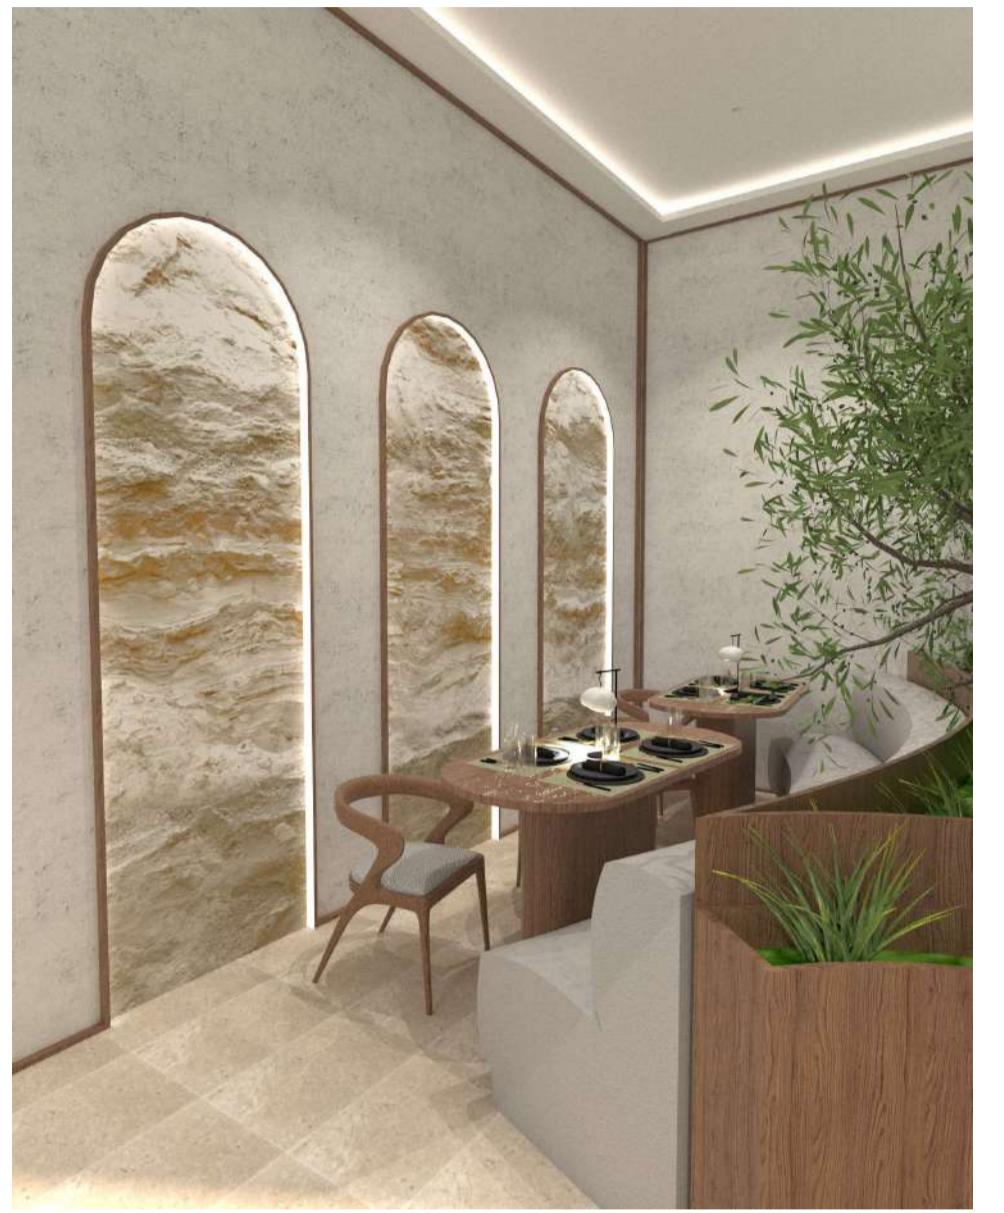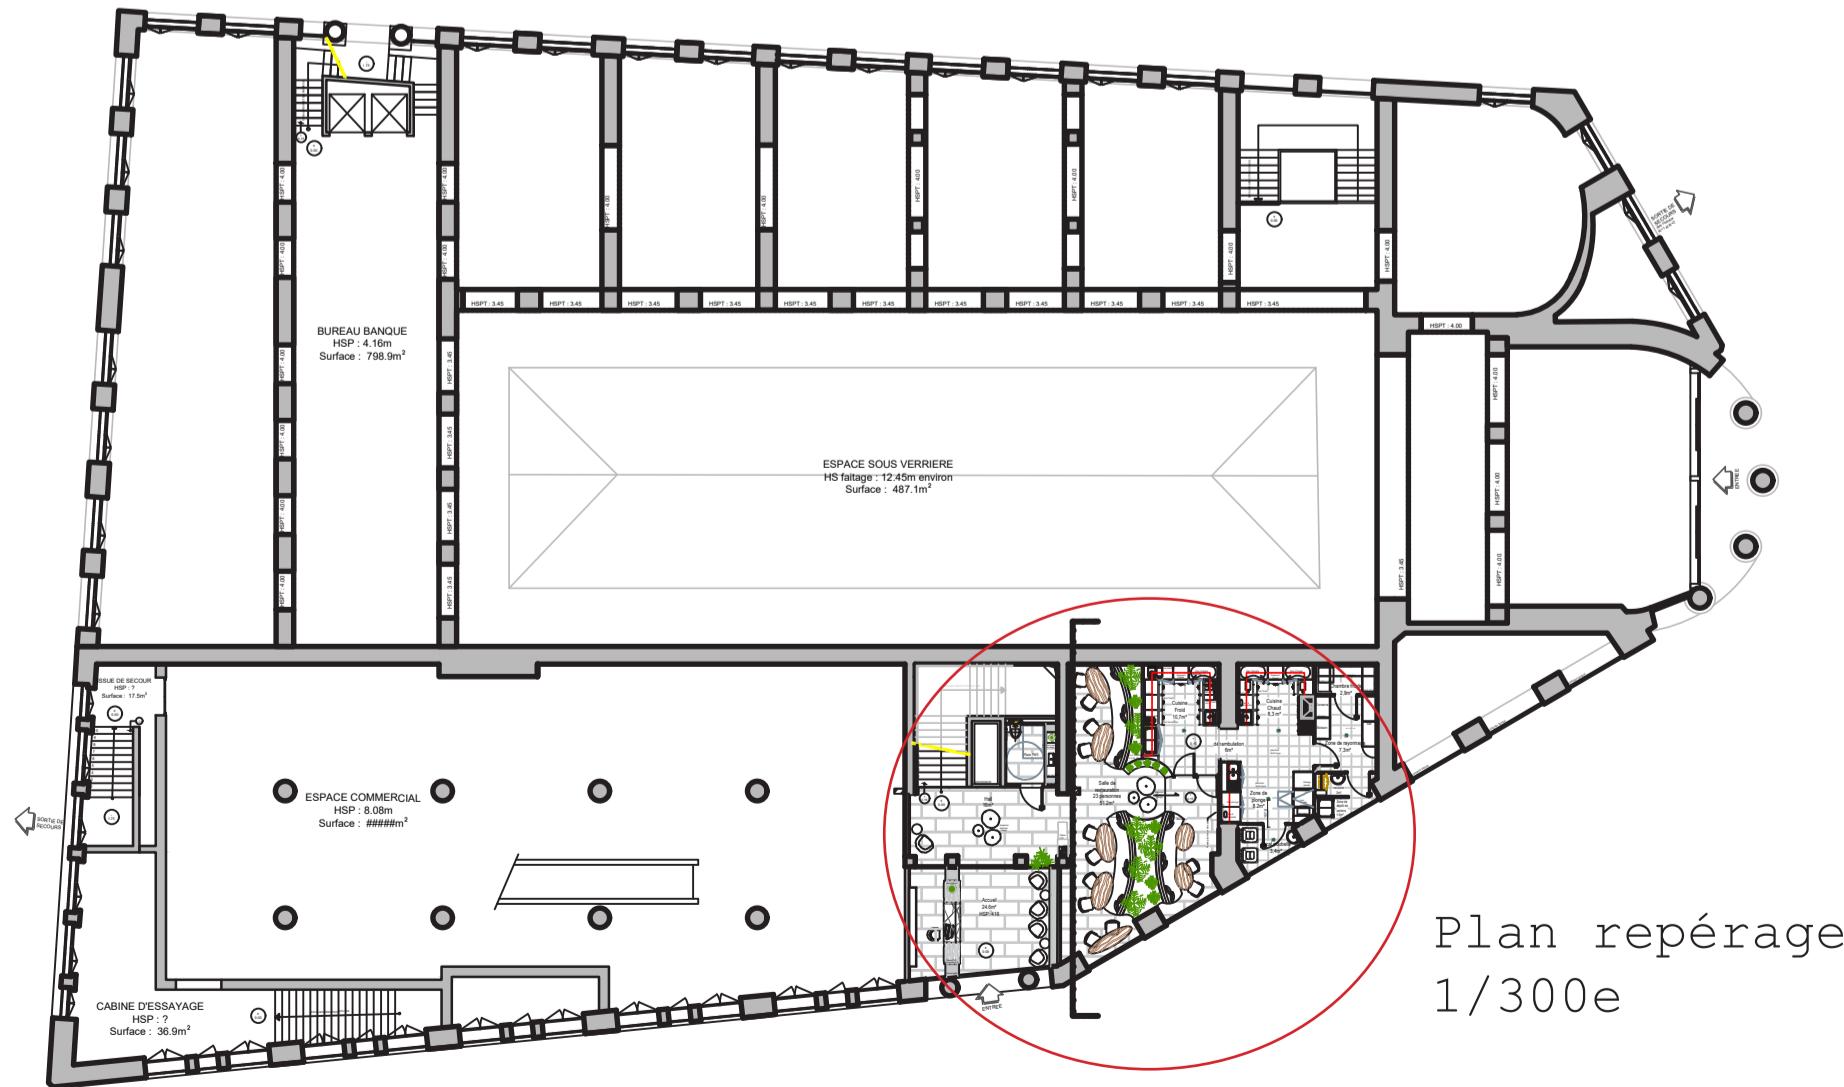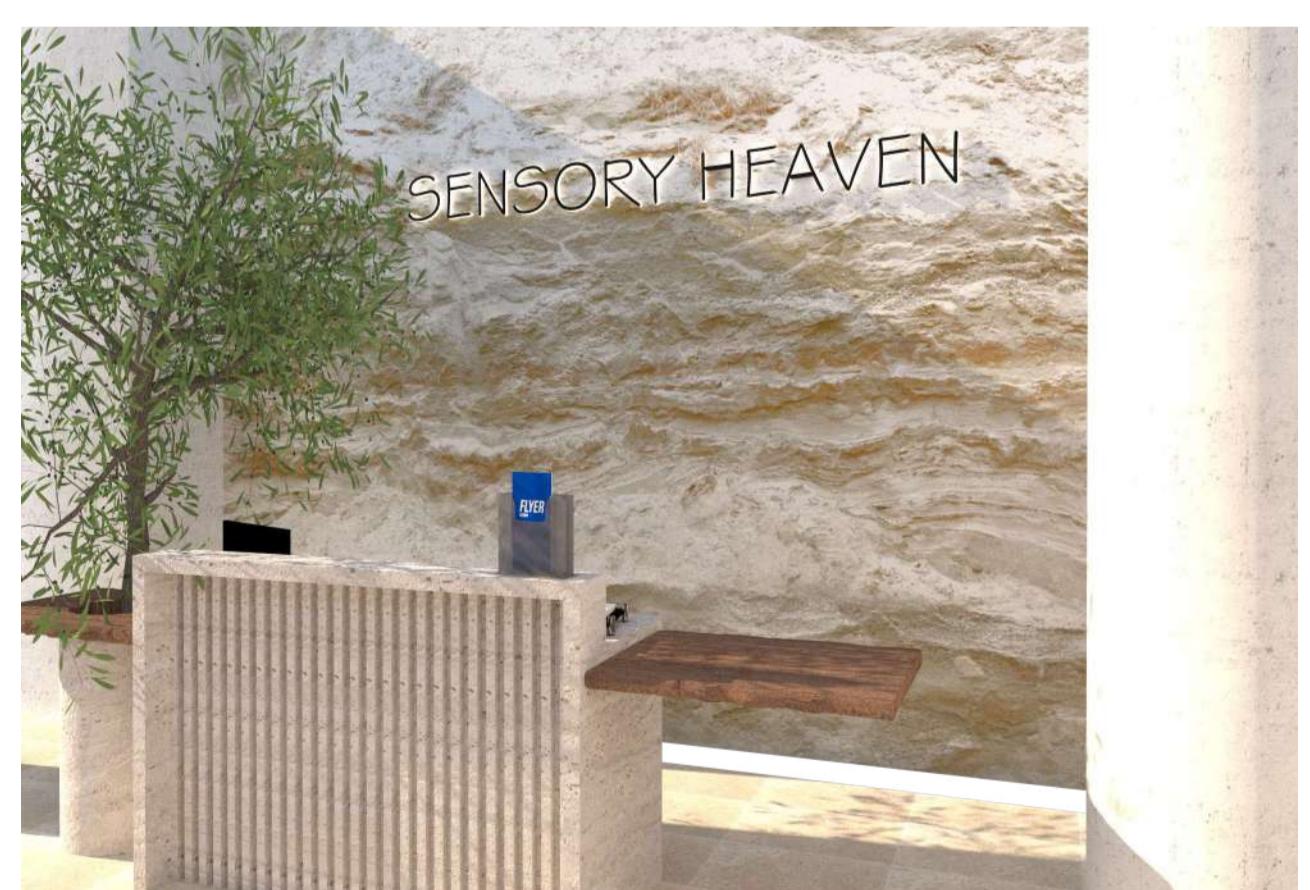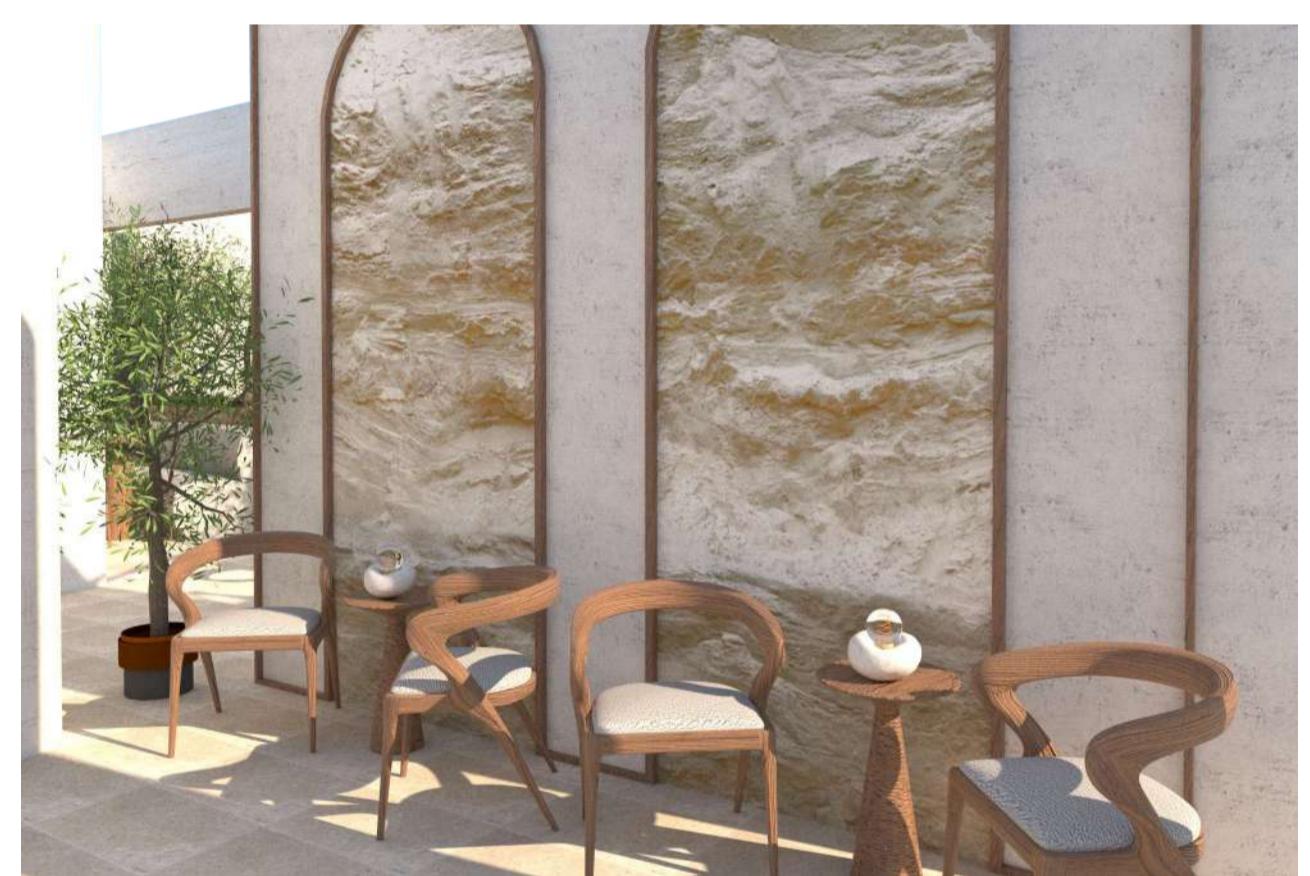

IV



V

VI

VII

VIII

PLAN COULEUR
1ER ÉTAGE

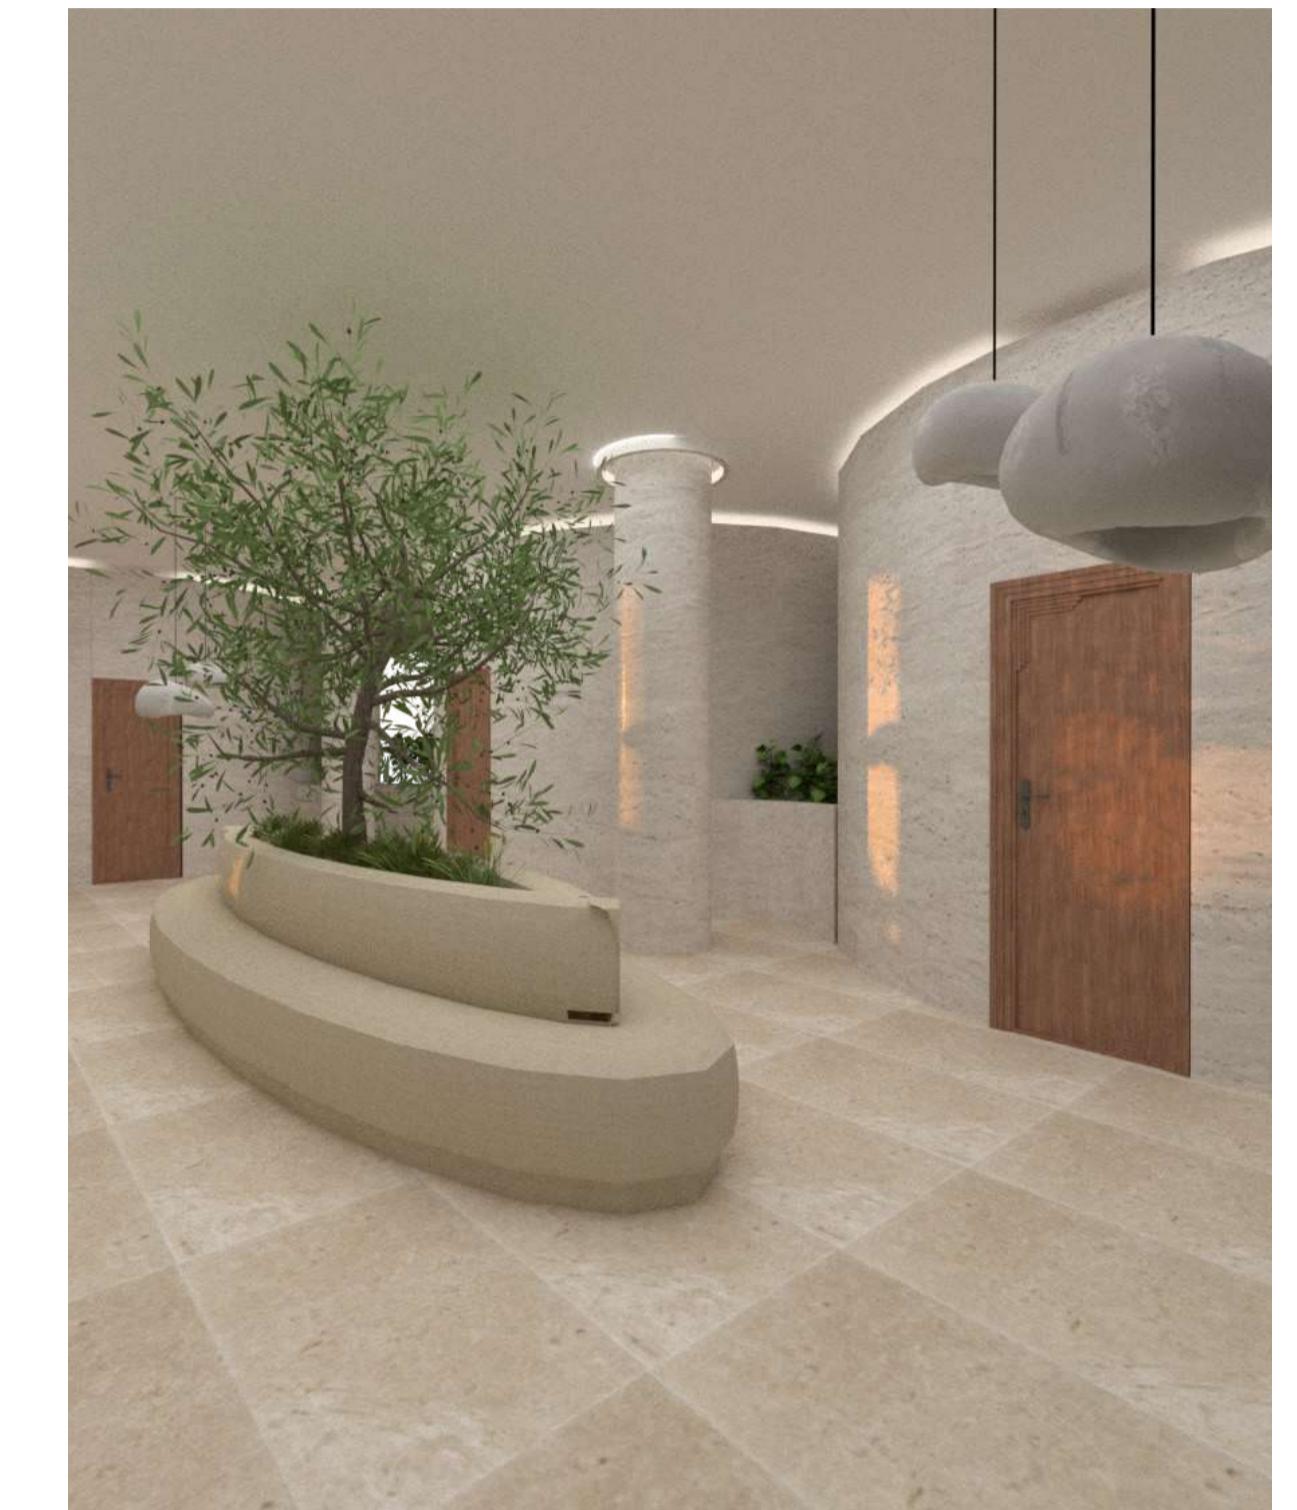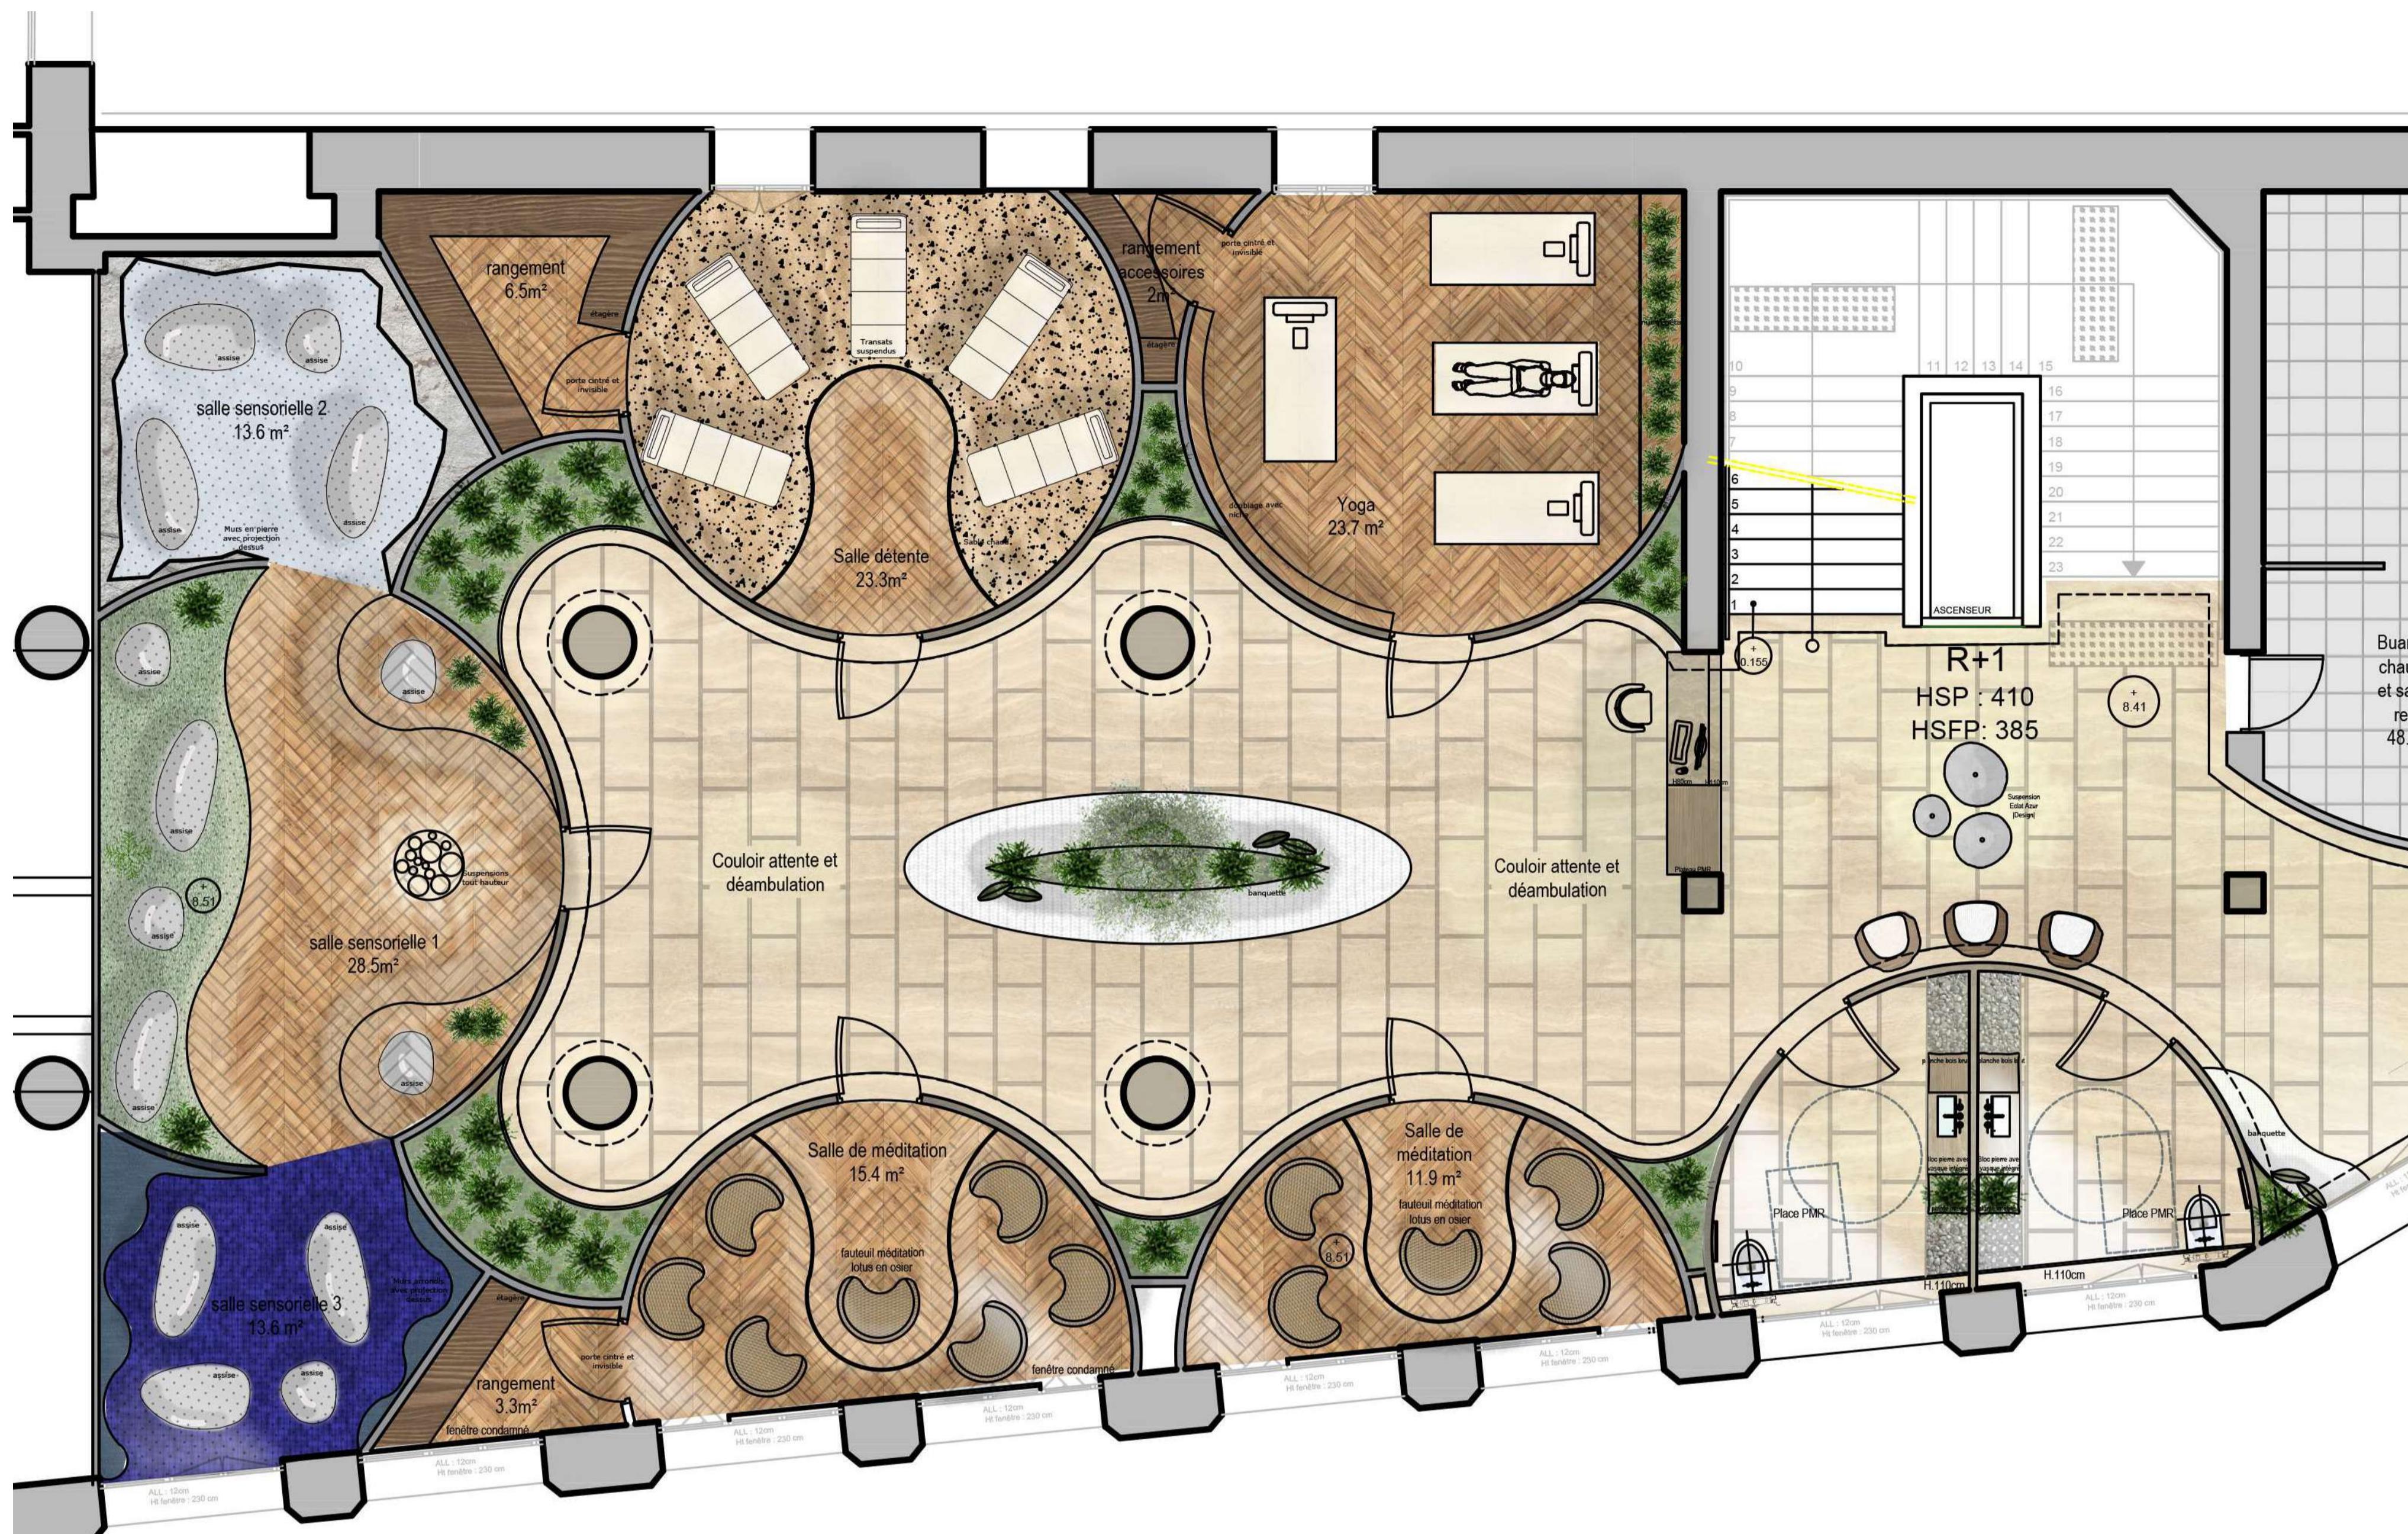



IV

V

VI




VII

VIII


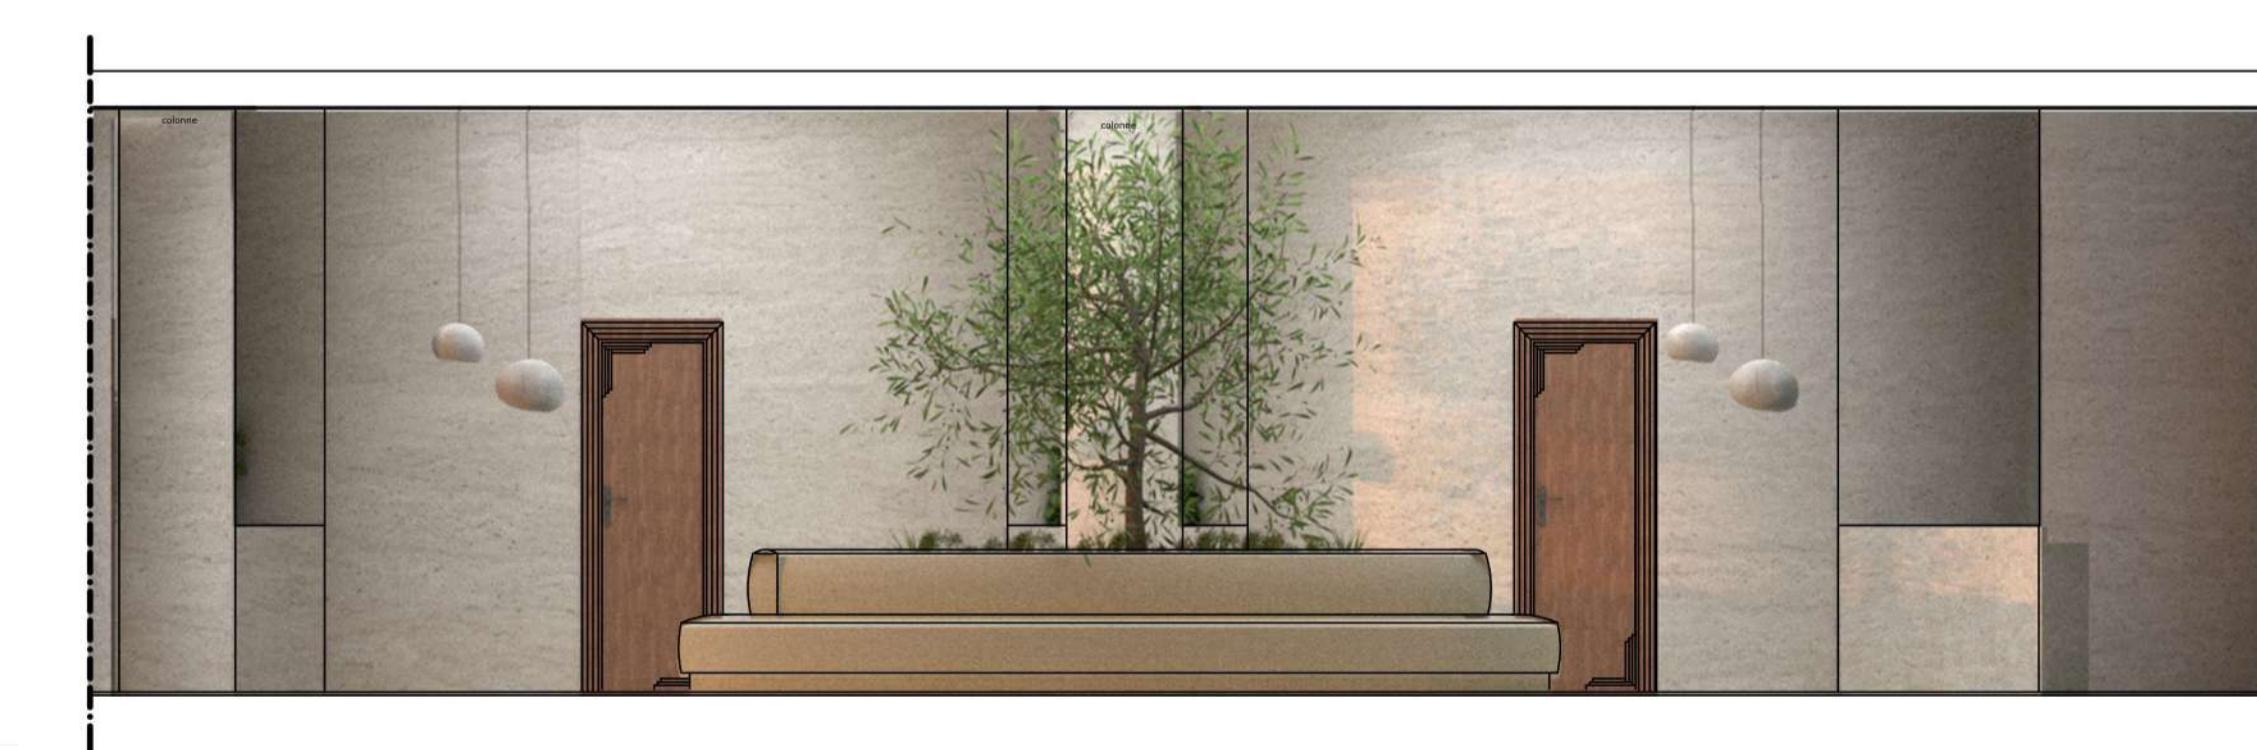
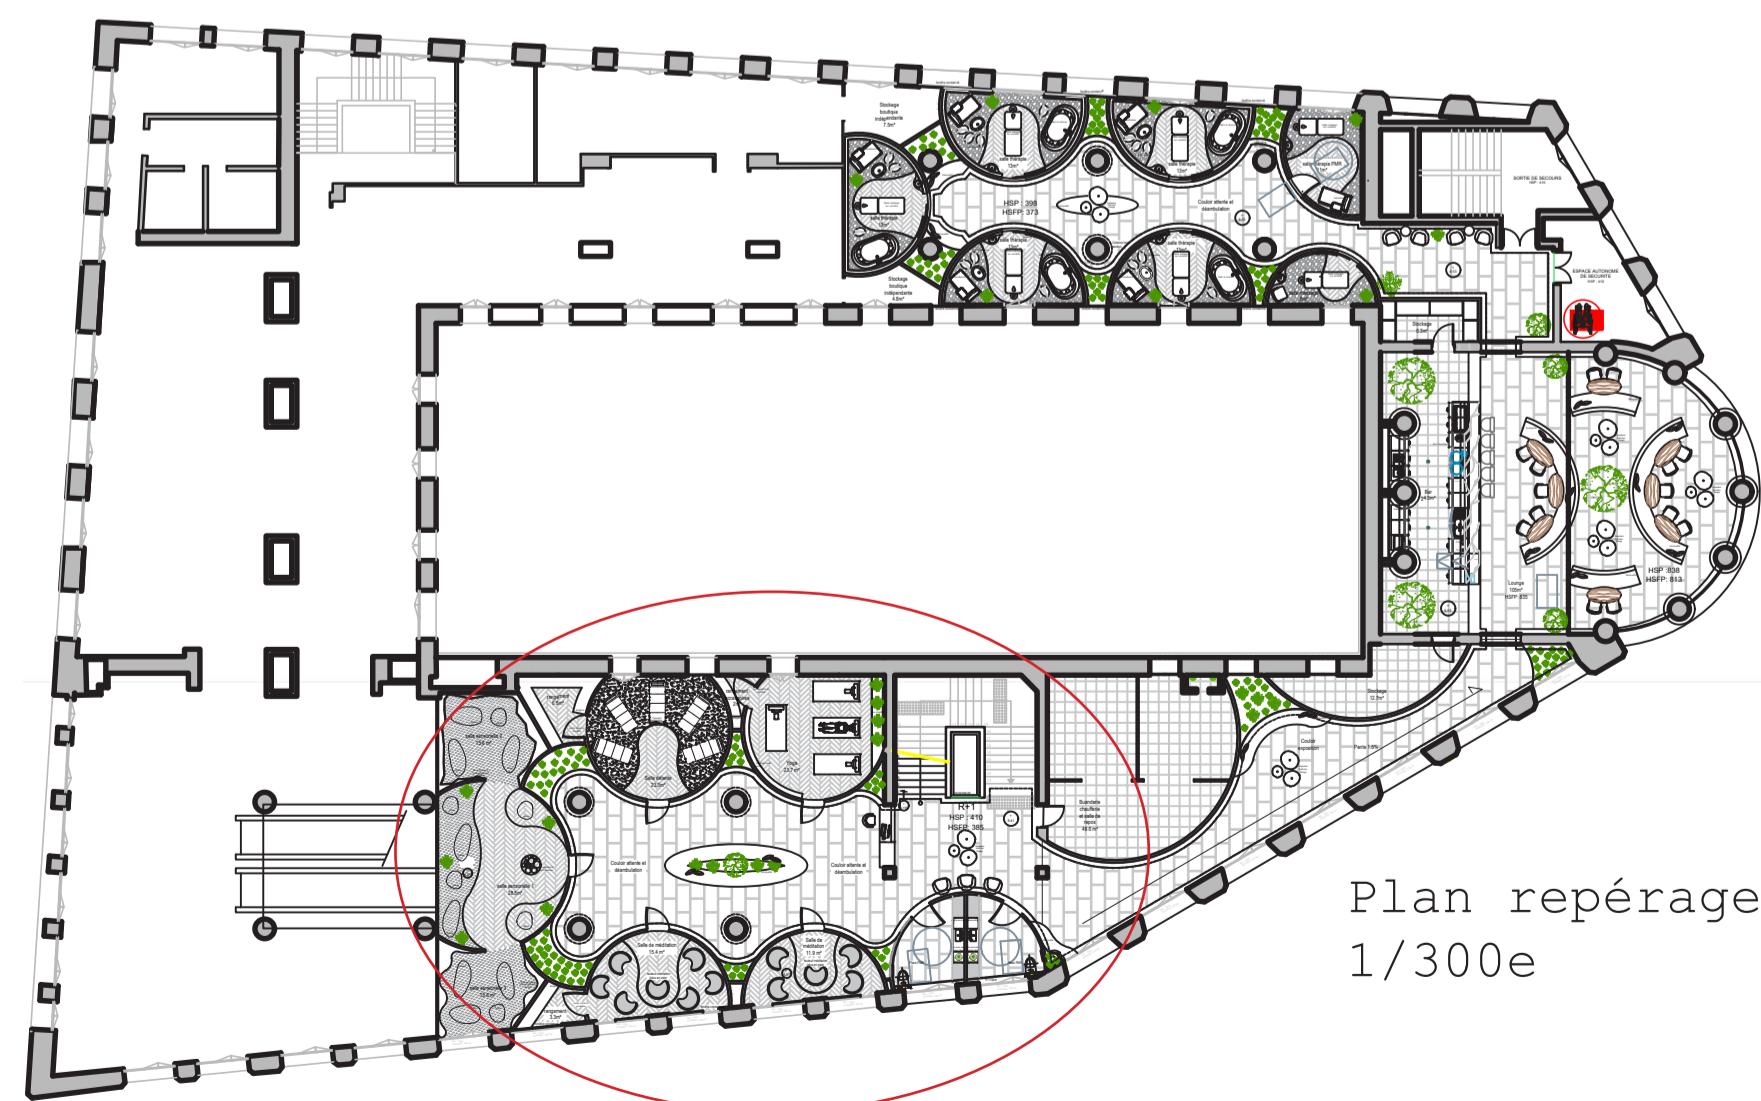


+8.53m

PLAN COULEUR
1ER ÉTAGE

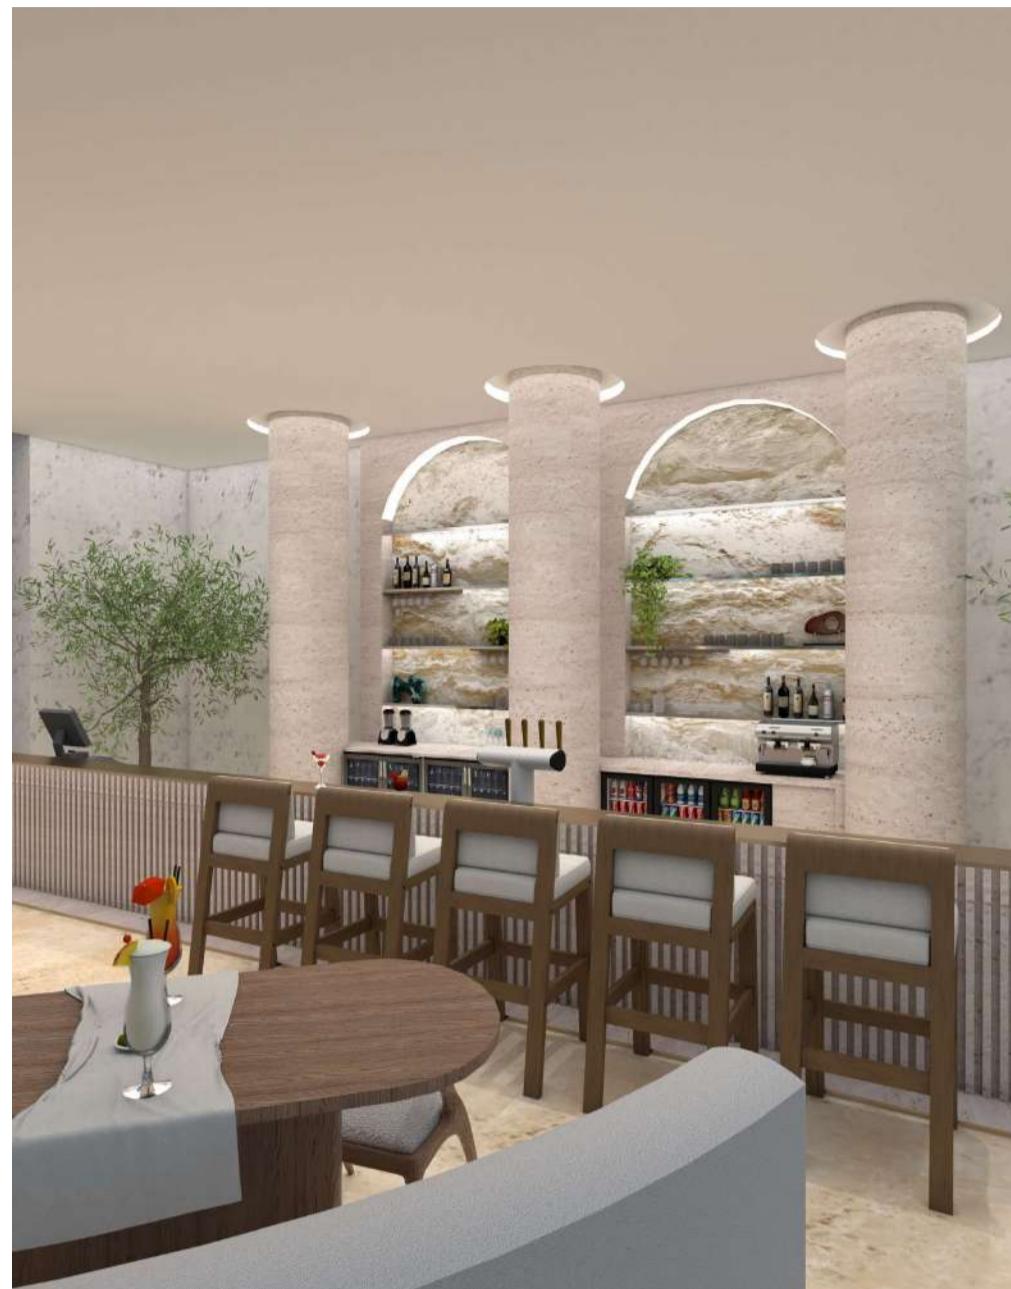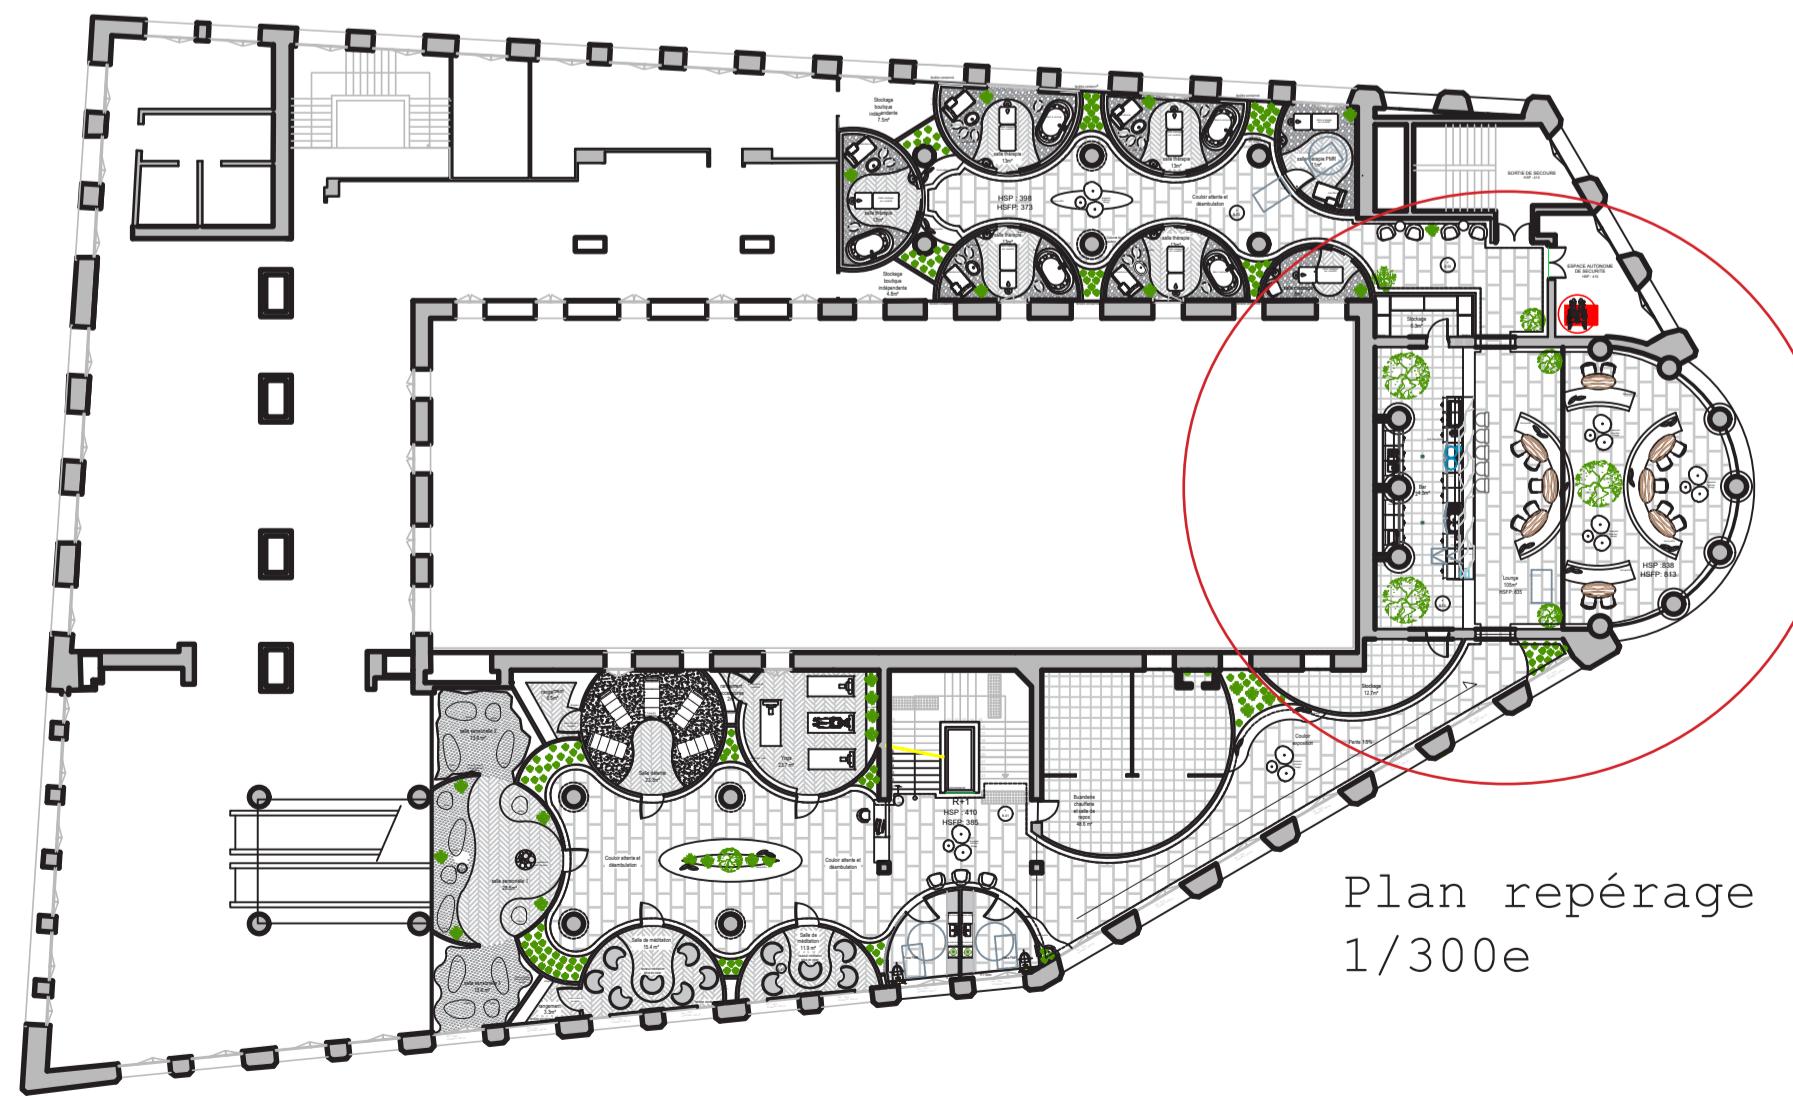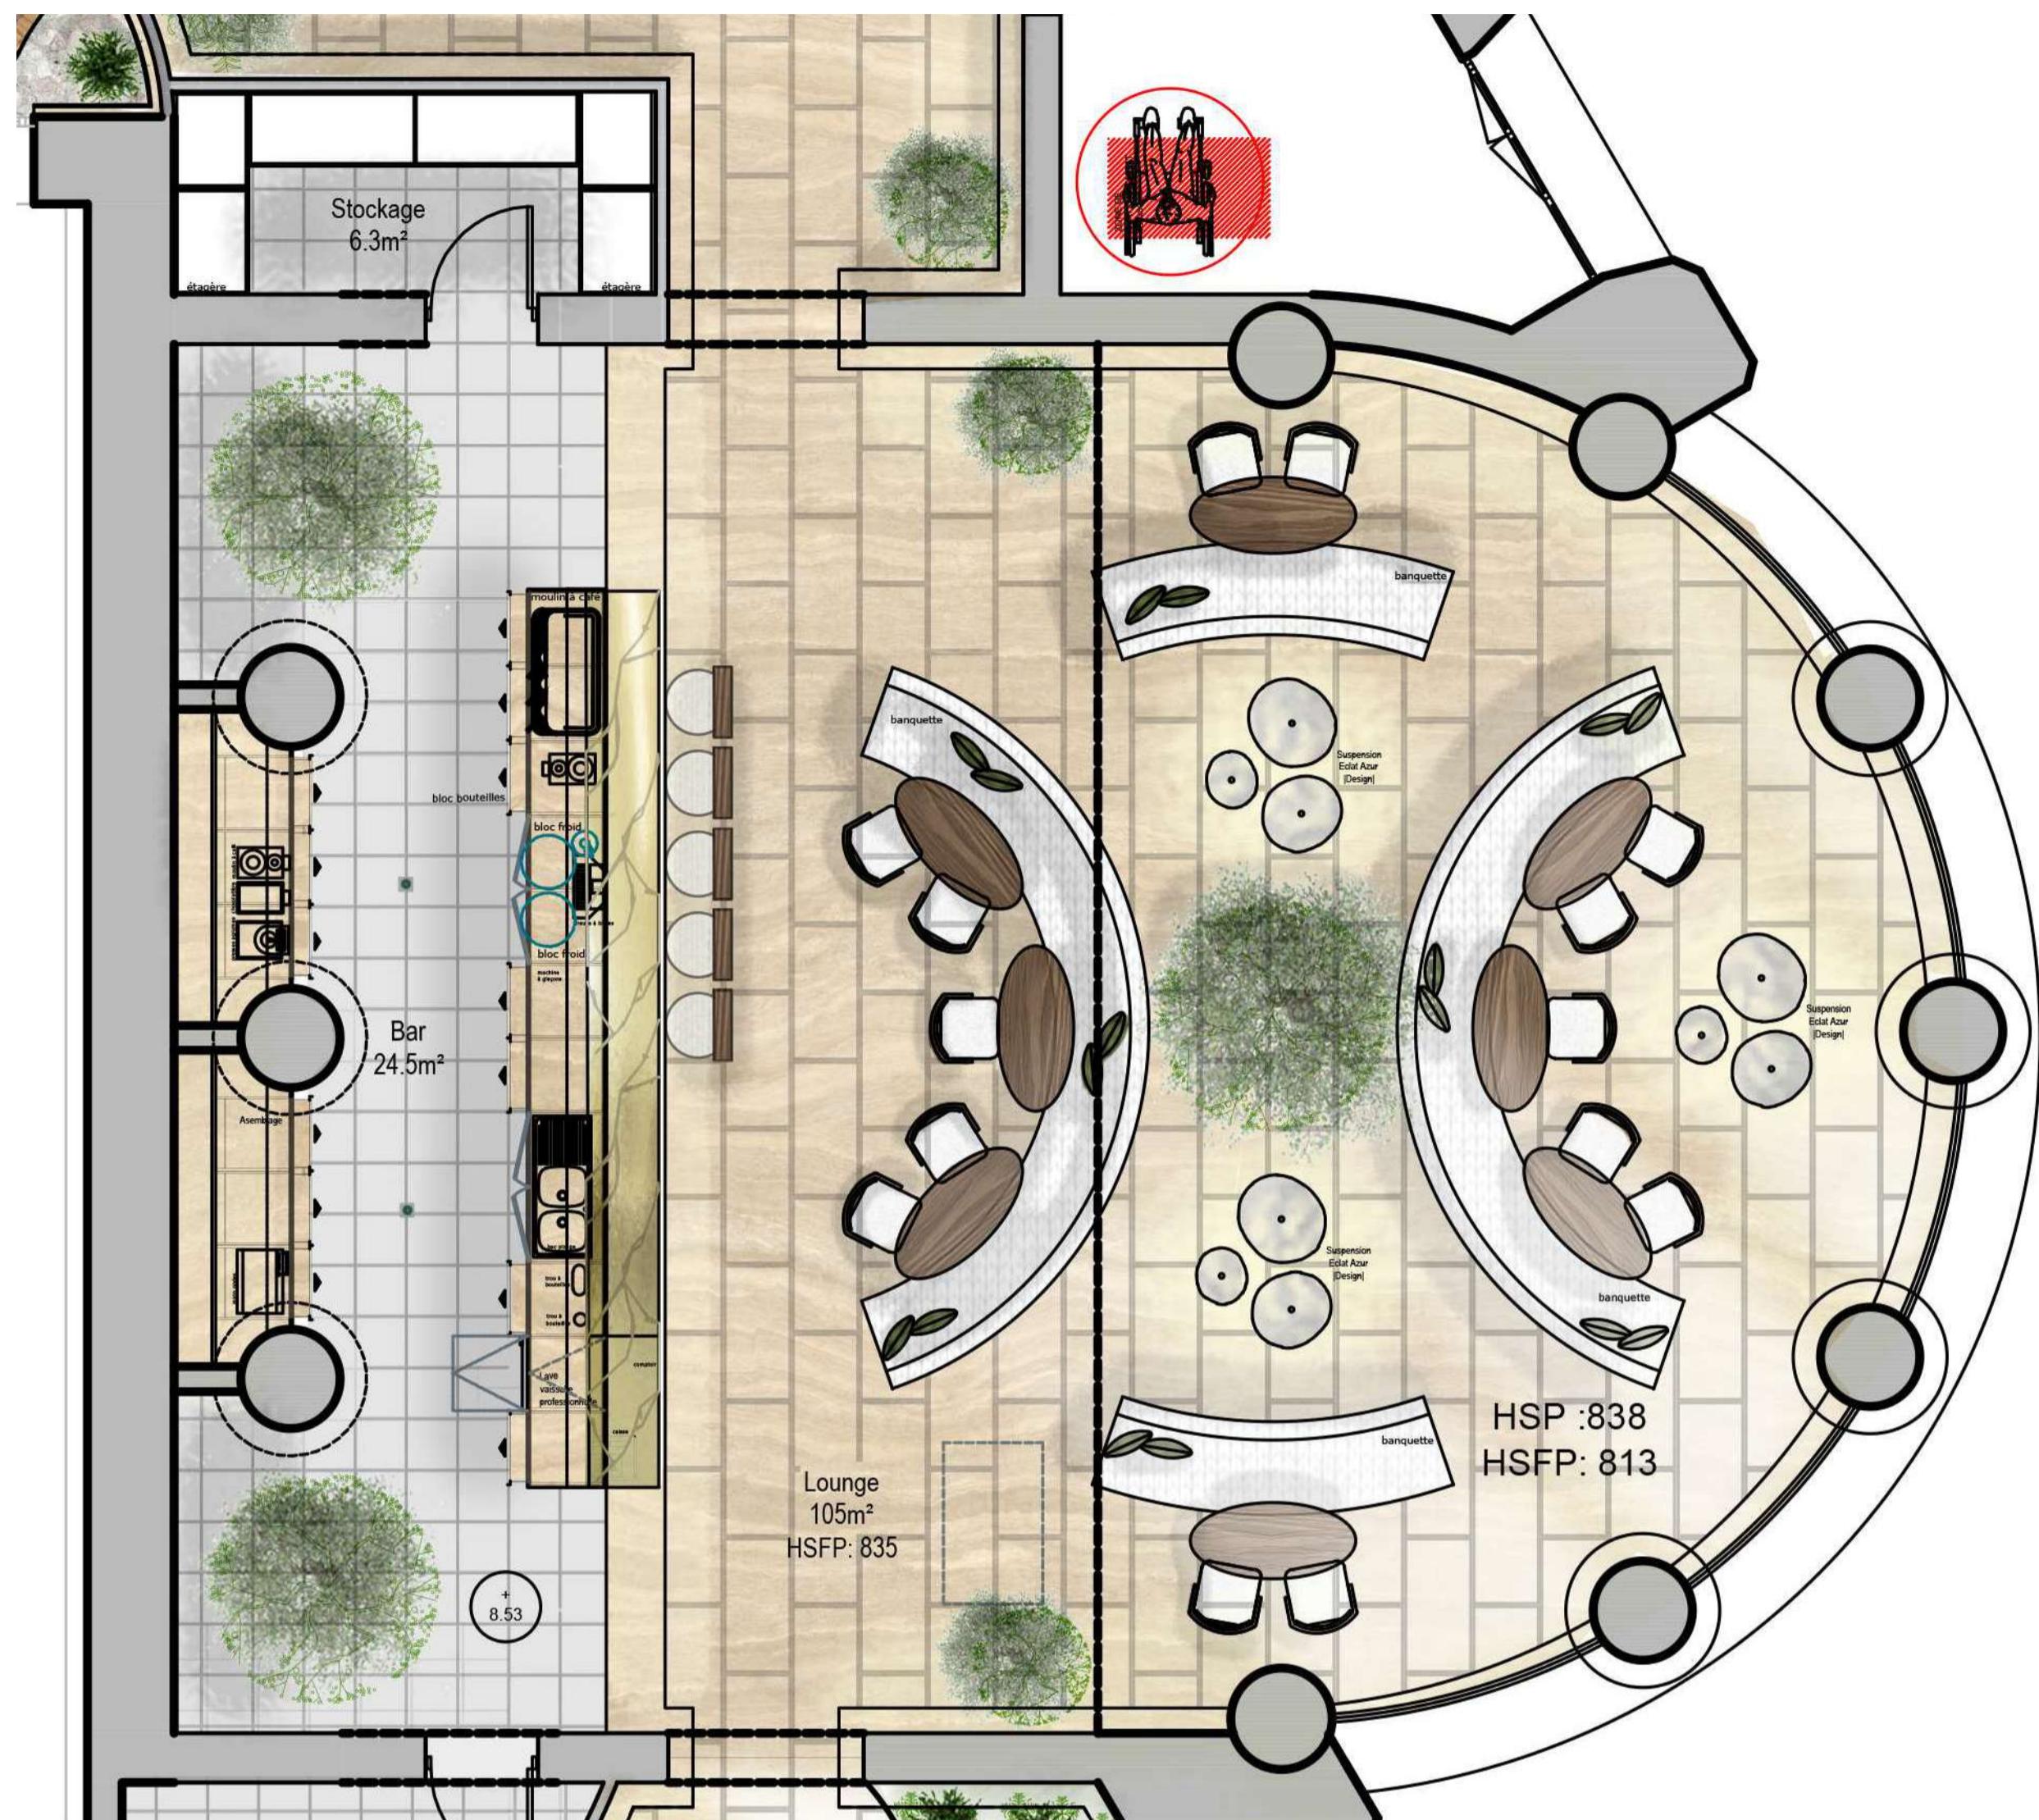

PLAN COULEUR 1ER ÉTAGE

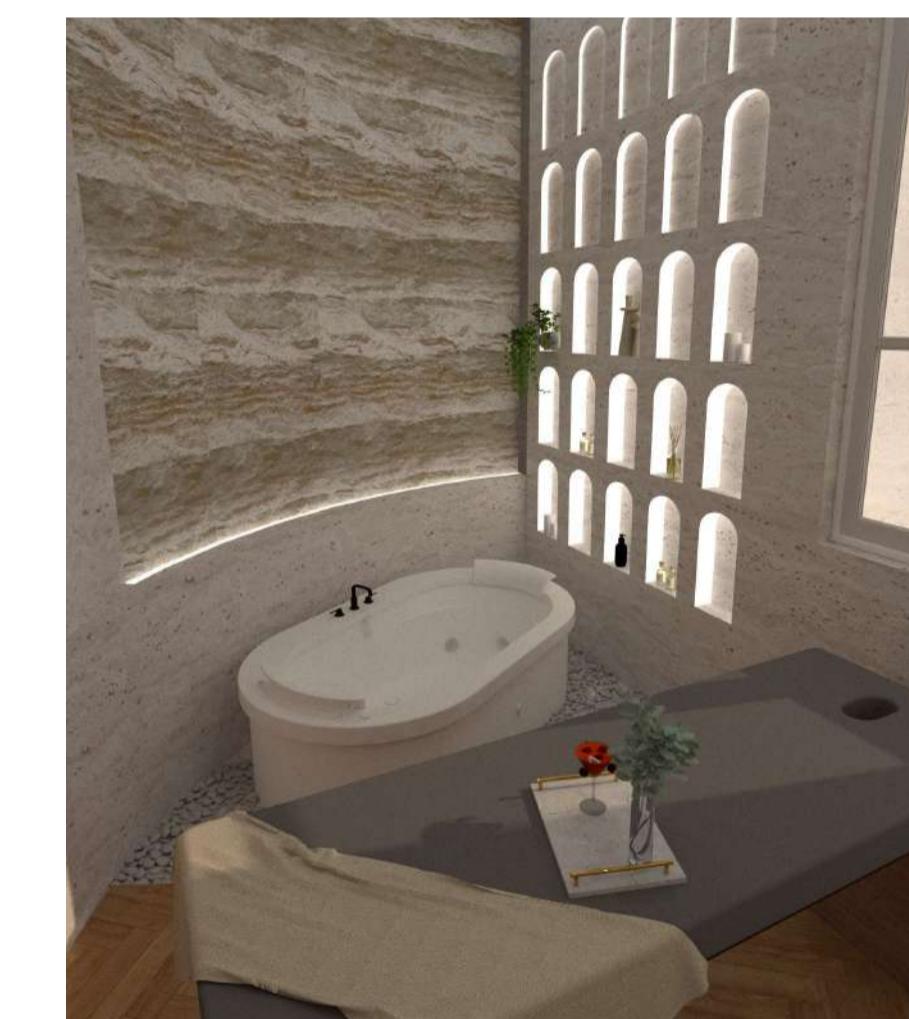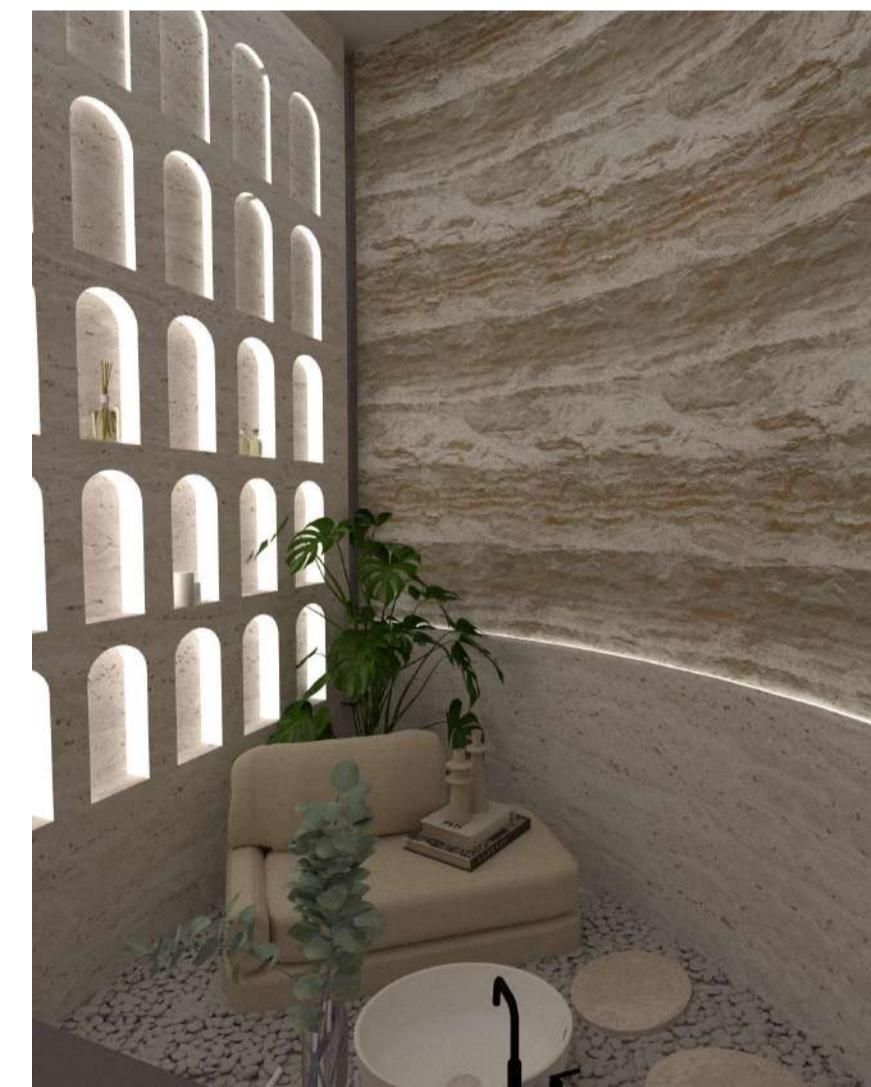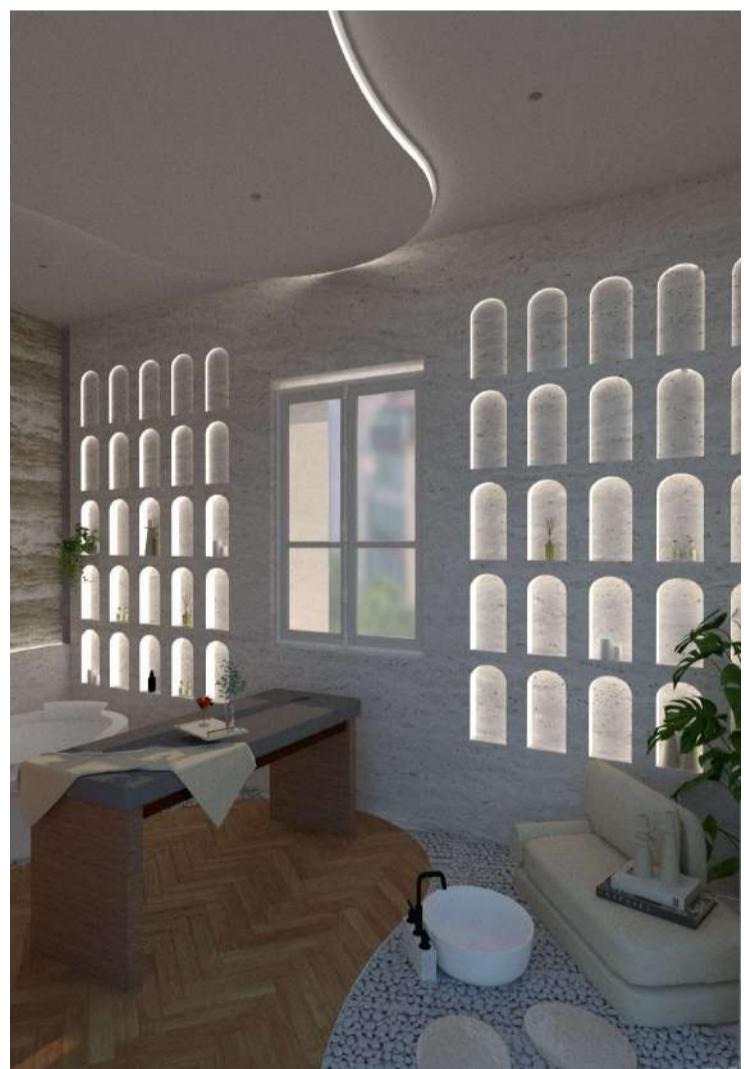

IV

V

VI

VII

VIII

