


APE

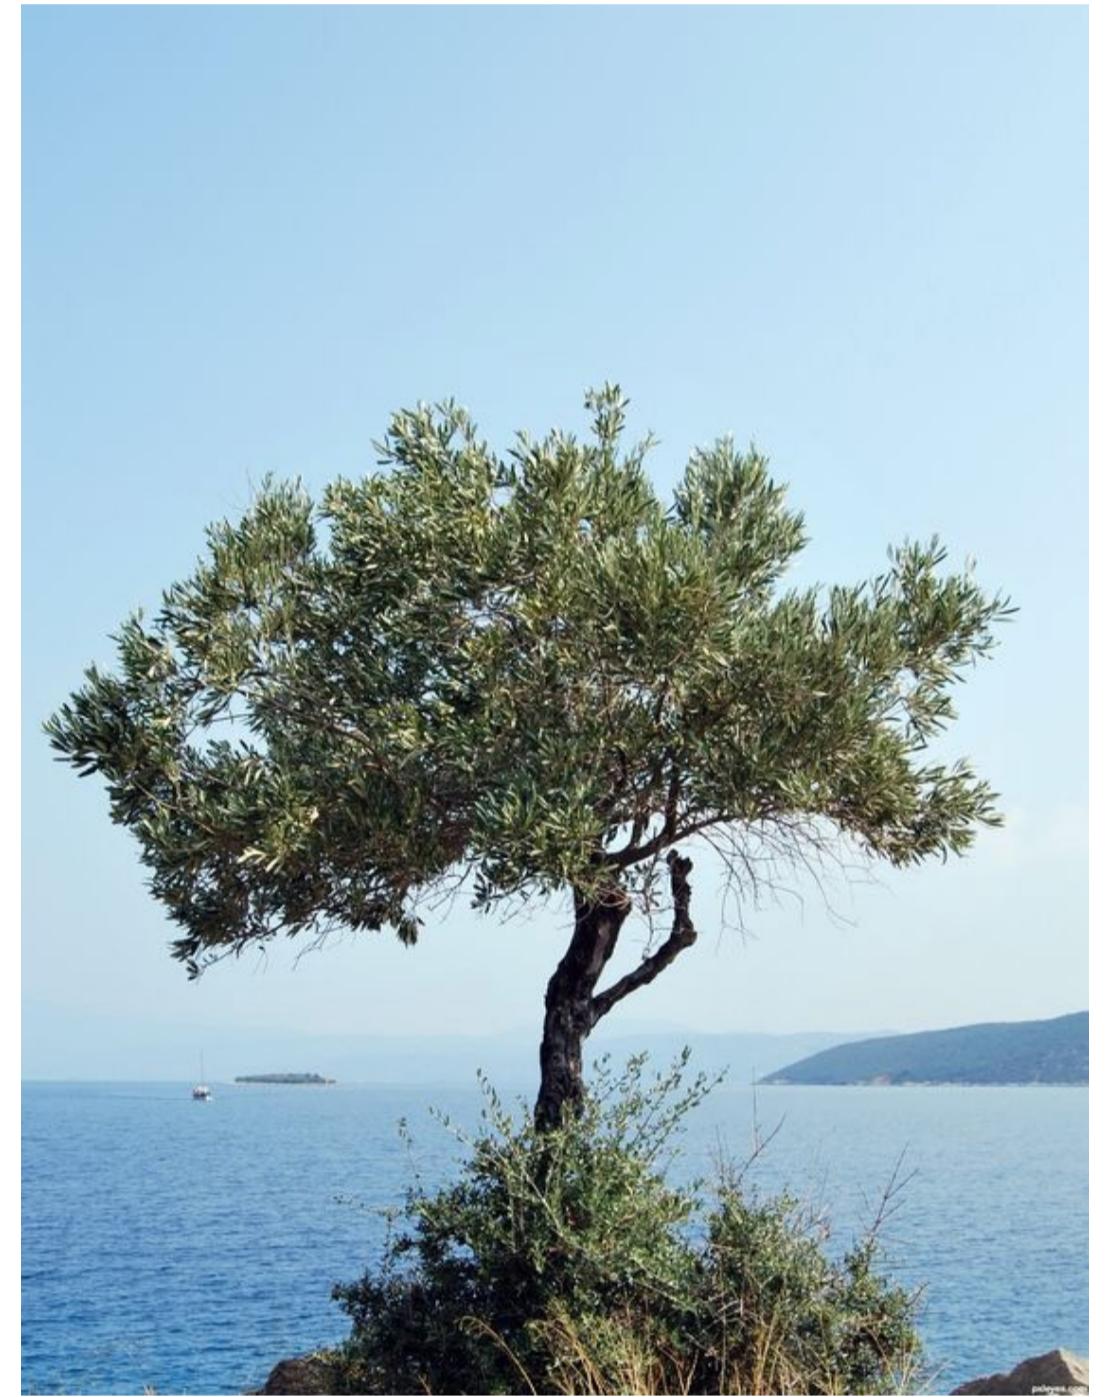


2024

EMIE GUGLIELMO

MEMOIRE PROJET
PROFESSIONNEL


CHAMBRE 20E

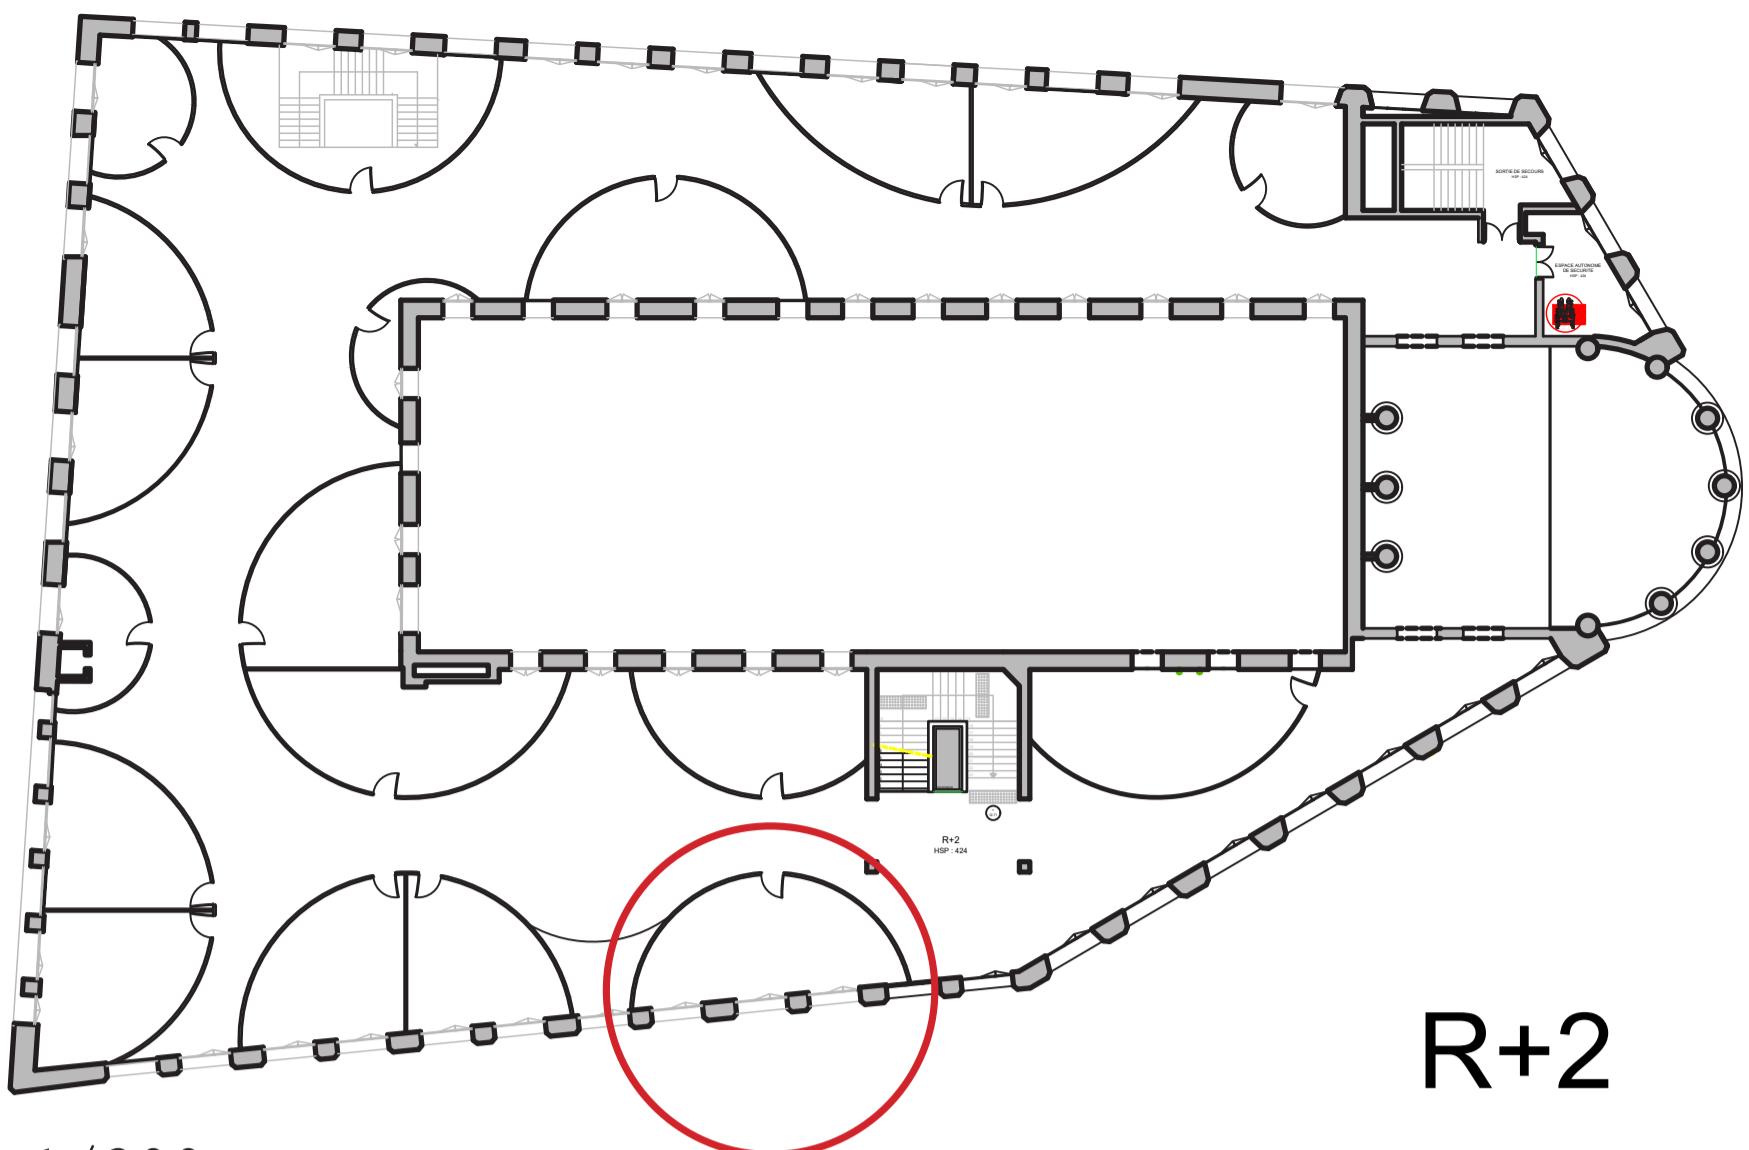


1/300e

R+2

- ① WC suspendu By Olympia Ceramica Ref :FOR1202R01
- ② Bâti support Geberit DF WC Sig8 Ref : 111.796 Dim : H114 90/110 VB
- ③ Spray bidet - Dornbracht Ref : 27 701 970-00
- ④ MADISON Porte-balai murale - Dornbracht Ref : 83 900 361-00
- ⑤ LULU Distributeur de papier - Dornbracht Ref : 83 500 710-00
- ⑥ Nourrice | distribution arrivées d'eaux chaudes et froides
- ⑦ VAIA Mélangeur lavabo - Dornbracht Ref : 20 705 819-00
- ⑧ Plan vasque Travertin,double vasque intégré
- ⑨ Planche bois brut | chêne
- ⑩ Ideagroup BEAUTY Miroir ovale suspendu double-face
- ⑪ ARTICLES GÉNÉRIQUES AQUAHALO Panneau de pluie - Chrome | Dorn Bracht | ref: 41 750 979-00
- ⑫ VAIA Mitigeur monocommande Ref : 36 120 809-00
- ⑬ LULU Garniture de douche avec rosaces individuelles Ref:27 808 710-00
- ⑭ Niche Rigole de douche en acier inoxydable - OMP Ref : DEFLOW 973.801.8
- ⑮ Sol galet blanc
- ⑯ Plante Monstera
- ⑰ Sol de douche + 0.12
- ⑱ Fauteuil - Paolo Castelli Armchair Vao
- ⑲ Modenature Coffee table CHAI
- ⑳ Lampe à poser | Eclat Azur
- ㉑ Paolo Castelli Console Kenya
- ㉒ Cloison basse | Hauteur 110cm Avec verrière tout hauteur - sur mesure - Verre plakglass et profil aluminium noir
- ㉓ Lit 180 x 200cm
- ㉔ Gejst Side table Ismo dark oak
- ㉕ Suspension | Eclat Azur
- ㉖ Frigorio HULI Banquette en bois massif
- ㉗ Bureau sur mesure | Panneau de bois massif contre plaqué - Columbia Forest Products - Pure Bond
- ㉘ Trape pour television escamotable - mécanisme Flatlift ECO TV-Lift
- ㉙ Carel Woodworks Pouf Gizmo
- ㉚ Panneau | doublage
- ㉛ Tapis Eichholtz - carpet sestri 118110
- ㉜ Porte coulissante - Affleurant
- ㉝ Dressing sur mesure | Panneau de bois massif contre plaqué - Columbia Forest Products - Pure Bond
- ㉞ Boffi TWIG Porte-serviettes sur pied en iroko
- ㉟ Parquet Carréol | Chêne semi massif, vanille - ref: 00602318016
- ㉟ Moab DOOR TEAK STRIPES Receveur de douche à lattes à l'italienne en teck
- ㉟ CUPASTONE PIERRES DISTRIBUTION Dallage sol travertin - light mix - opus 4 formats, ref: Pointp4190321
- ㉟ TRAVERTIN LIGHT MIXTE CUPASTONE PAVÉS 10x25 cm
- ㉟ PLACO Plaque de plâtre cintrable Placoplatre BA10 - 2,6x1,2 m - ép. 10 mm
- ㉟ revêtement, Carrelage Zellige Marocain Bleu Magique 5x15 cm, Ro'manature
- ㉟ Corniche à éclairage indirect- Staff décor - D104
- ㉟ Plâtre staff effet pierre
- ㉟ Peinture naturelle à la chaux | couleur blanc vieilli
- ㉟ Panneau bois massif contre plaqué - Columbia Forest Products - Pure Bond
- ㉟ Tissage Cannage | panneau sur mesure CMO Paris
- ㉟ PANNEAUX MURAUX CANNELÉS en platre, effet pierre naturelle travertin | Design and Visual Concepts
- ㉟ Boîte à rideaux

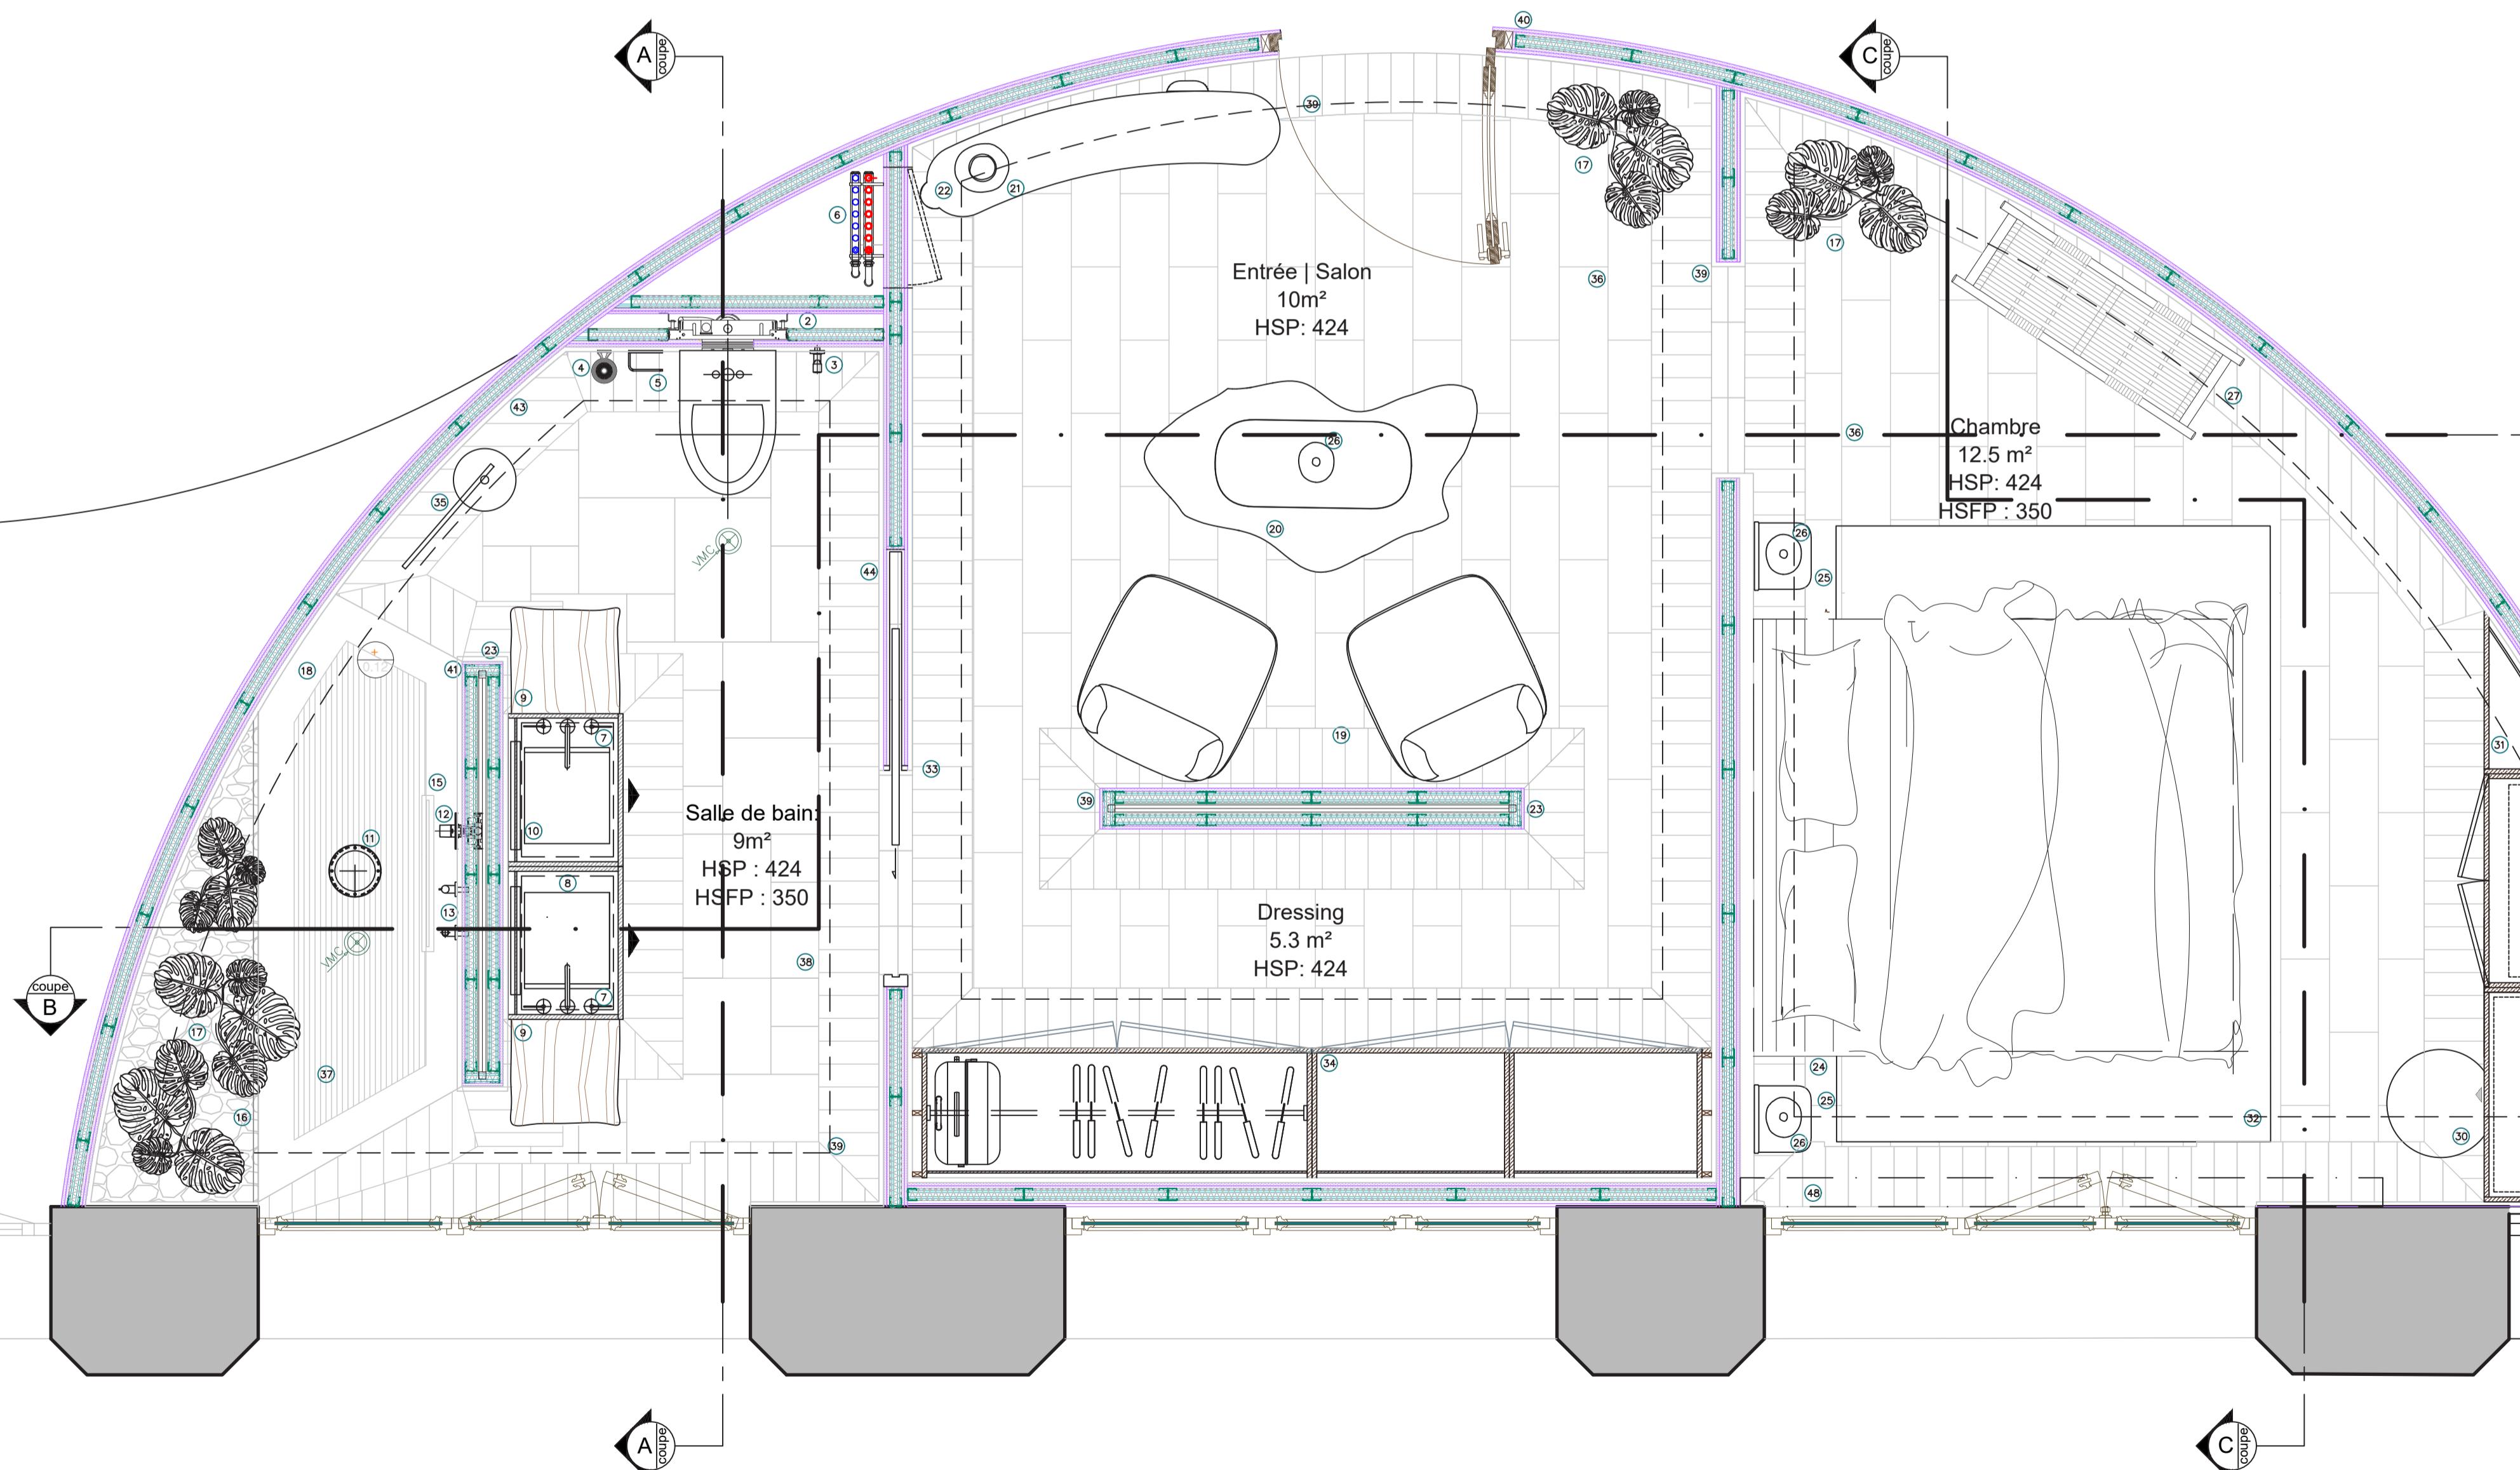


COUPES

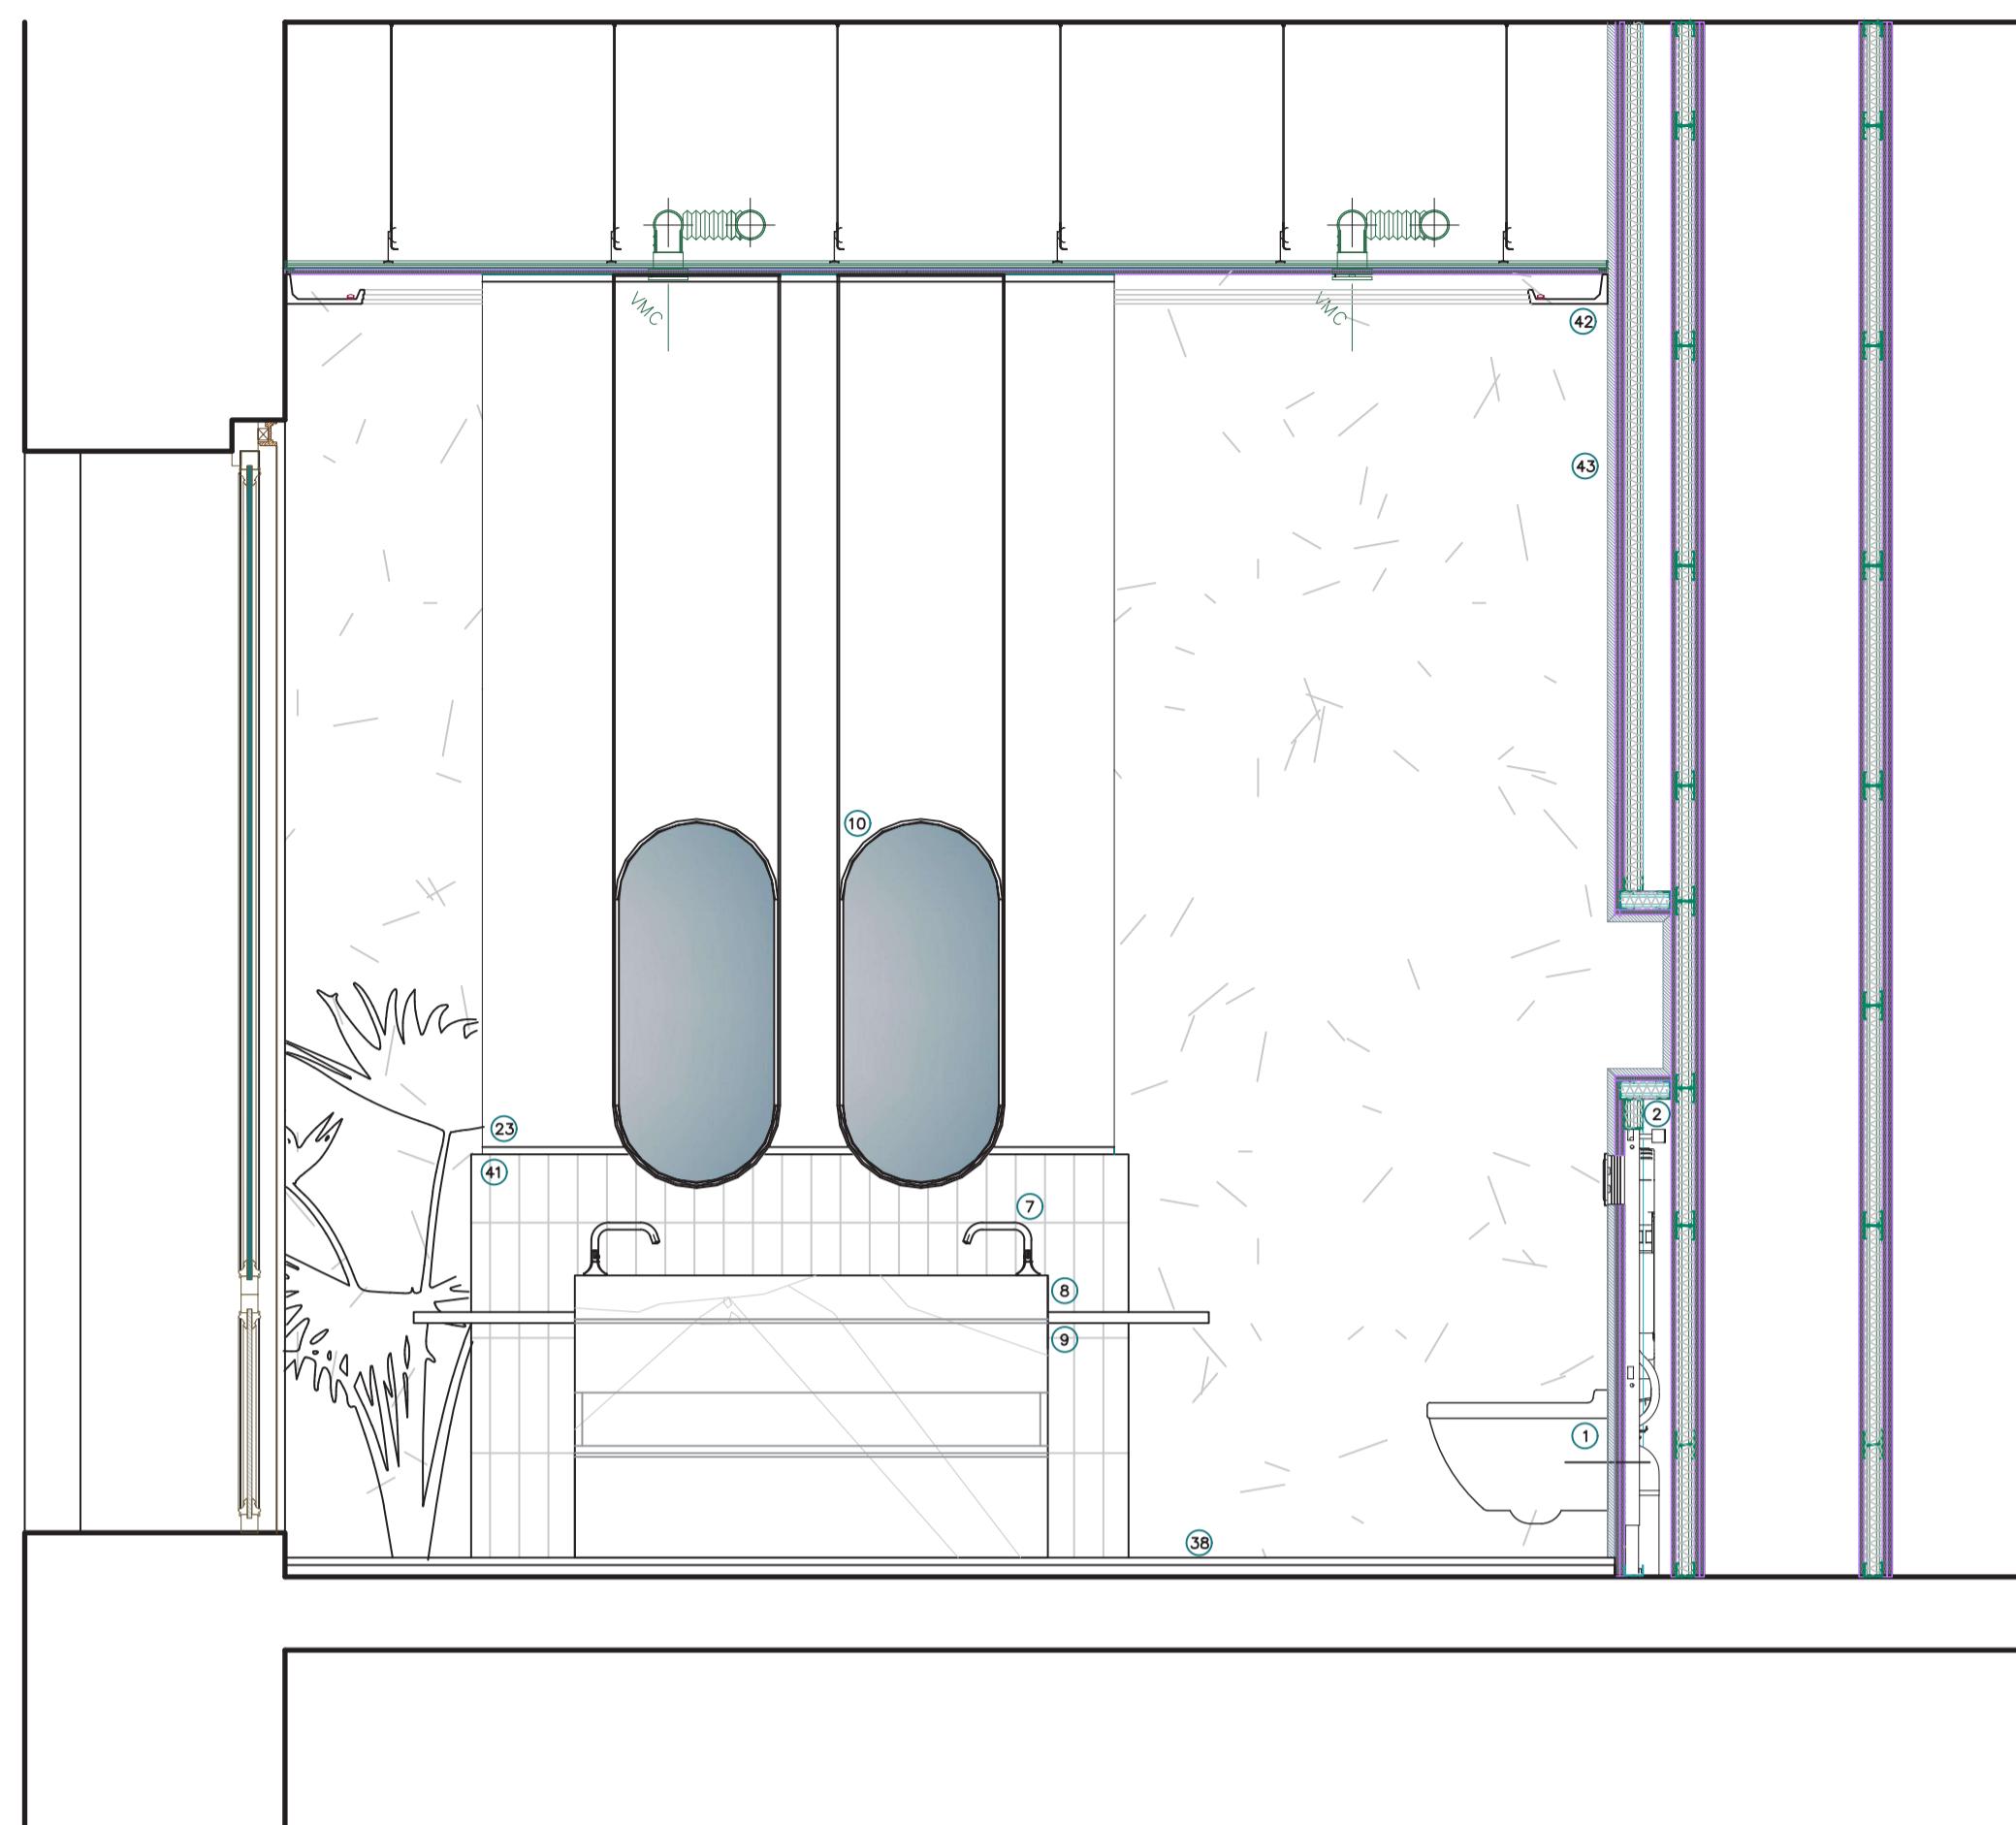

Ideagroup
BEAUTY
Miroir ovale suspendu
double-face



ARTICLES GÉNÉRIQUES
AQUAHALO Panneau de
pluie - Chrome | Dorn and
Bracht | ref: 41 750
979-00

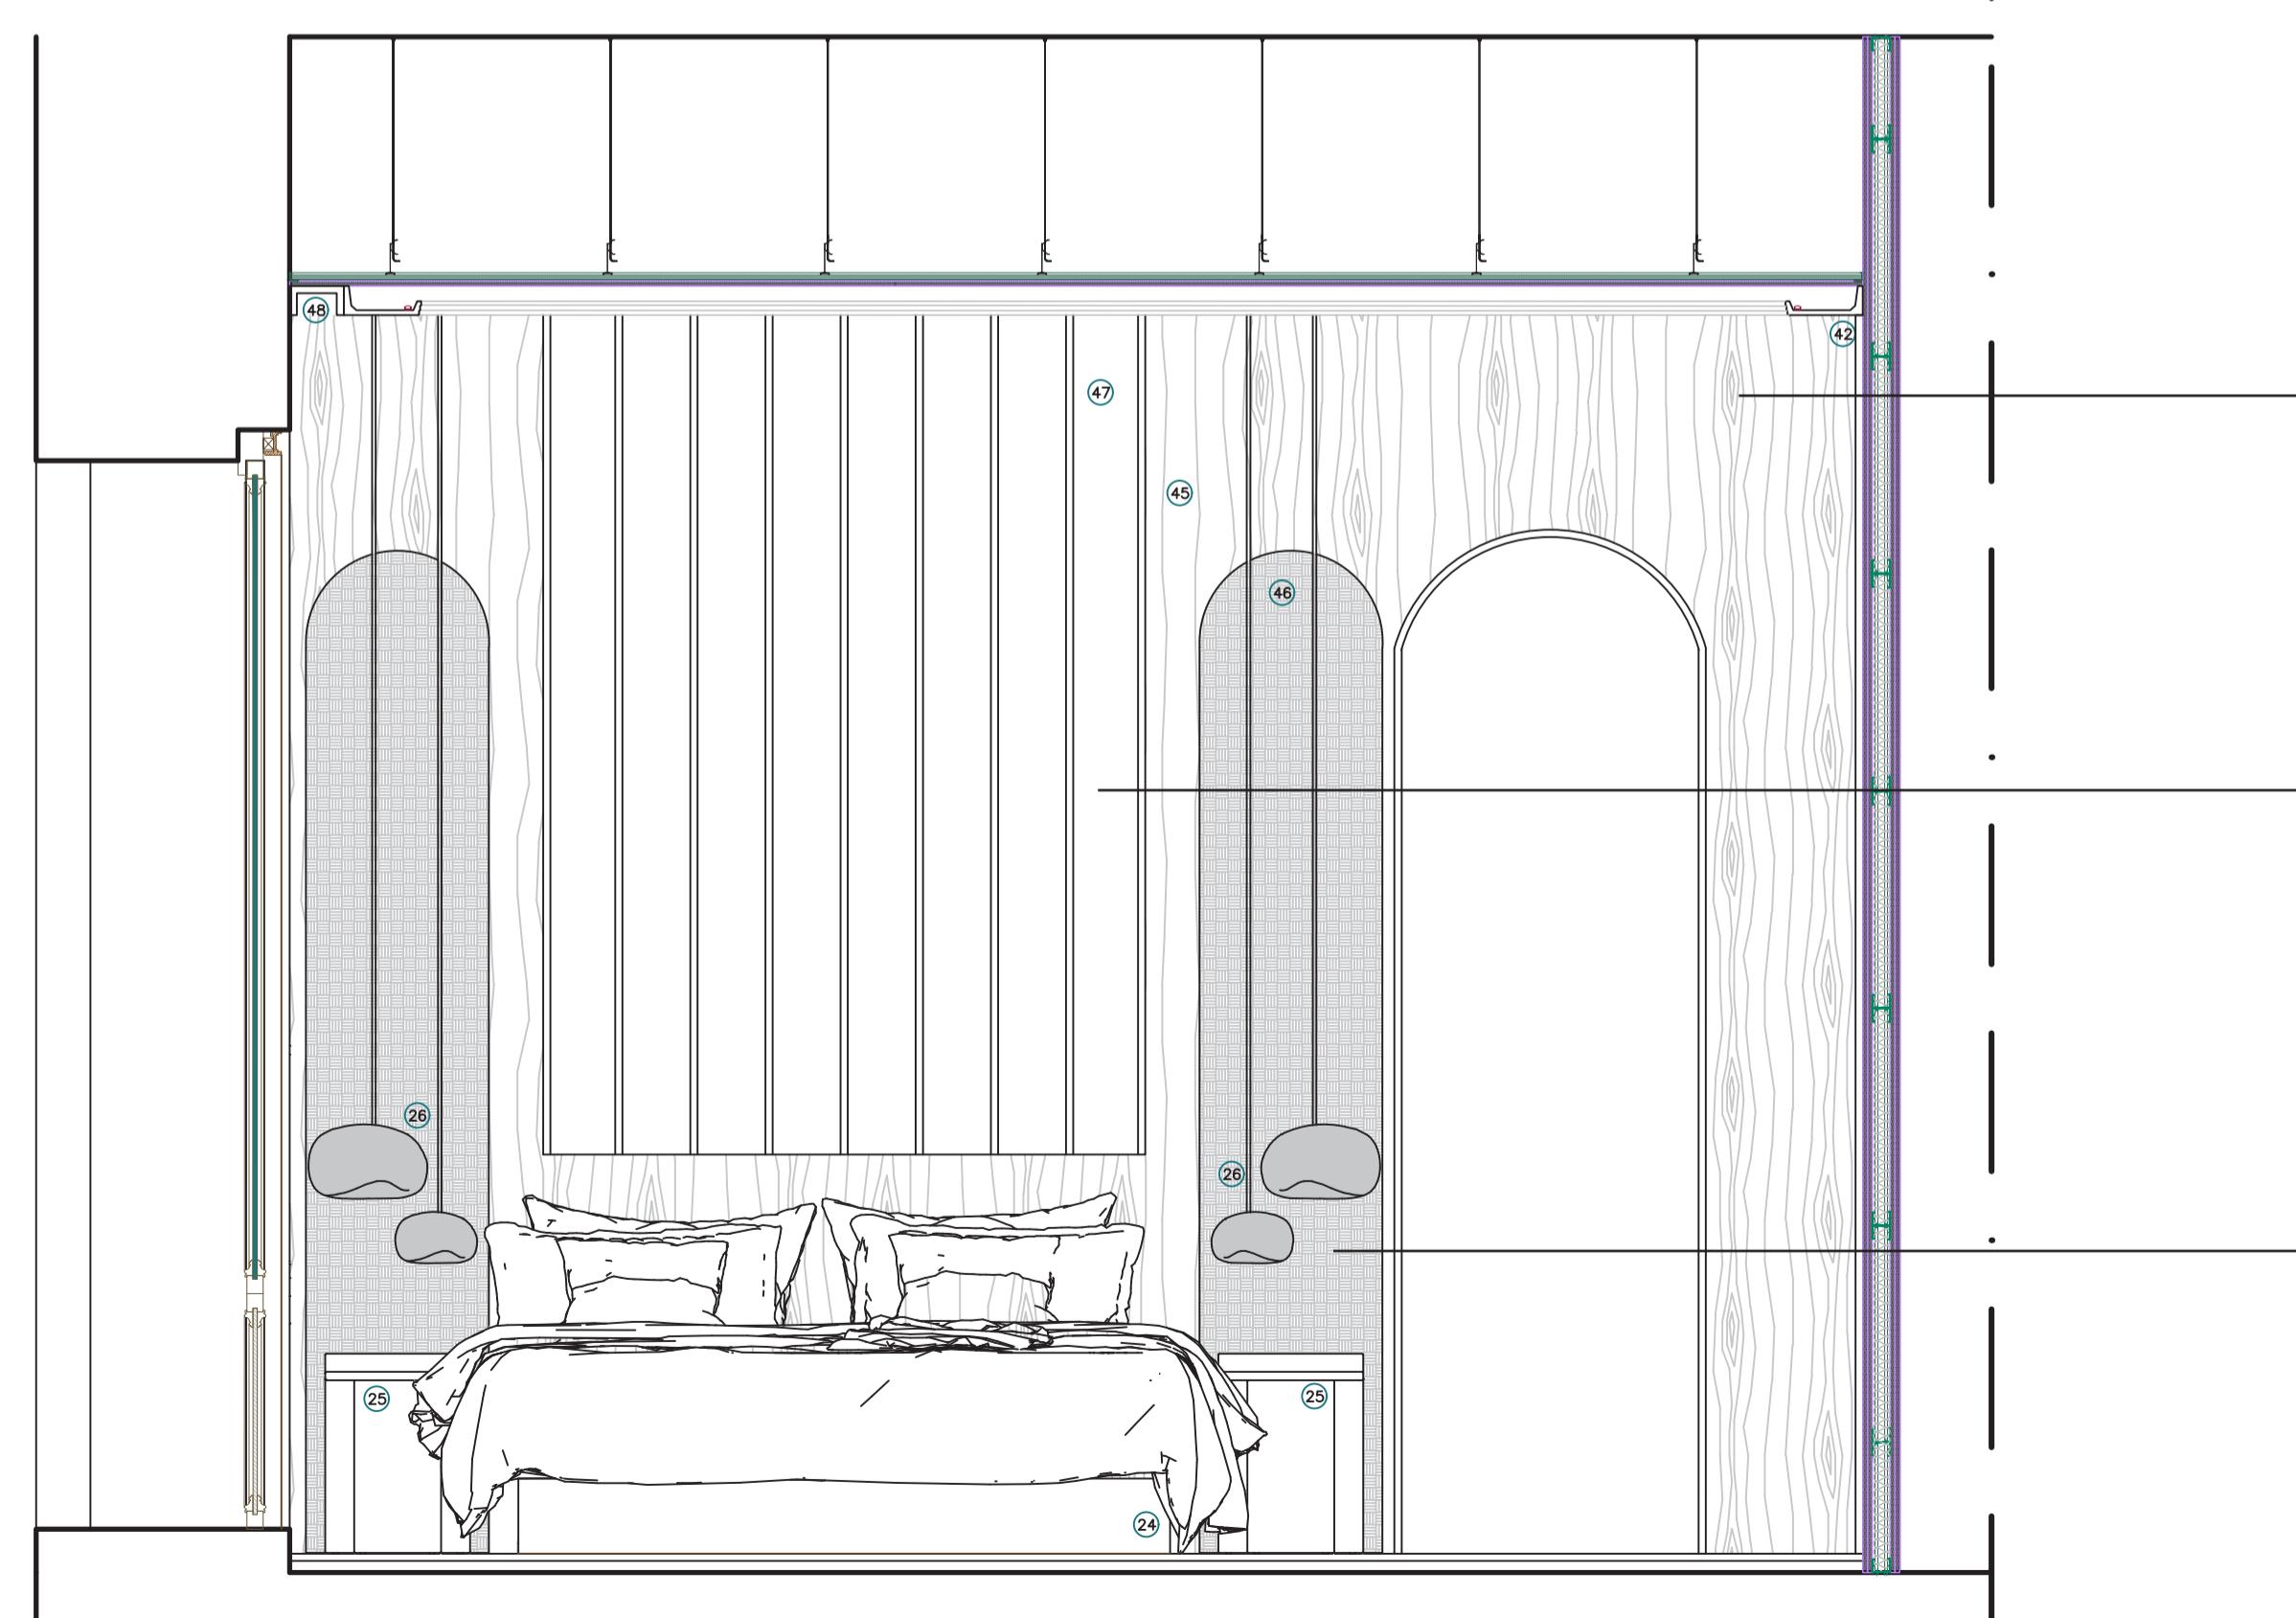

Panneau bois massif
contre plaqué - Columbia
Forest Products - Pure
Bond

PANNEAUX MURAUX CANNELÉS
en platre, effet pierre
naturelle travertin | De-
sign and Visual Concepts

Tissage Cannage | panneau
sur mesure
CMO Paris



Suspension
| Eclat
Azur

Lit 180 x 200cm

Gejst
Side table Ismo dark oak

Sensory Haven

Coupe détaillé chambre

A1- 1/20e

2024


N° XXX

COUPES


Paolo Castelli
Console Kenya



Dressing sur mesure |
Panneau de bois massif
contre plaqué - Columbia
Forest Products - Pure
Bond

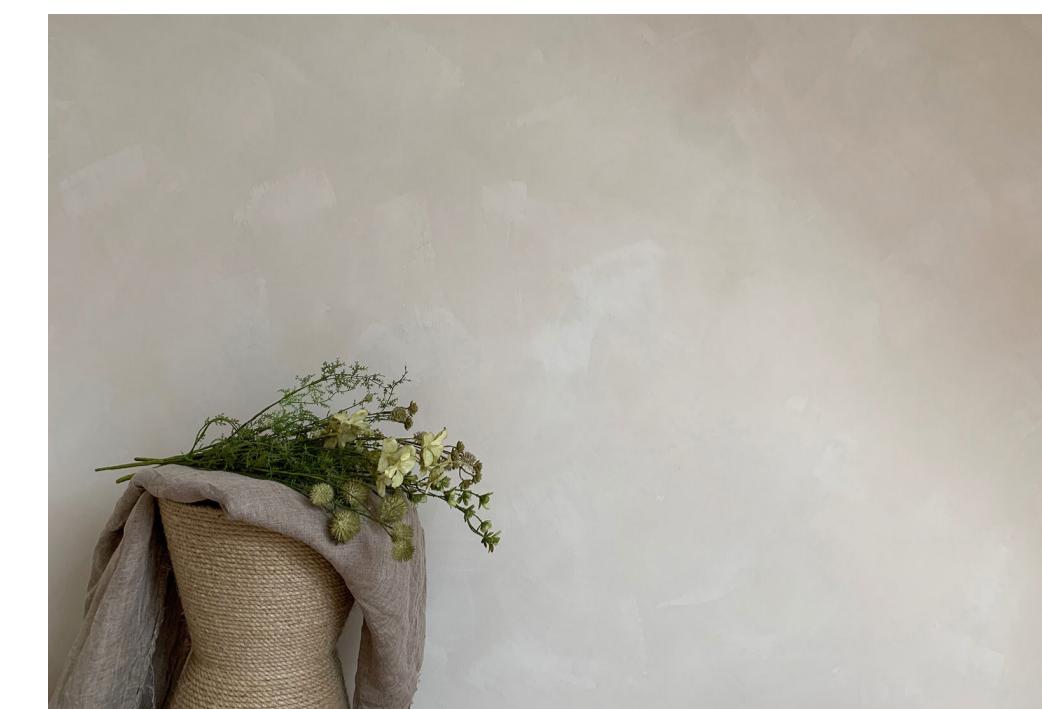

Peinture naturelle à la
chaux | couleur blanc
vieilli

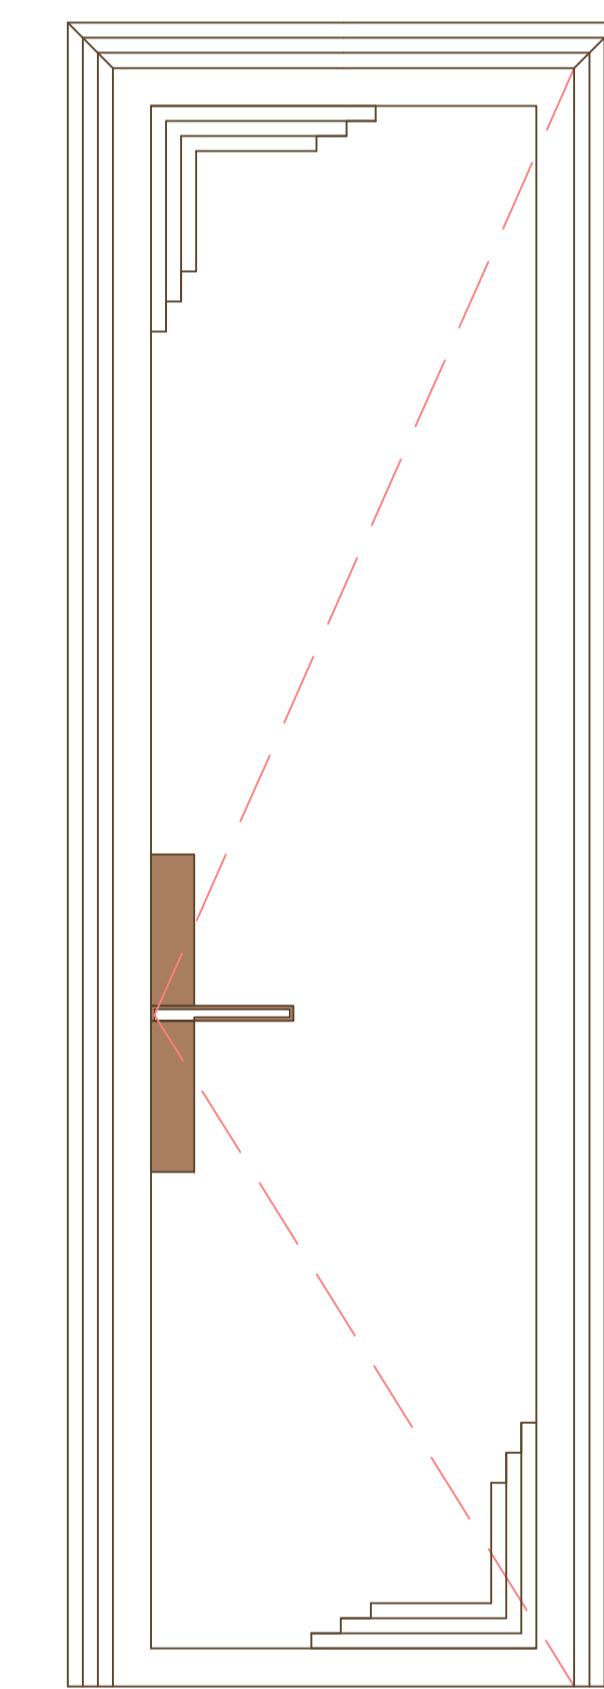

Détail porte
1/10e

I
II
III
IV
V
VI
VII
VIII





Fauteuil - Paolo Castelli
Armchair Vao



Modenature
Coffee table CHAI


PLAN SOL

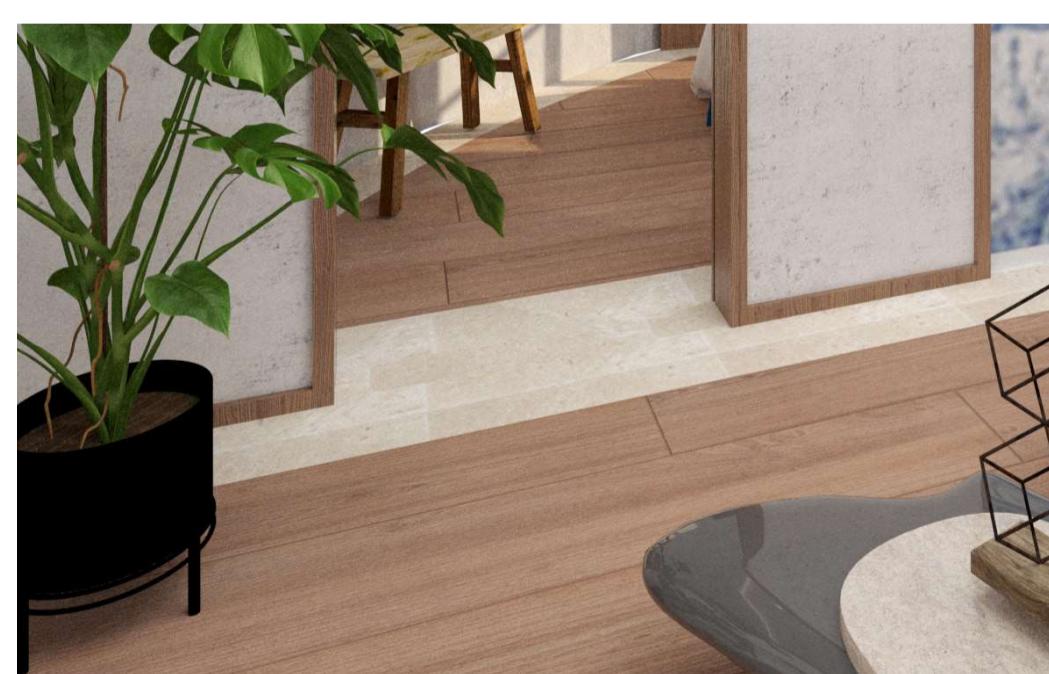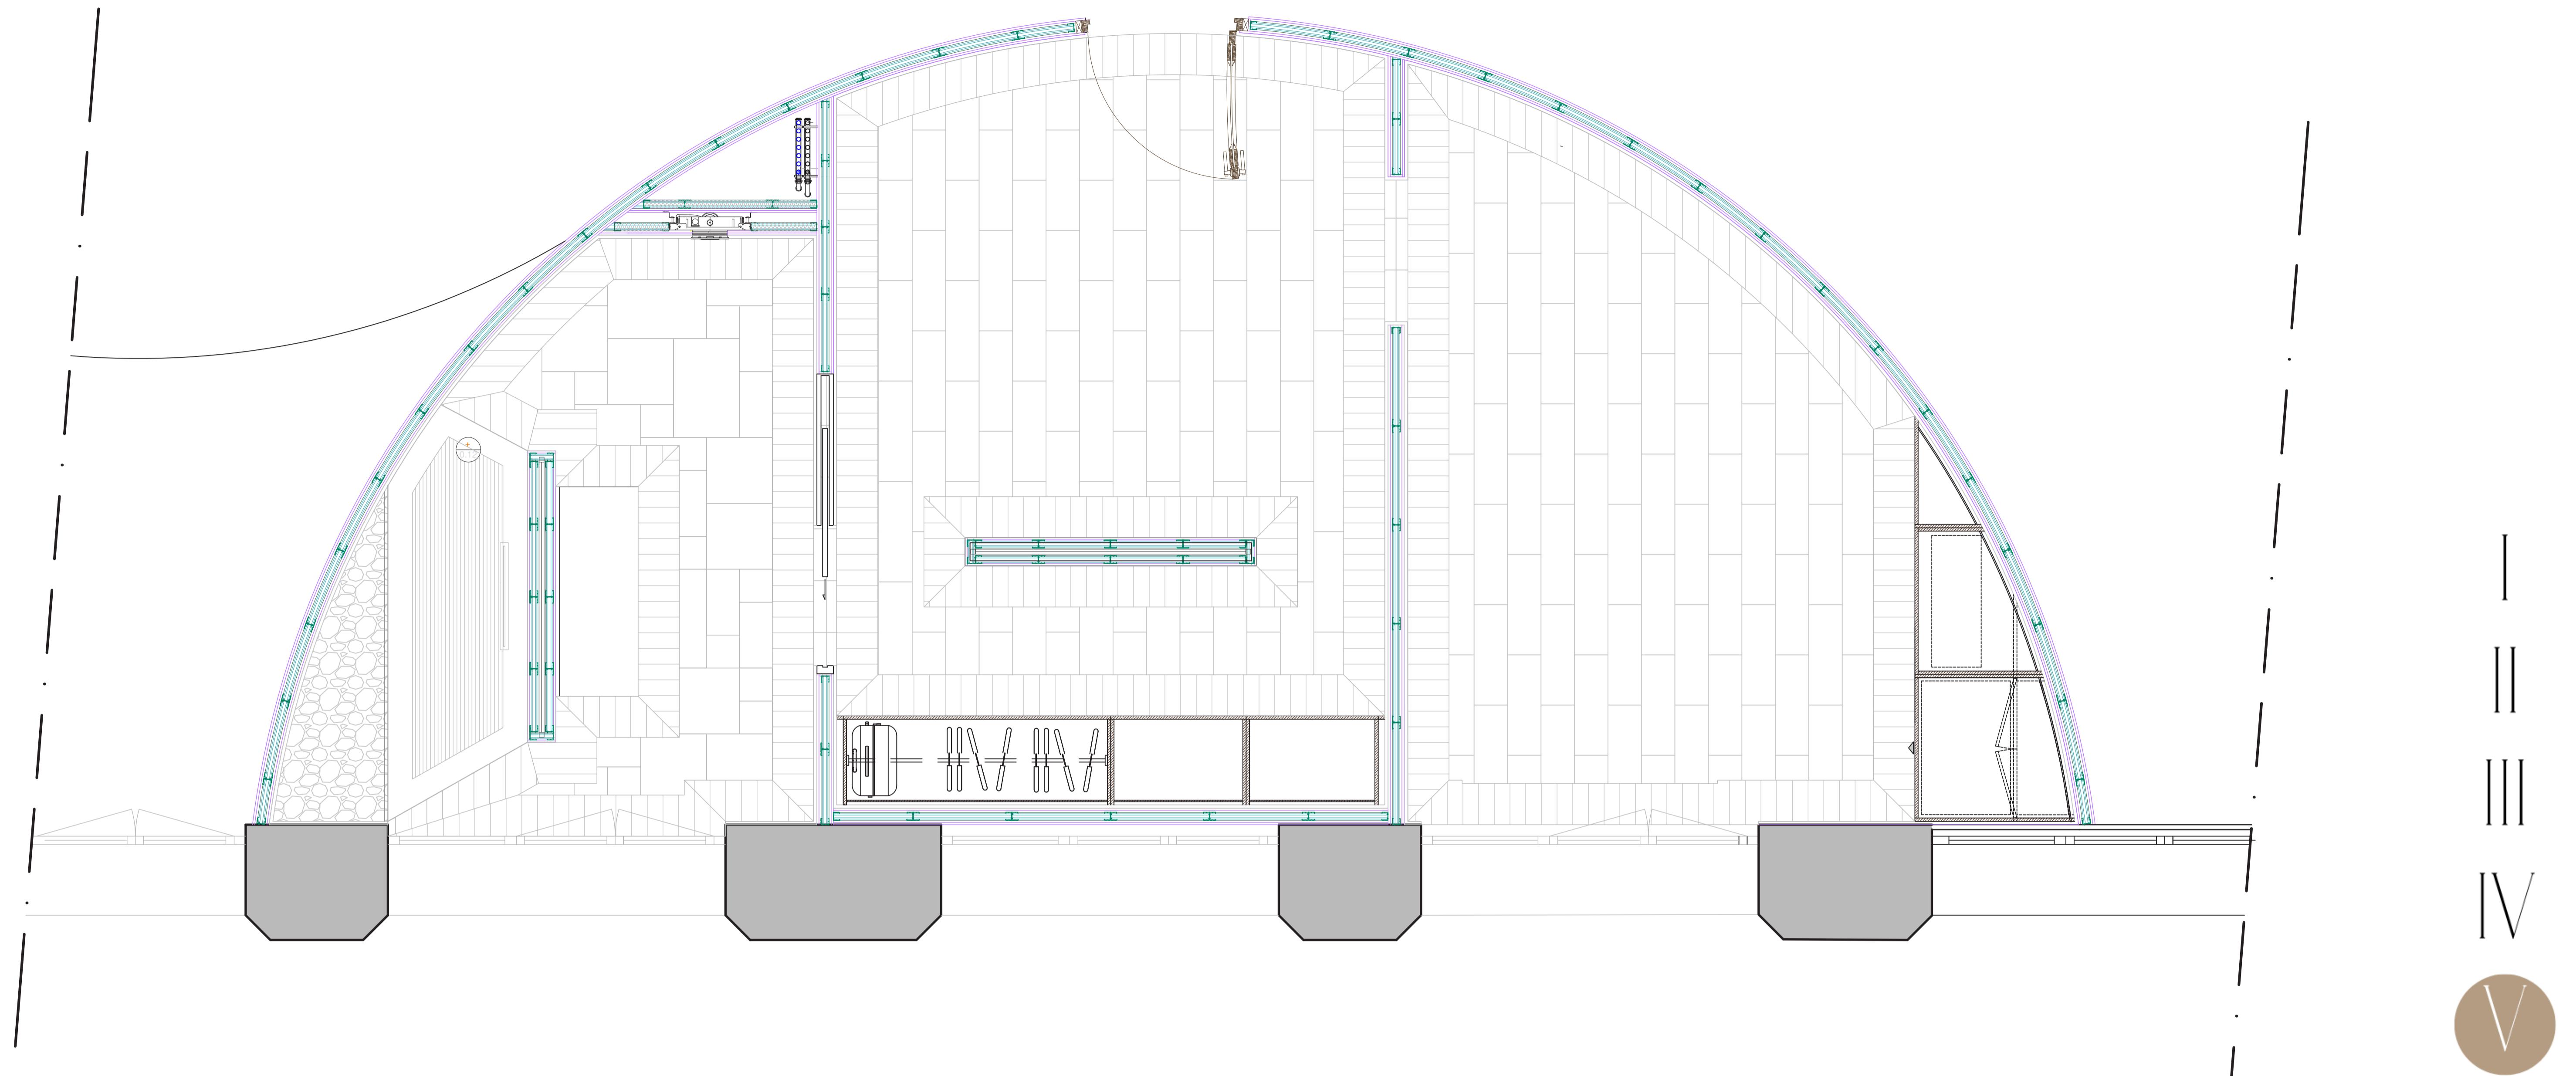


Détail 3D



TRAVERTIN LIGHT MIXTE
CUPASTONE
PAVÉS 10x25 cm

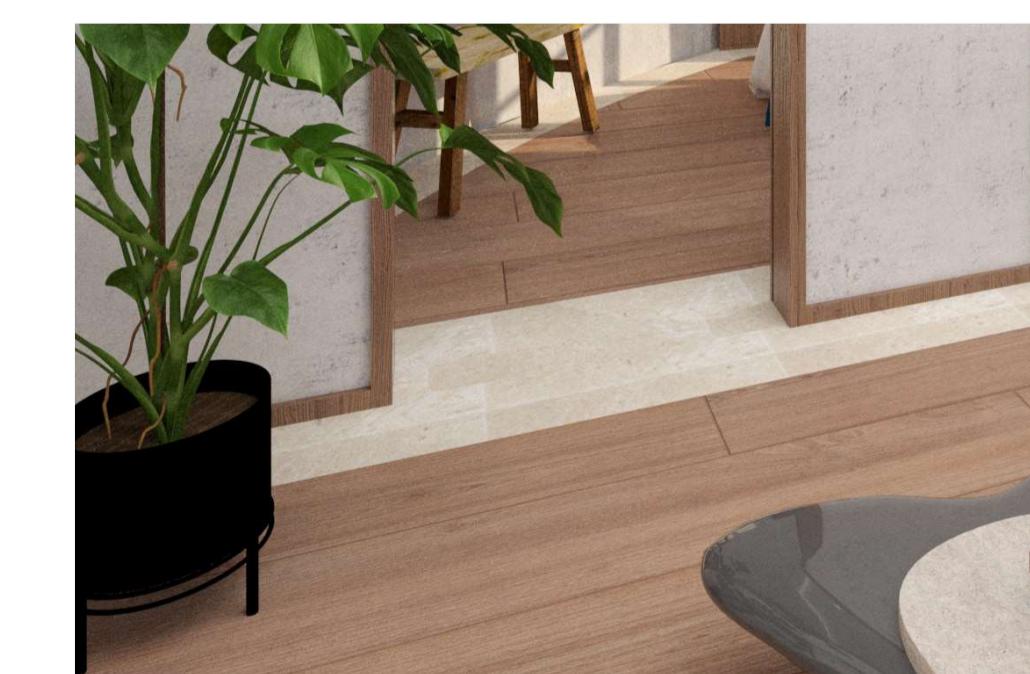

Parquet Carrésol | Chêne
semi massif, vanille -
ref: 00602318016

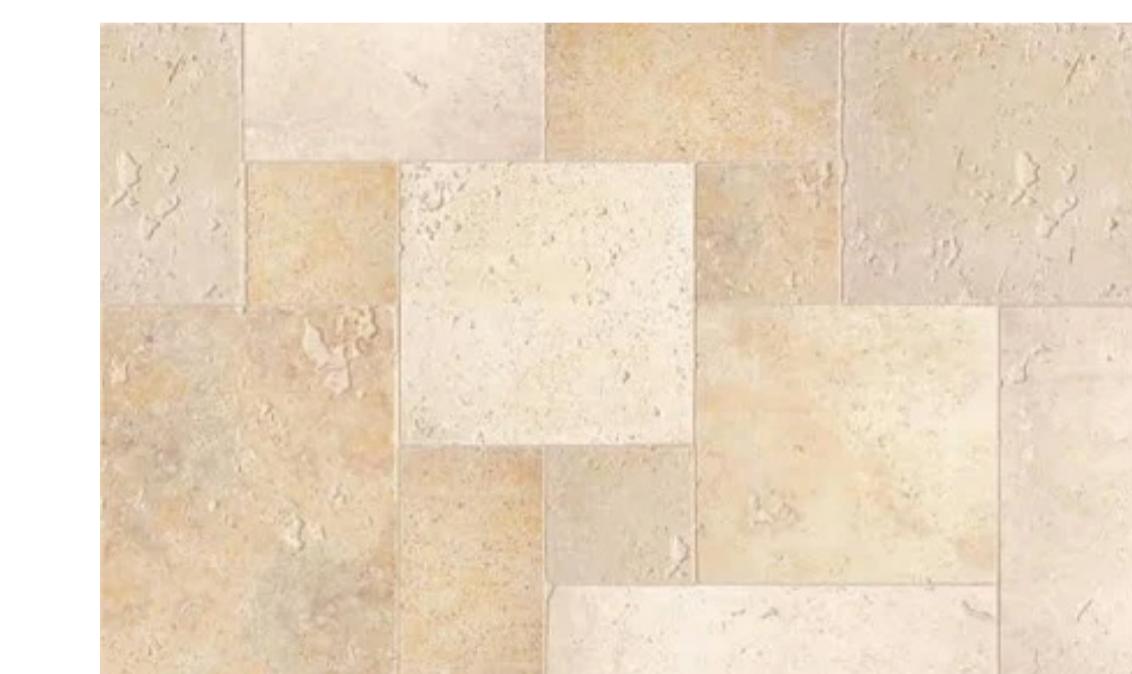


CUPASTONE PIERRES DISTRI-
BUTION
Dallage sol travertin -
light mix - opus 4 for-
mats, ref: Pointp4190321


PLAN PLAFOND




CORNICHE À ÉCLAIRAGE INDIRECT - STAFF DÉCOR - D104

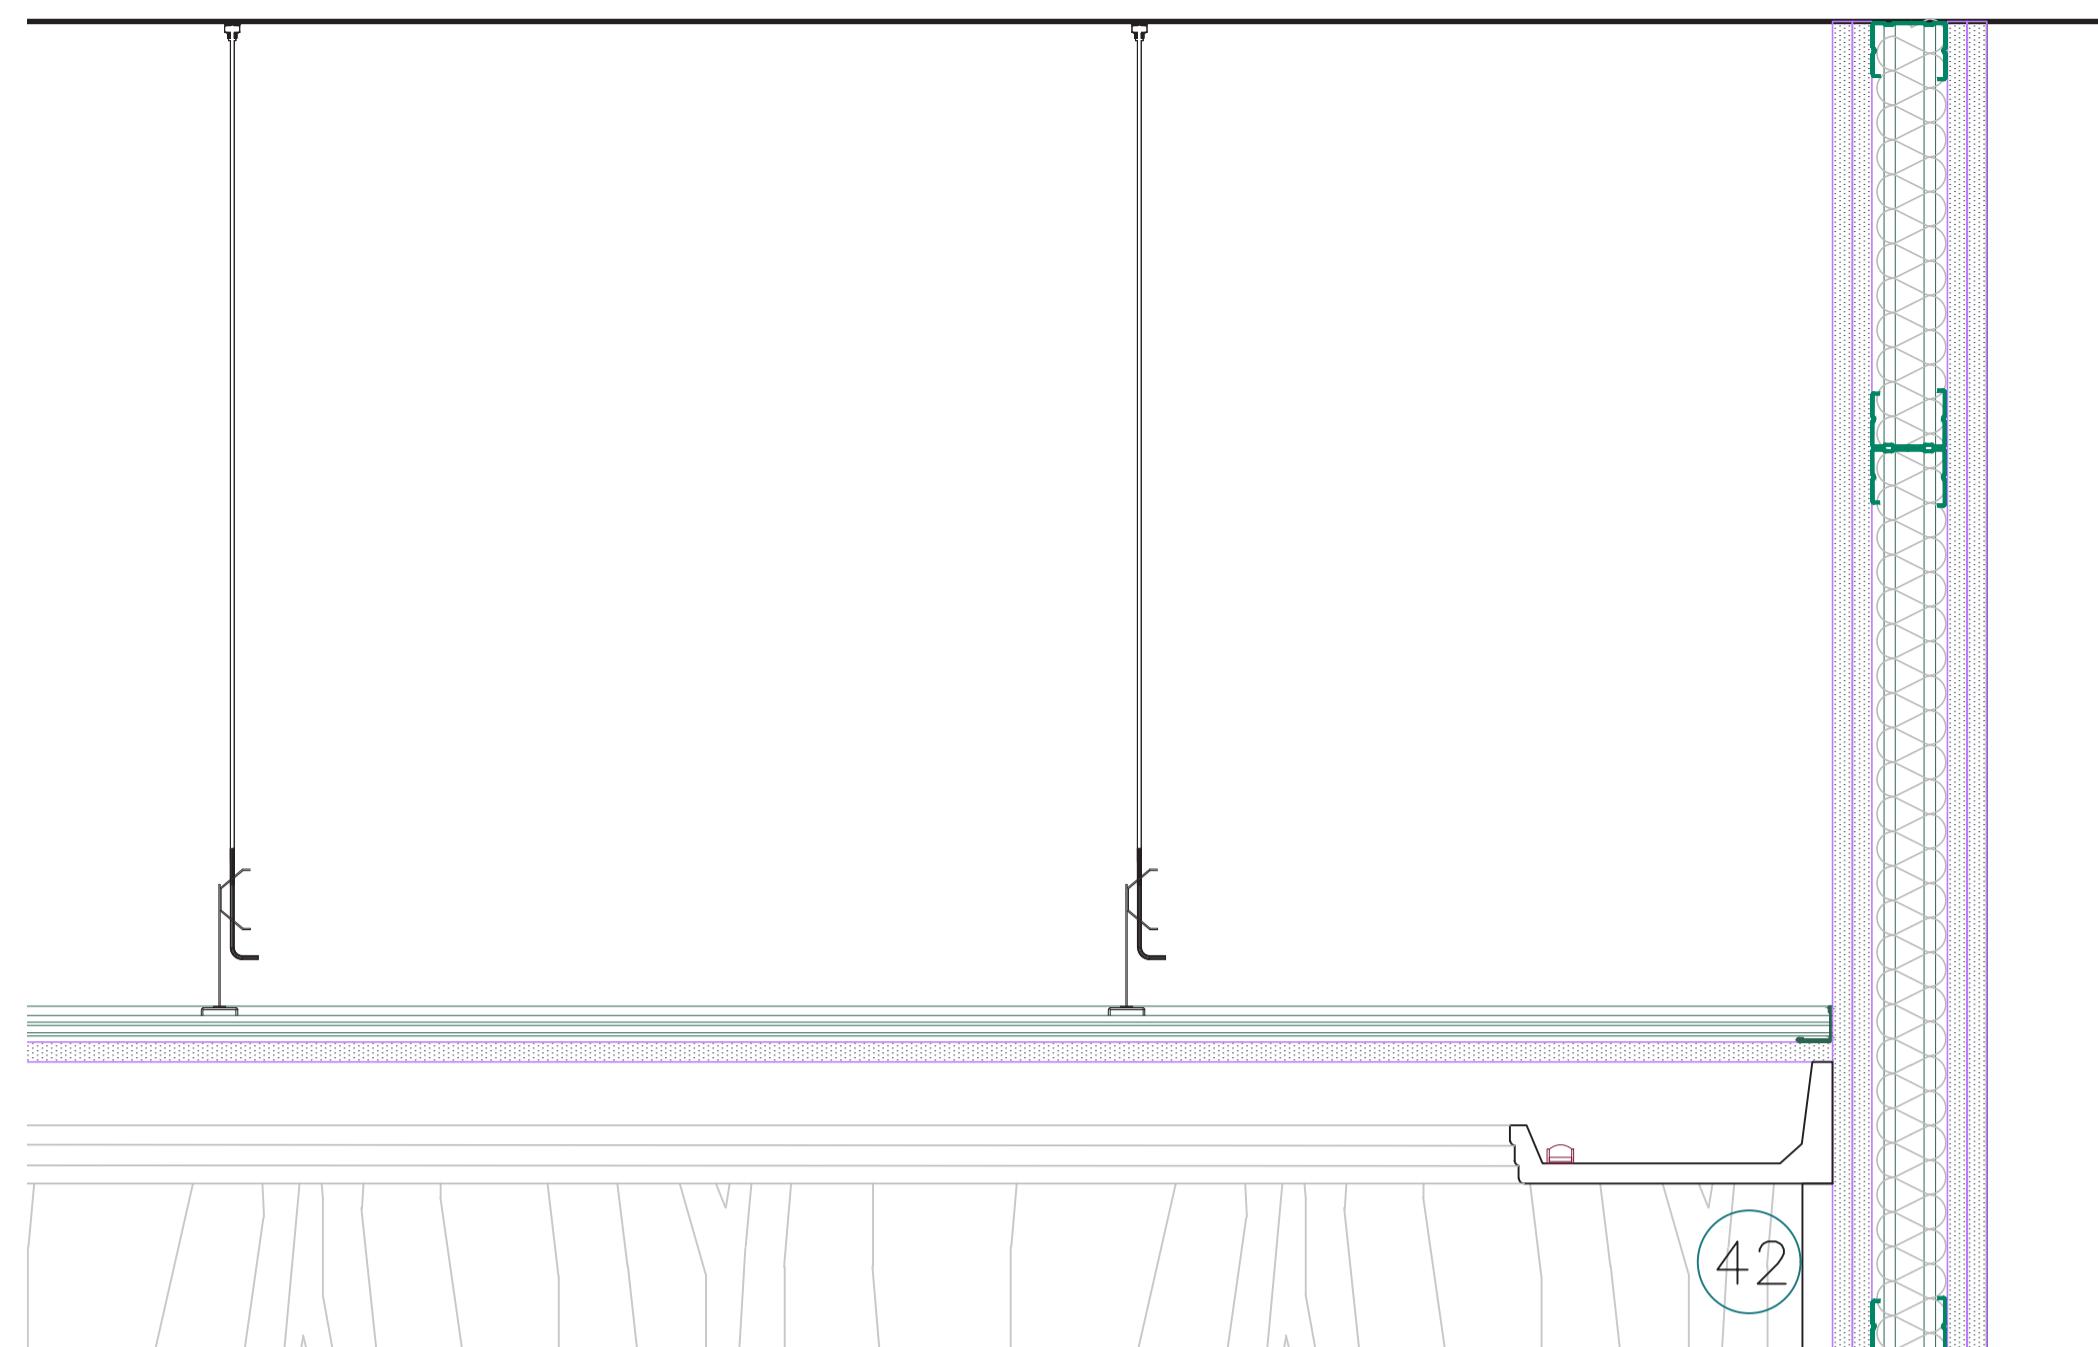


DÉTAIL FAUX PLAFOND SUSPENDU
1/5E

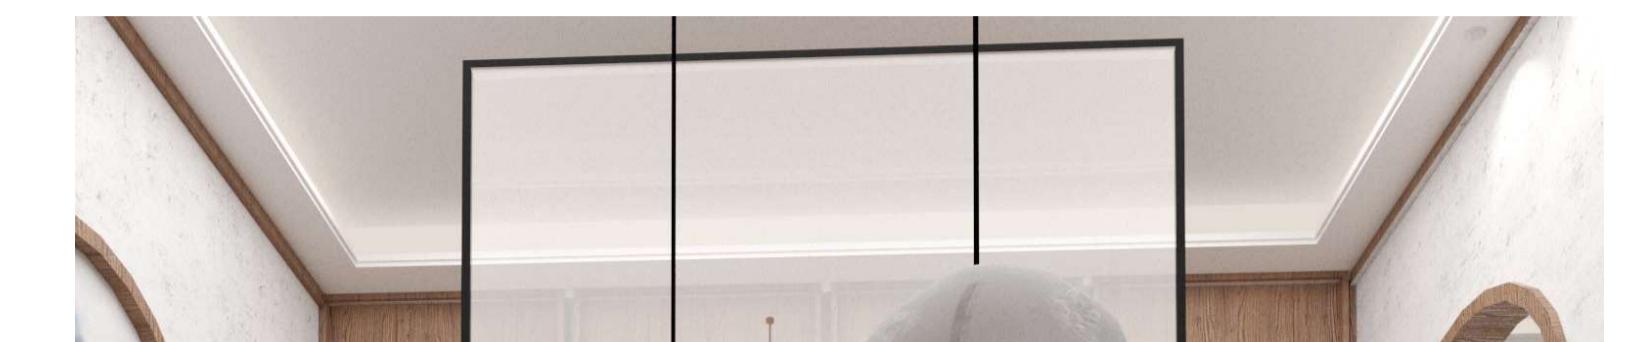

DÉTAIL 3D

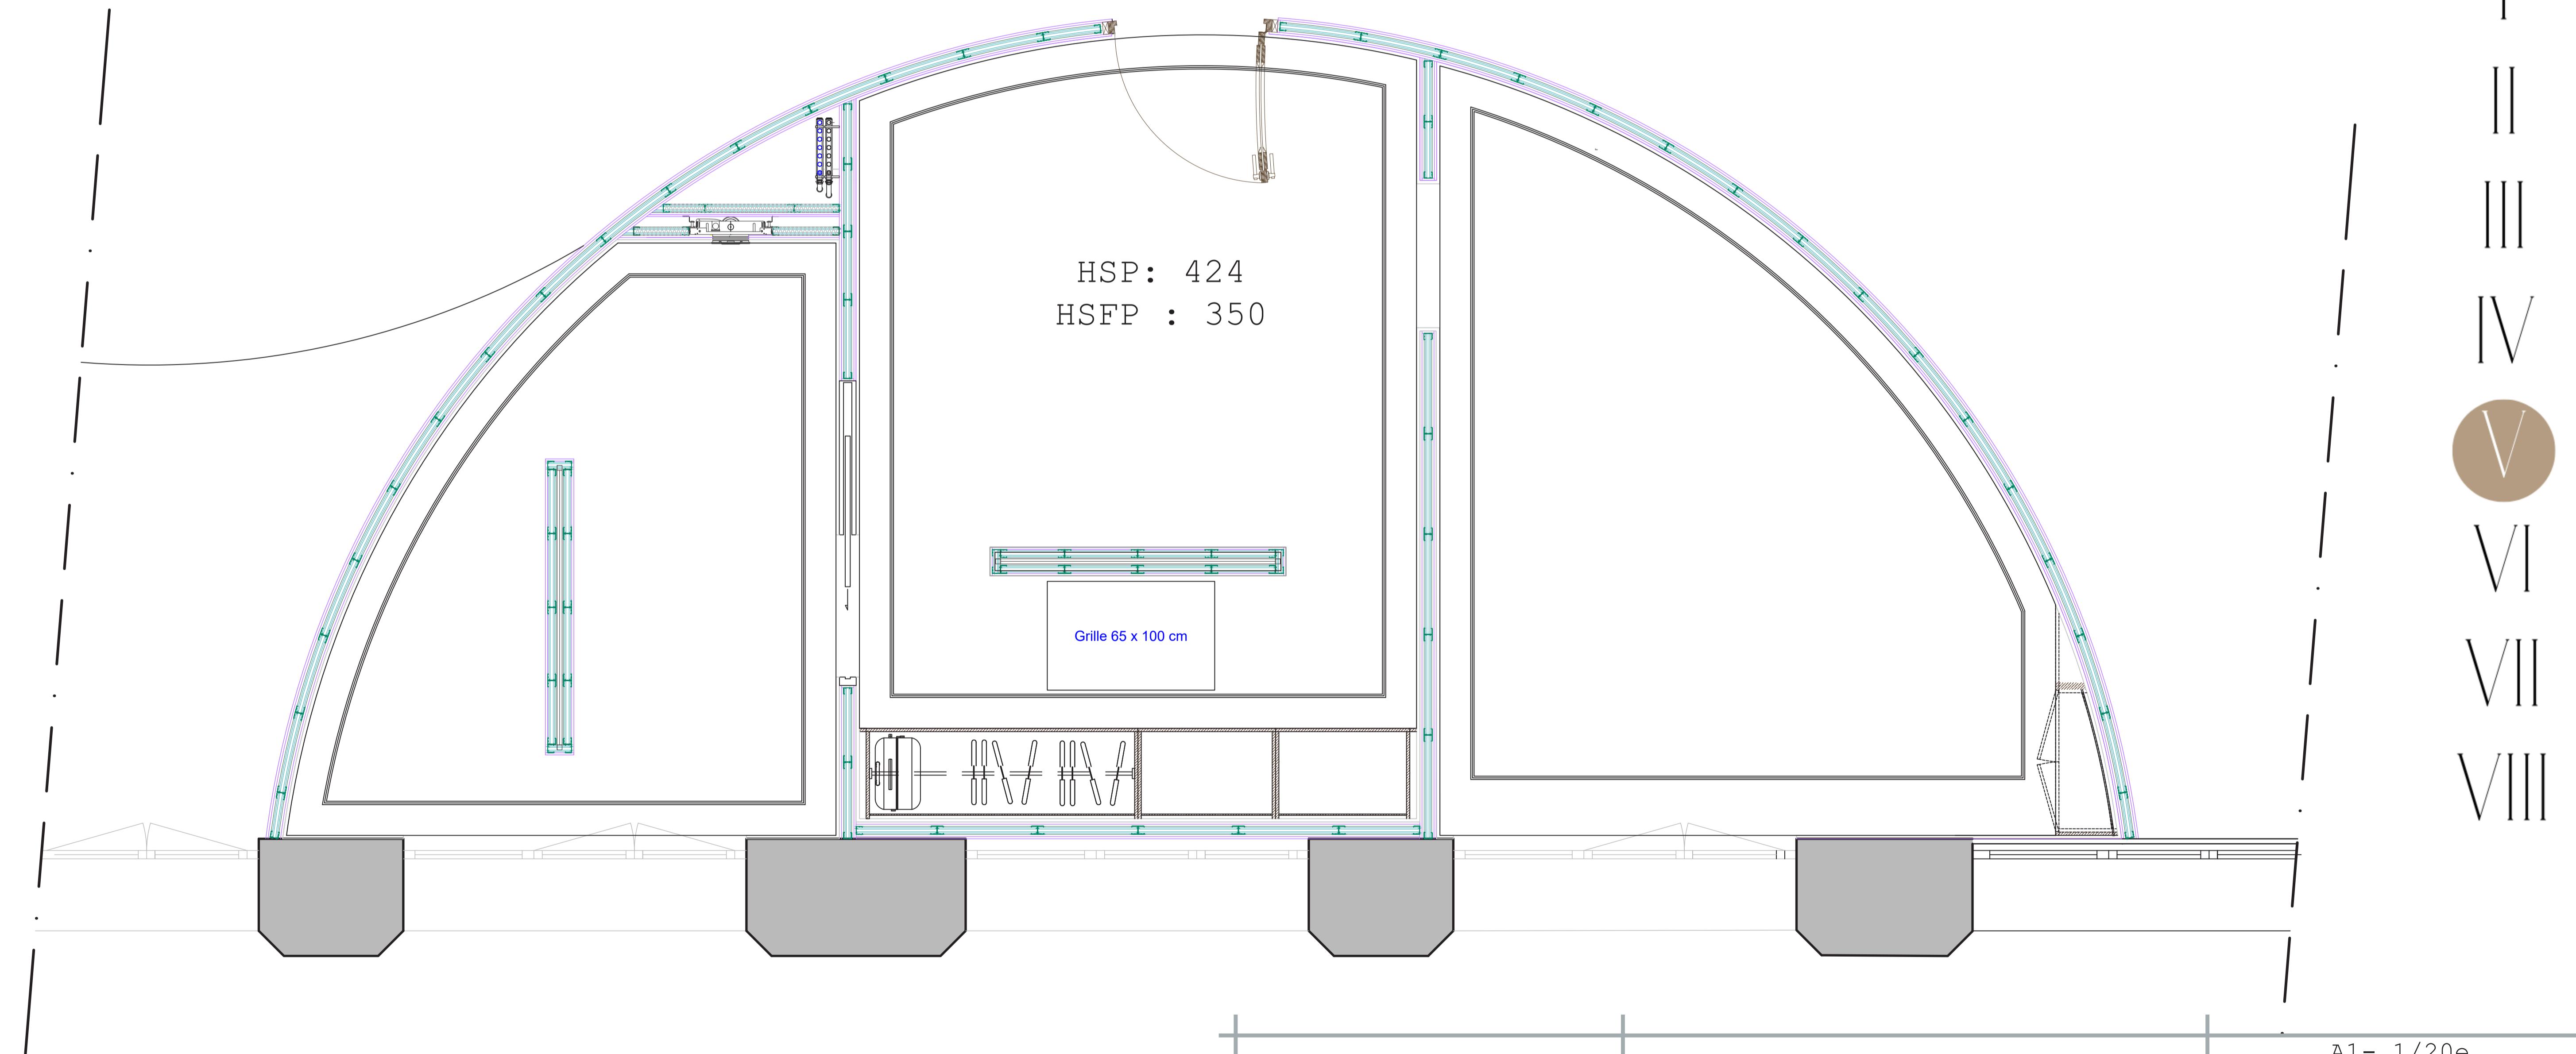


PLAN ELECTRIQUE

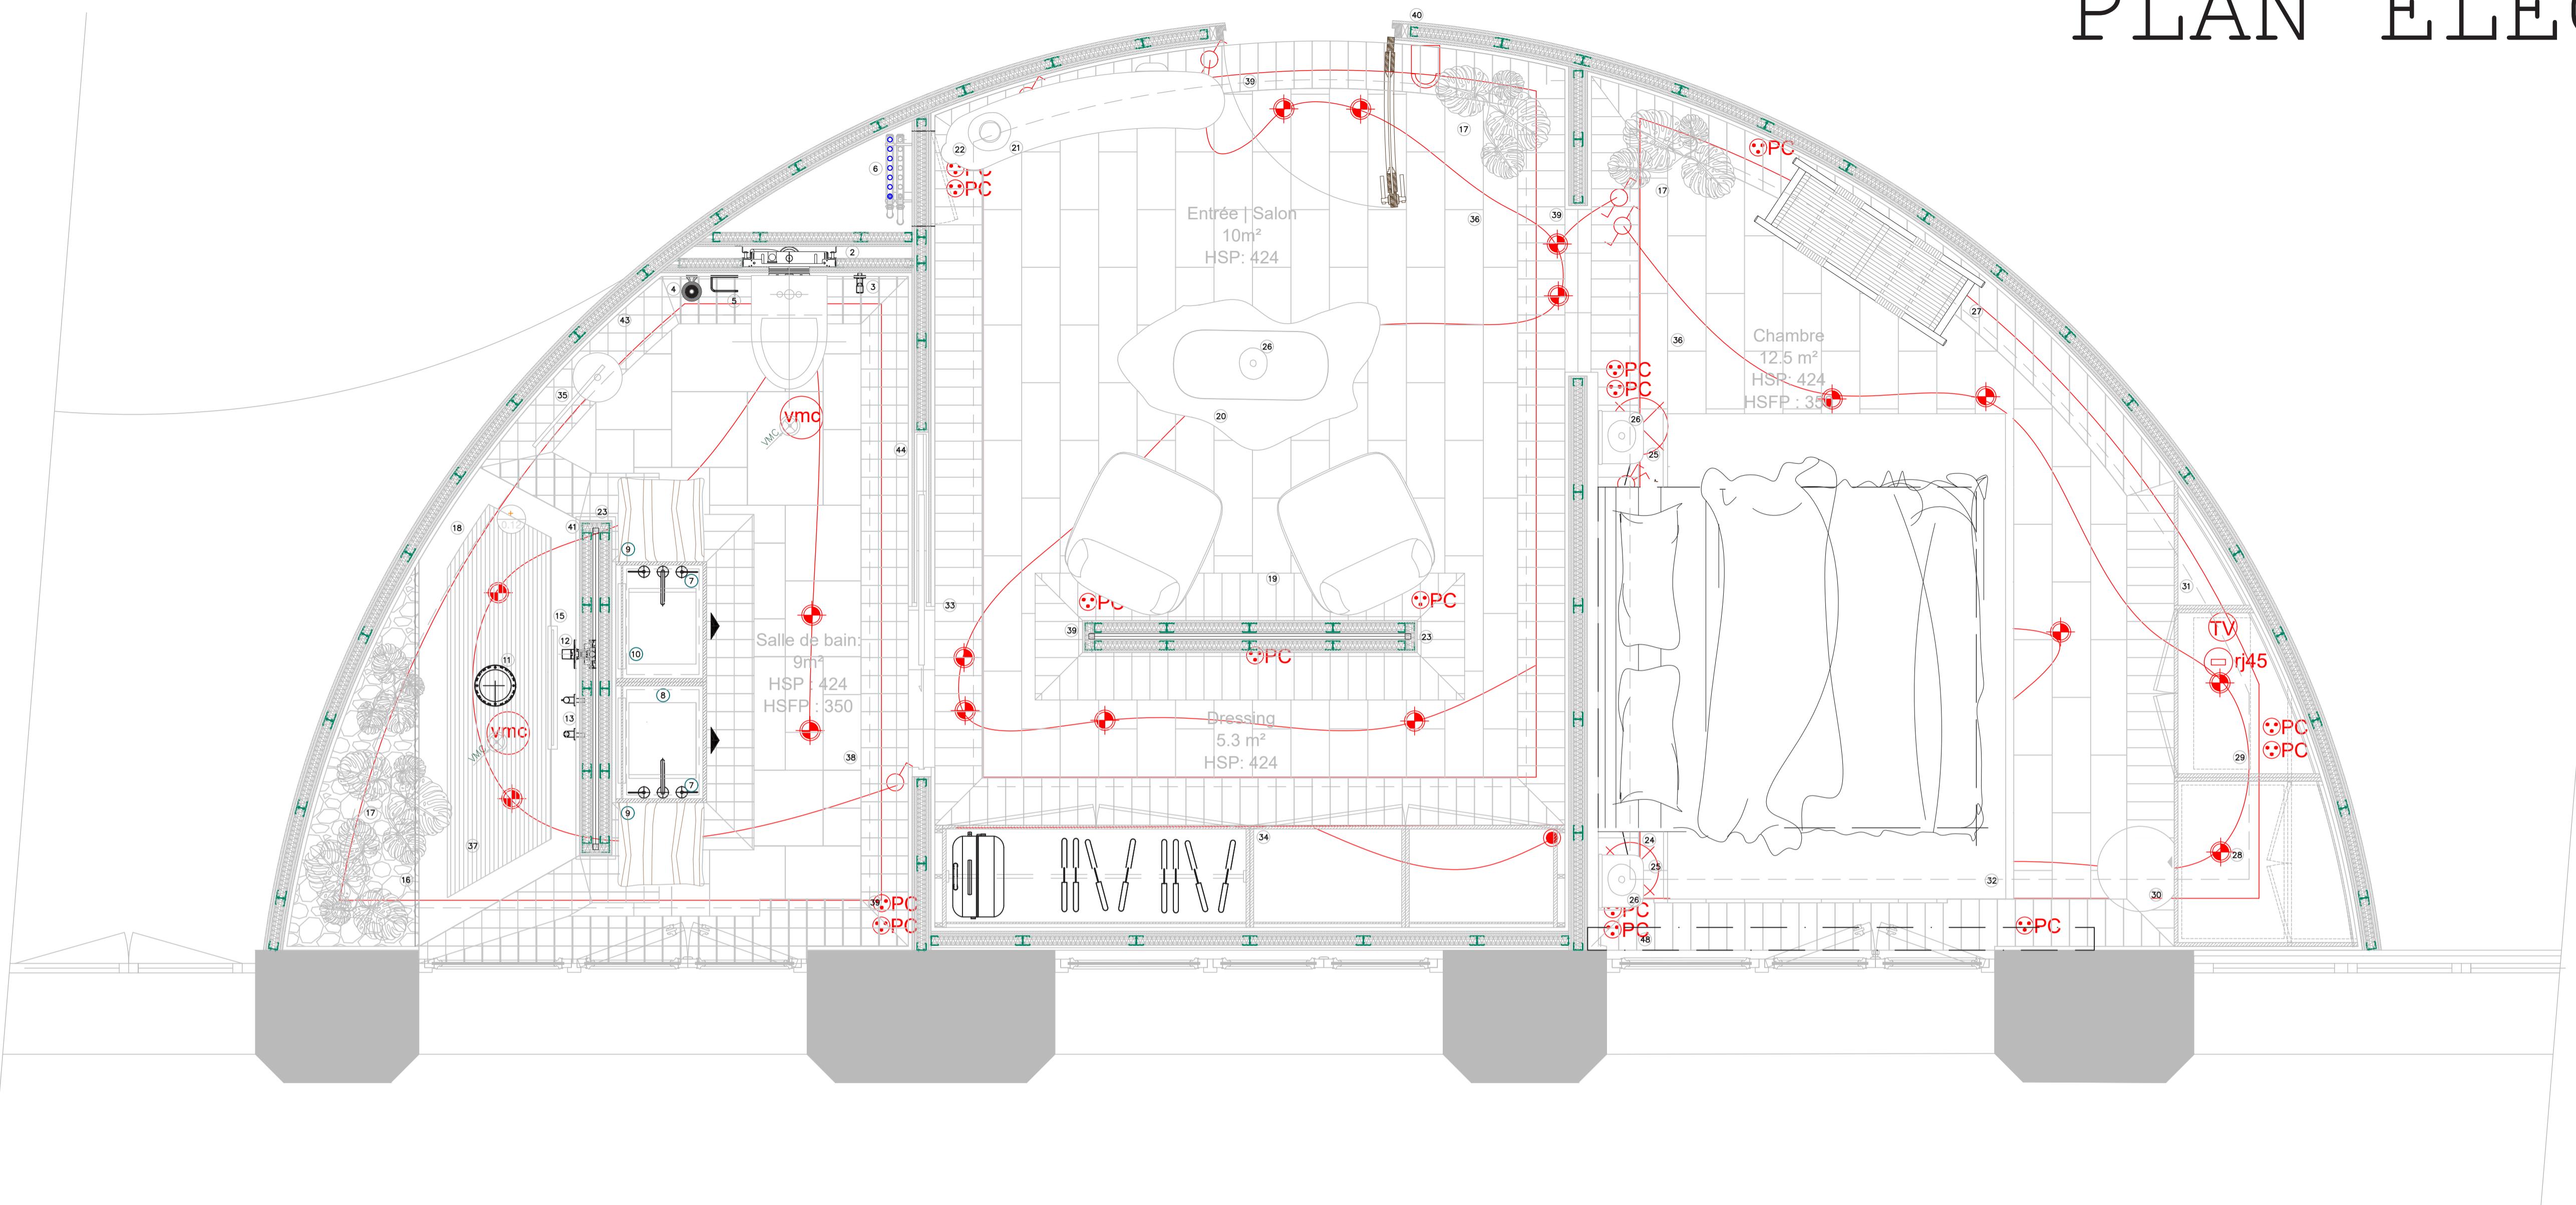

LEGENDE SYMBOLES ELECTRIQUES

liaison de terre	Pot de centre	Détecteur élec	four	Prise de courant four
Sonnette	Applique	Interrupteur	lv	Prise de courant lave vaisselle
Bouton sonnette	Spot encastré	Double interrupteur	LL	Prise de courant lave linge
Prise téléphone	Spot au sol	Va et vient	pe	Prise de courant plaque électrique
Prise télévision	Néon	VR Inter. volet roulant	fg	Prise de courant réfrigérateur
Prise RJ45	Ruban LED	Prise de courant	C	Interrupteur changement couleur
Ventilation Mécanique Contrôlée	Sortie de fils	Prise de courant commandée		
Interrupteur - variateur	Camera vidéo	interrupteur - détecteur de présence		
Tableau électrique				
Détecteur mouvement				

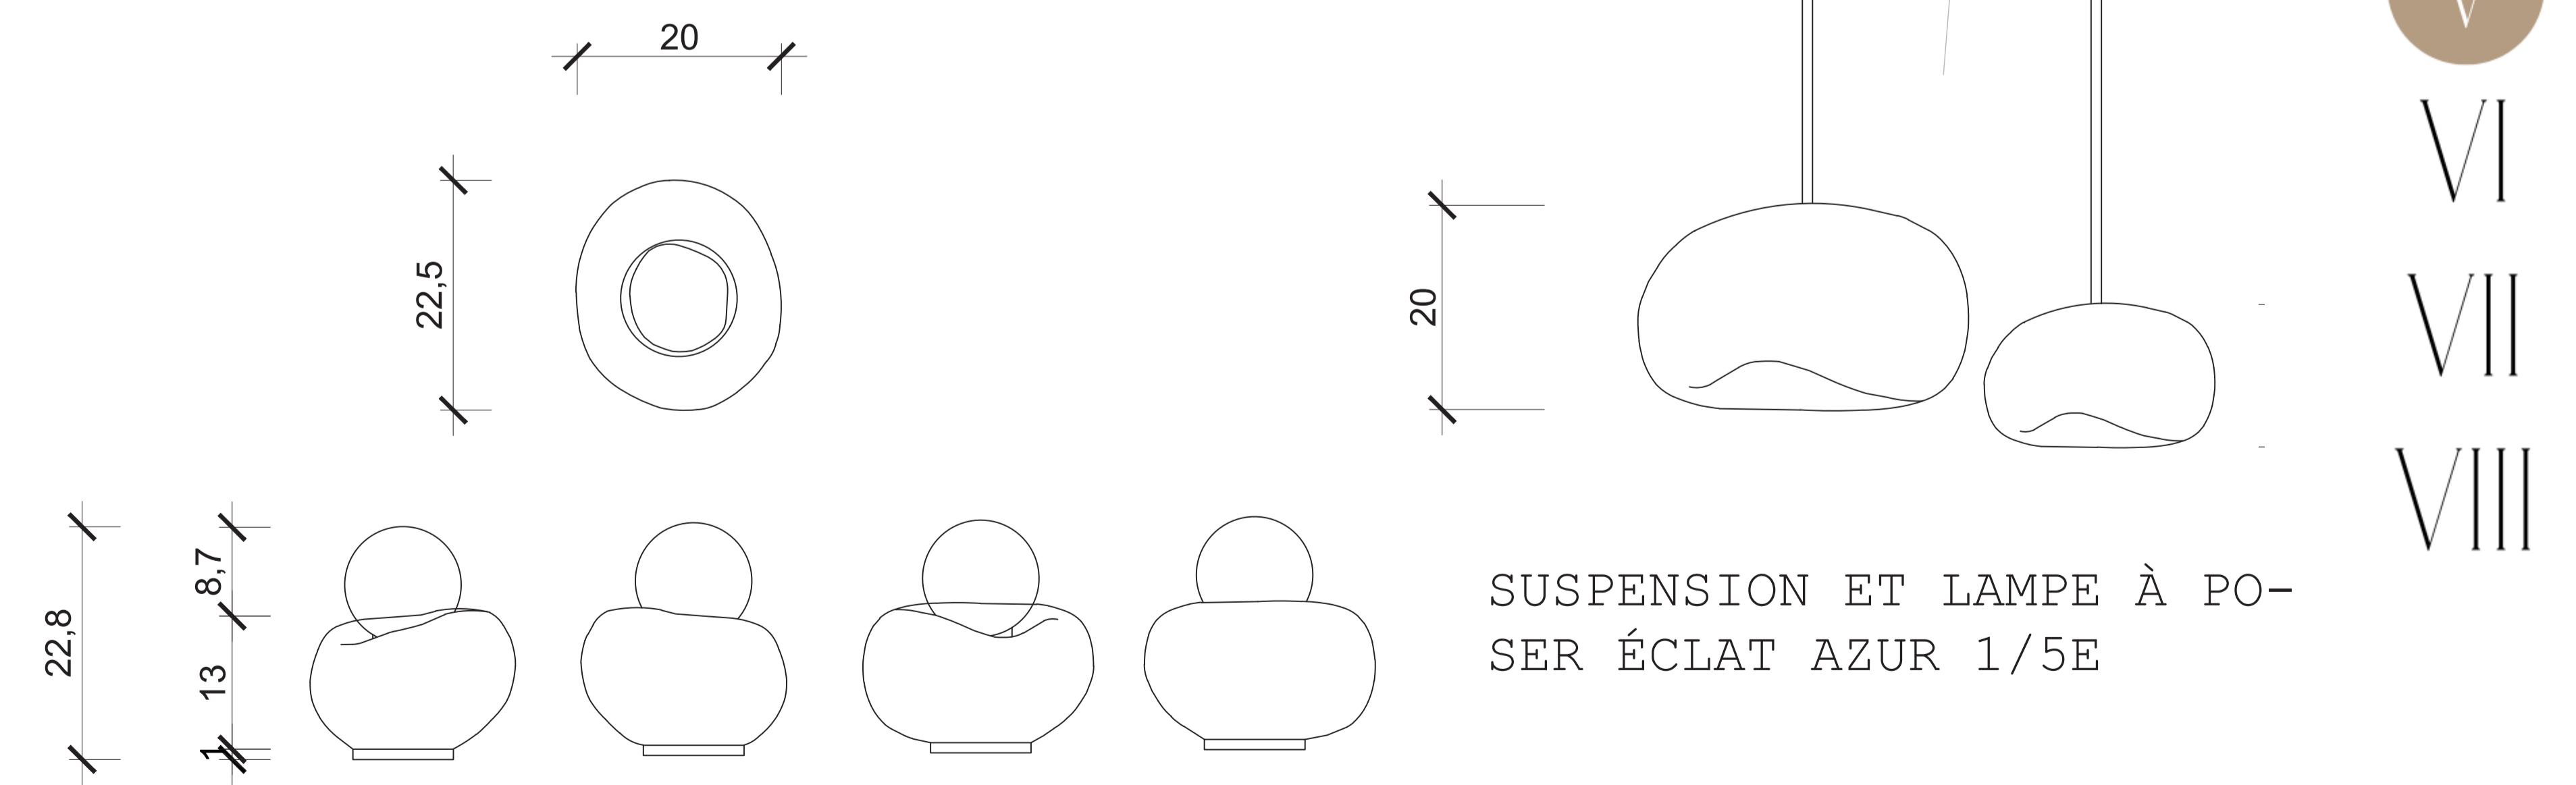


PLAN CLIME


UTILISATION D'UN GAINABLE COMPACT

Installer un gainable compact dans une chambre d'hôtel offre plusieurs avantages : discrétion, fonctionnement silencieux, efficacité énergétique, confort thermique uniforme, contrôle individuel de la température et maintenance simplifiée.

Ces atouts contribuent à améliorer le confort et la satisfaction des clients tout en réduisant les coûts d'exploitation et d'entretien pour l'hôtel.

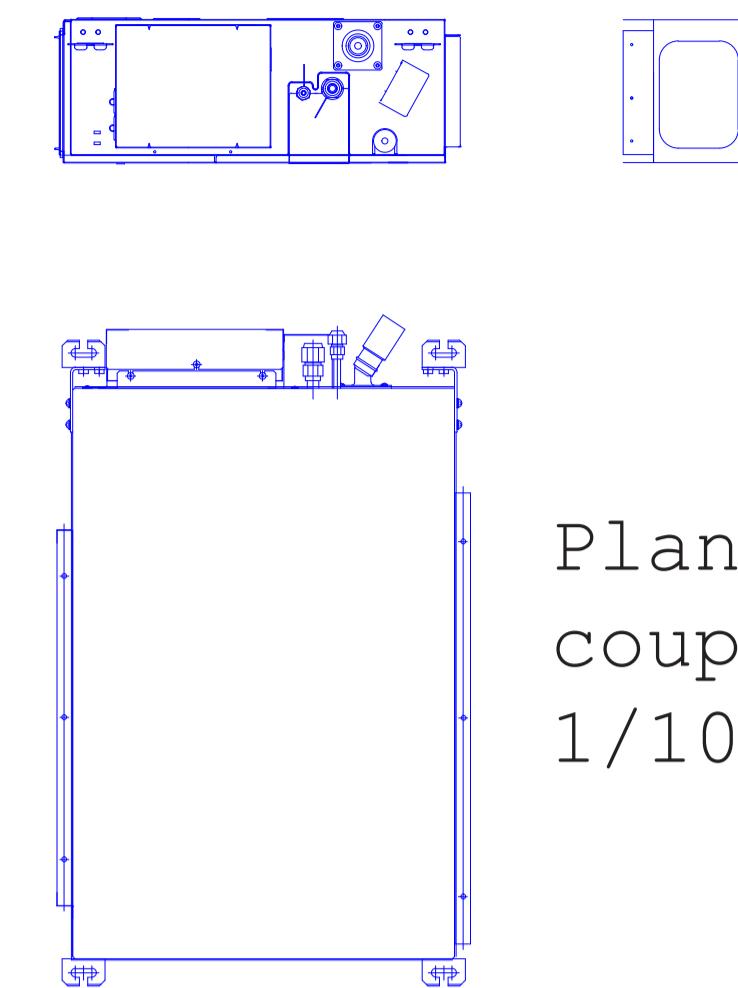


Un système de soufflage en sous face est utilisé pour combiner discrétion, silence, efficacité et confort, faisant de lui une excellente option.

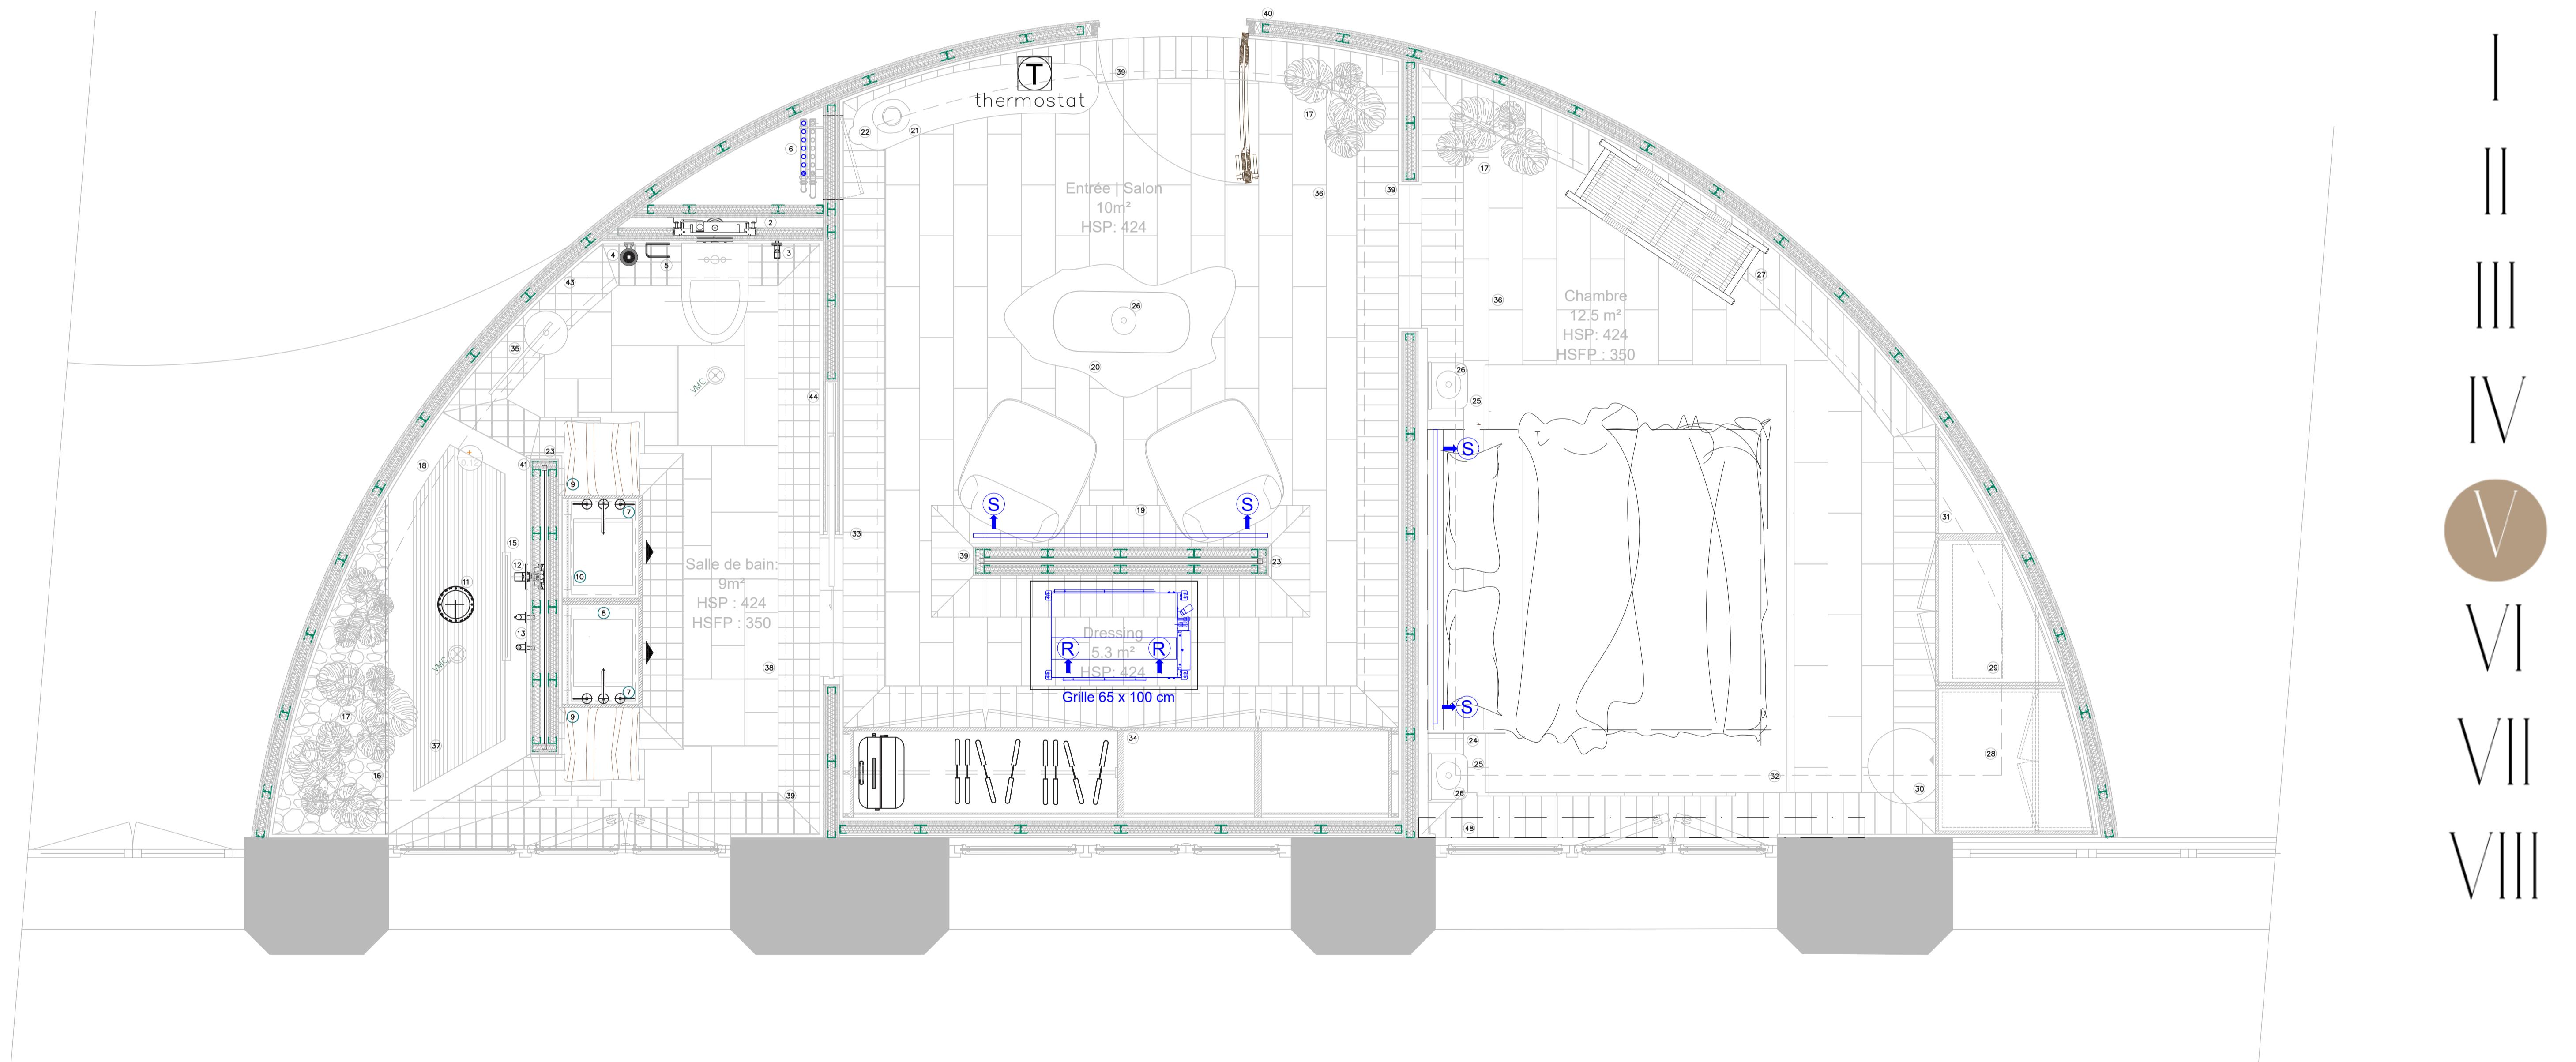

PLAN PLOMBERIE

- EVACUATION ET RACCORD
- ALIMENTATION EAU FROIDE
- ALIMENTATION EAU CHAUEDE

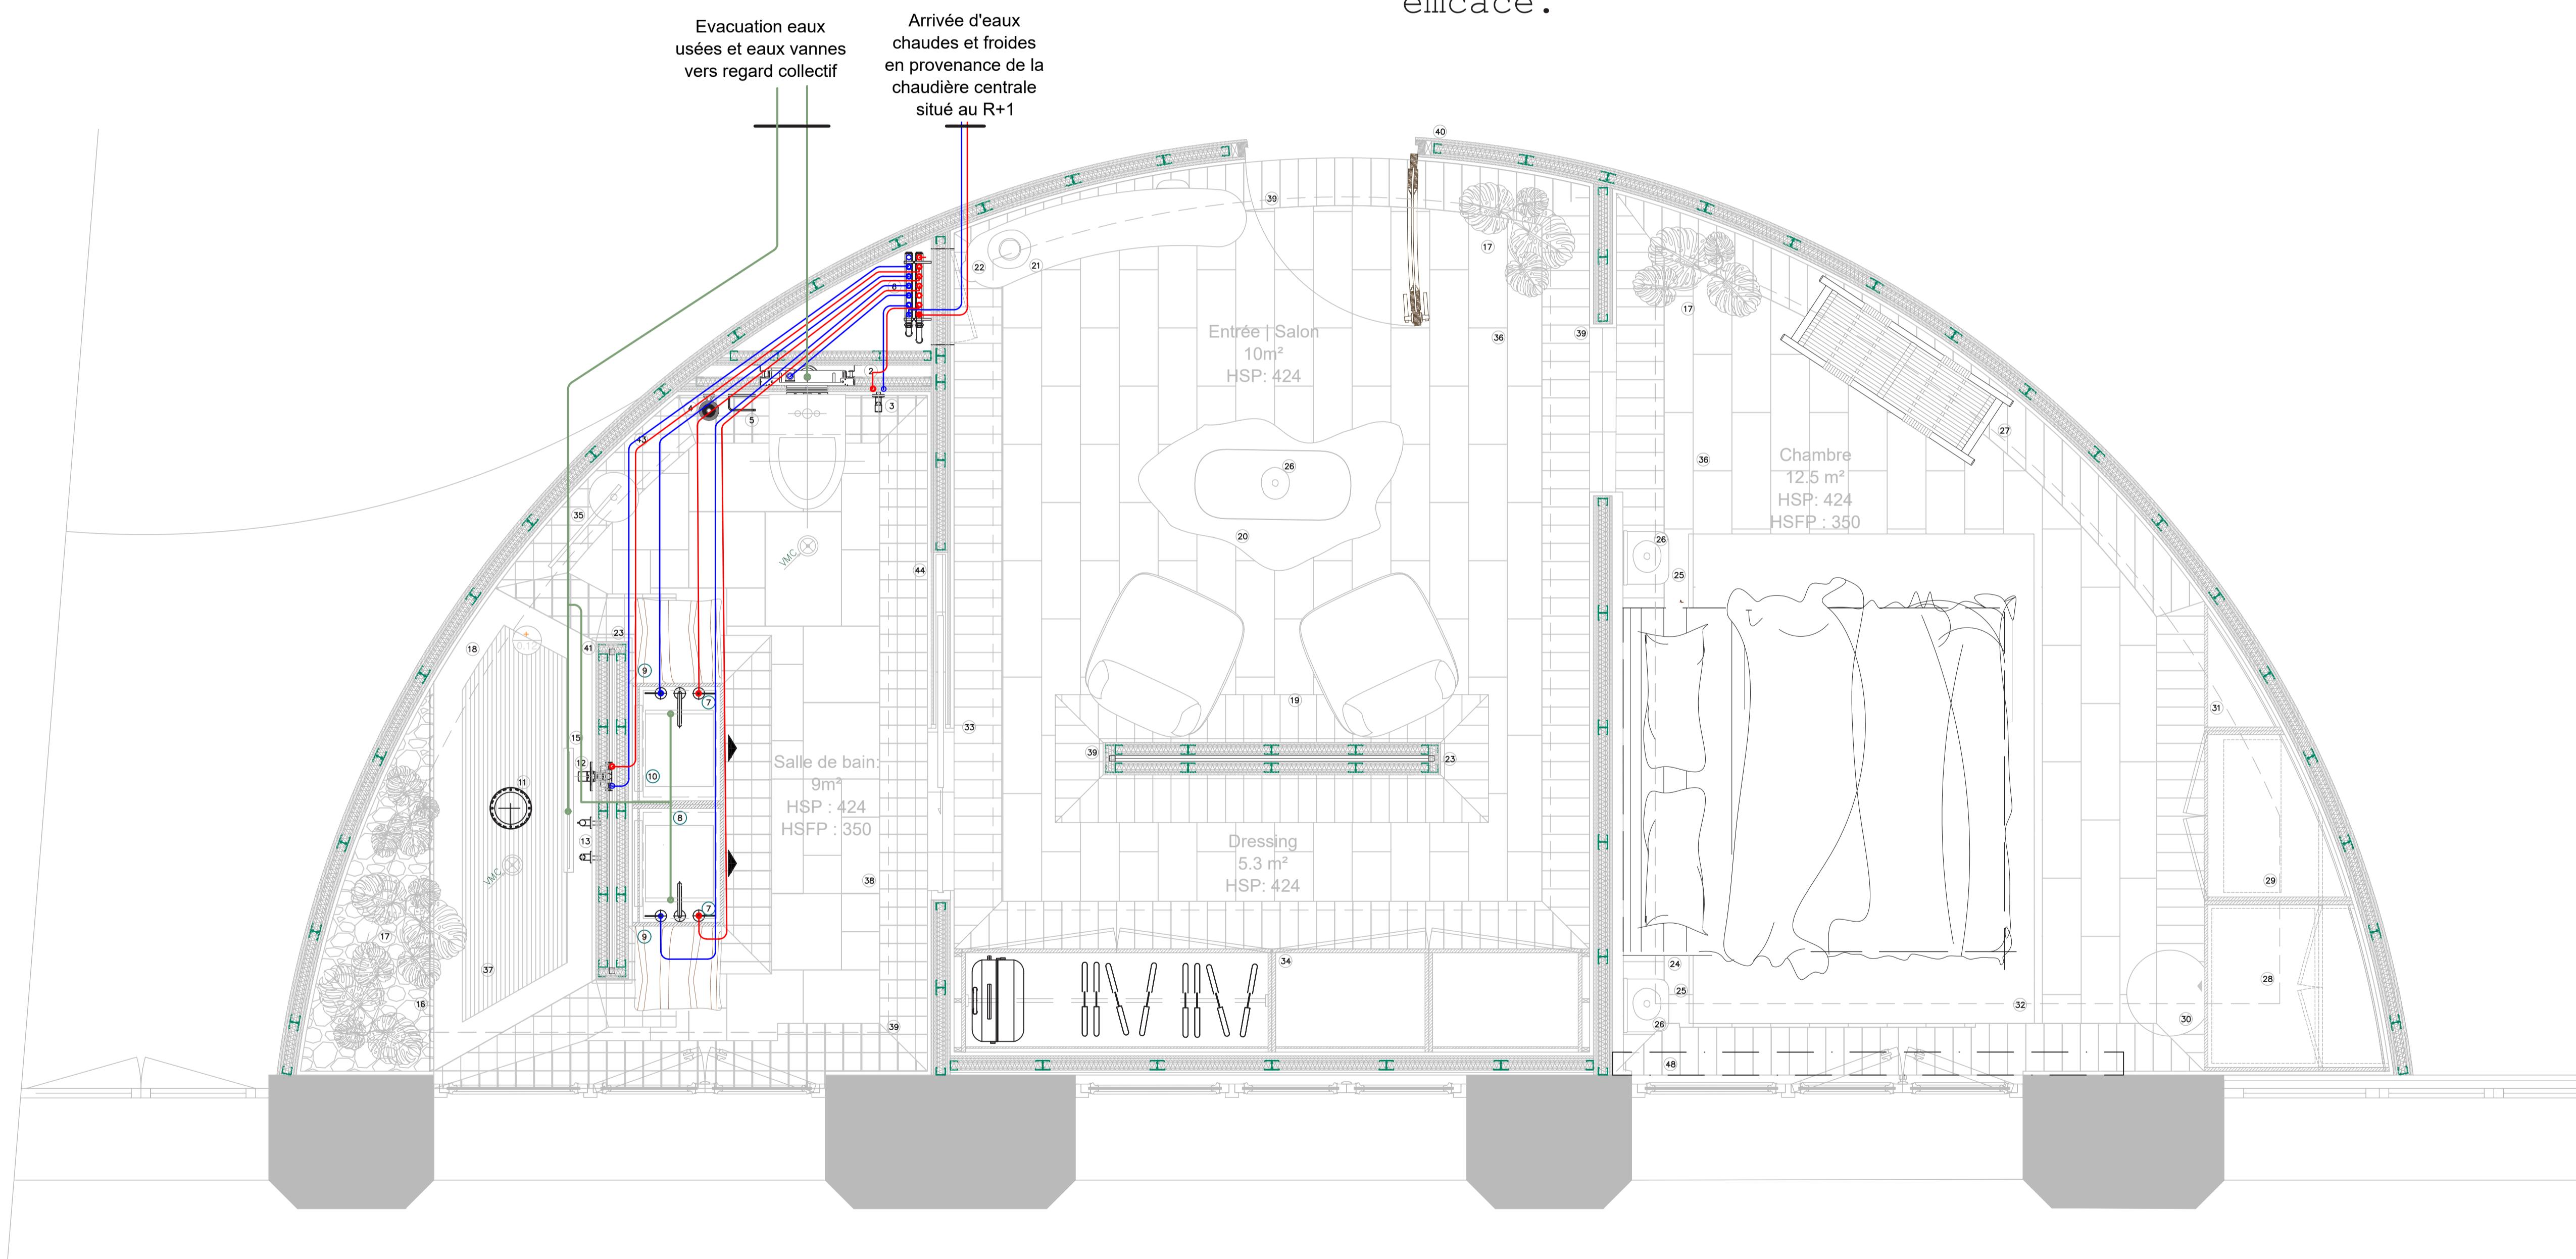


Ici, le système de distribution de l'eau fonctionne de la manière suivante : l'eau chaude est raccordée à la chaudière centrale, puis redistribuée vers une nourrice principale. De là, elle est dirigée vers chaque nourrice présente dans chaque chambre, permettant ainsi une distribution efficace.

Pour le système d'évacuation des eaux usées et des eaux vannes, celles-ci sont acheminées vers un regard collectif, lequel est connecté au collecteur public. Cela assure une gestion centralisée et efficace des eaux usées.

I
II
III
IV
V
VI
VII
VIII

PLAN COULEUR

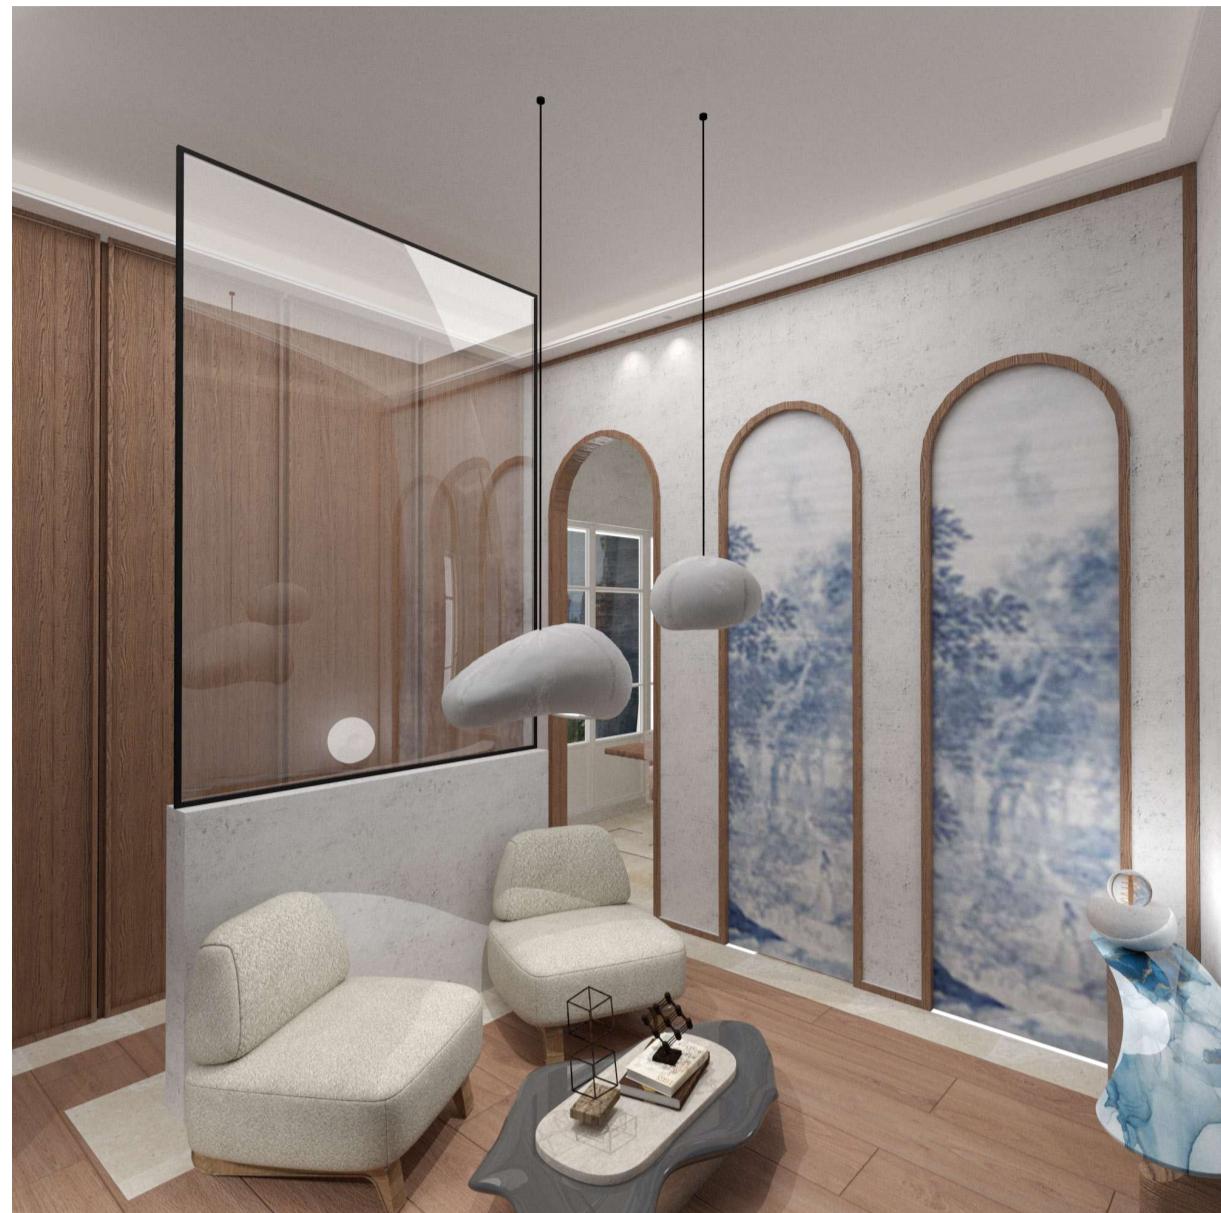

COUPE COULEUR





Ces images en 3D représentent notre chambre d'hôtel. On y perçoit clairement l'atmosphère chaleureuse et reposante du style méditerranéen.

Les tons terreux, les matériaux naturels et les touches de bleu évoquent la mer et le soleil, créant une ambiance propice à la détente.



I
II
III

IV
V
VI
VII
VIII

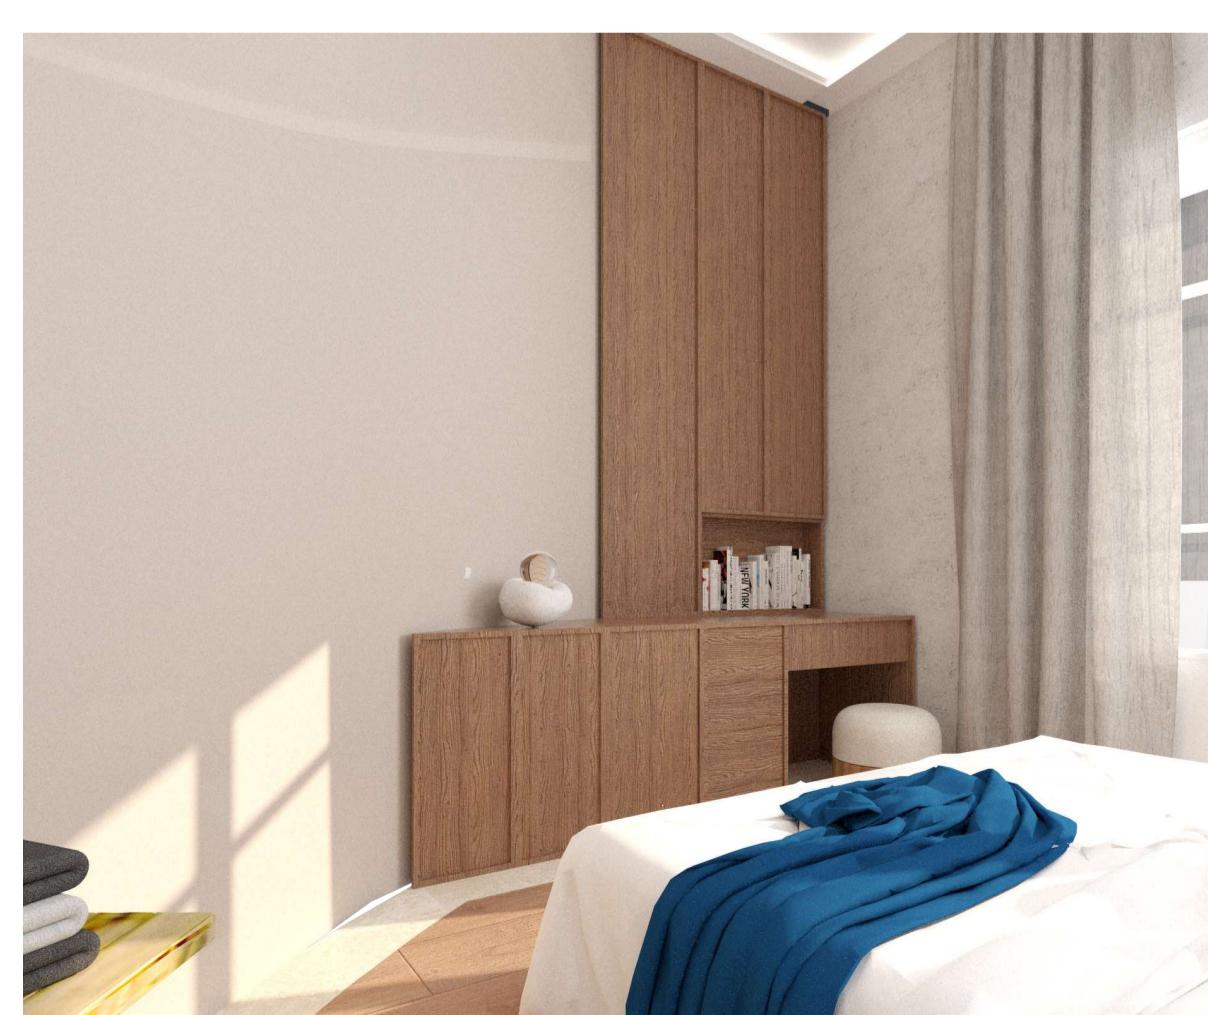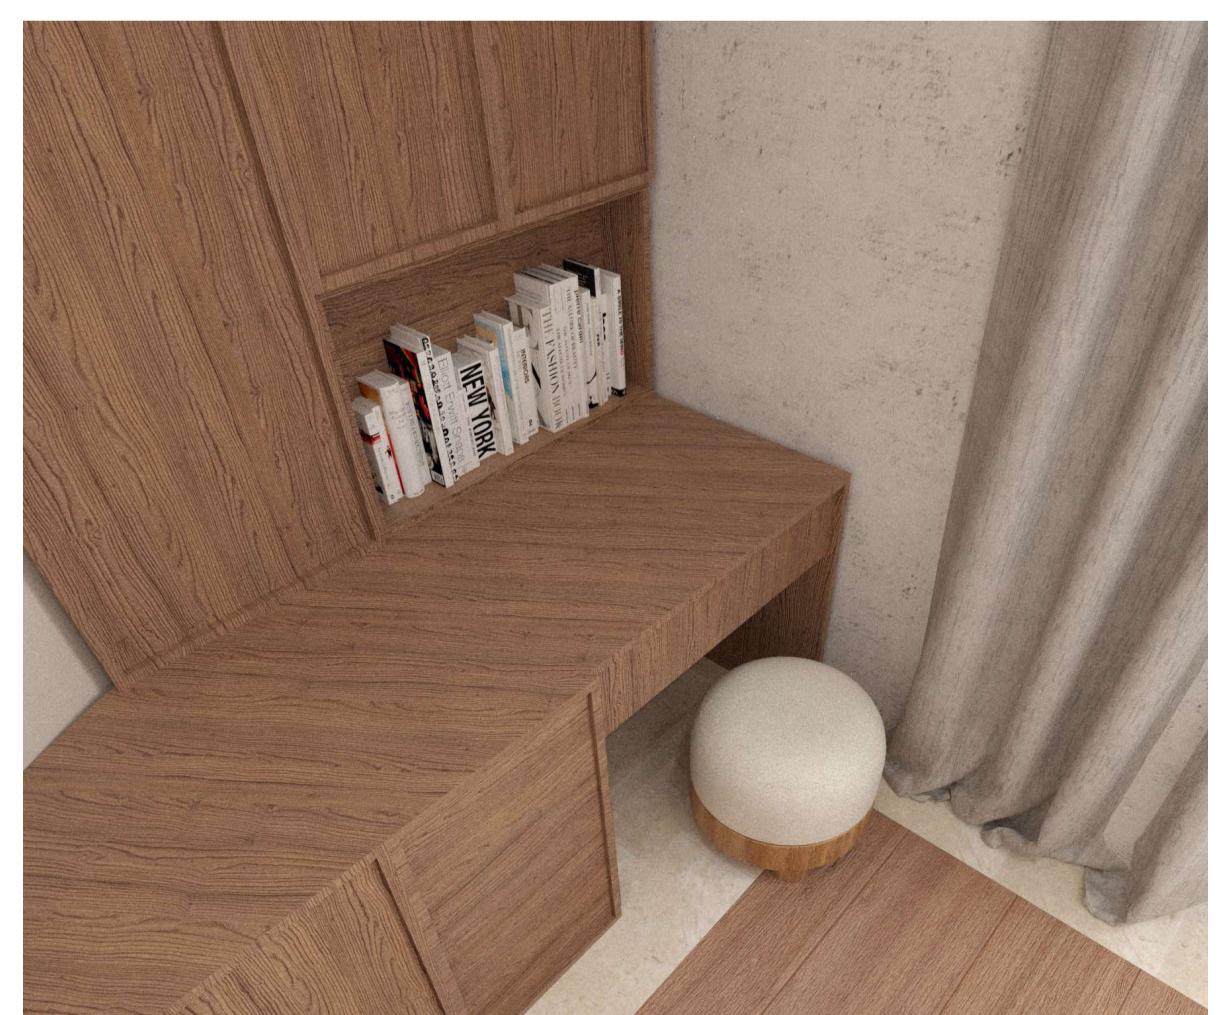

COUPE COULEUR



Ces images en 3D représentent notre salle d'eau d'hôtel. On y perçoit clairement l'atmosphère chaleureuse et reposante du style méditerranéen, avec des murs en pierre, une douche moderne, des plantes verdoyantes et des éléments en bois. L'ensemble crée un espace harmonieux et apaisant, parfait pour se ressourcer.